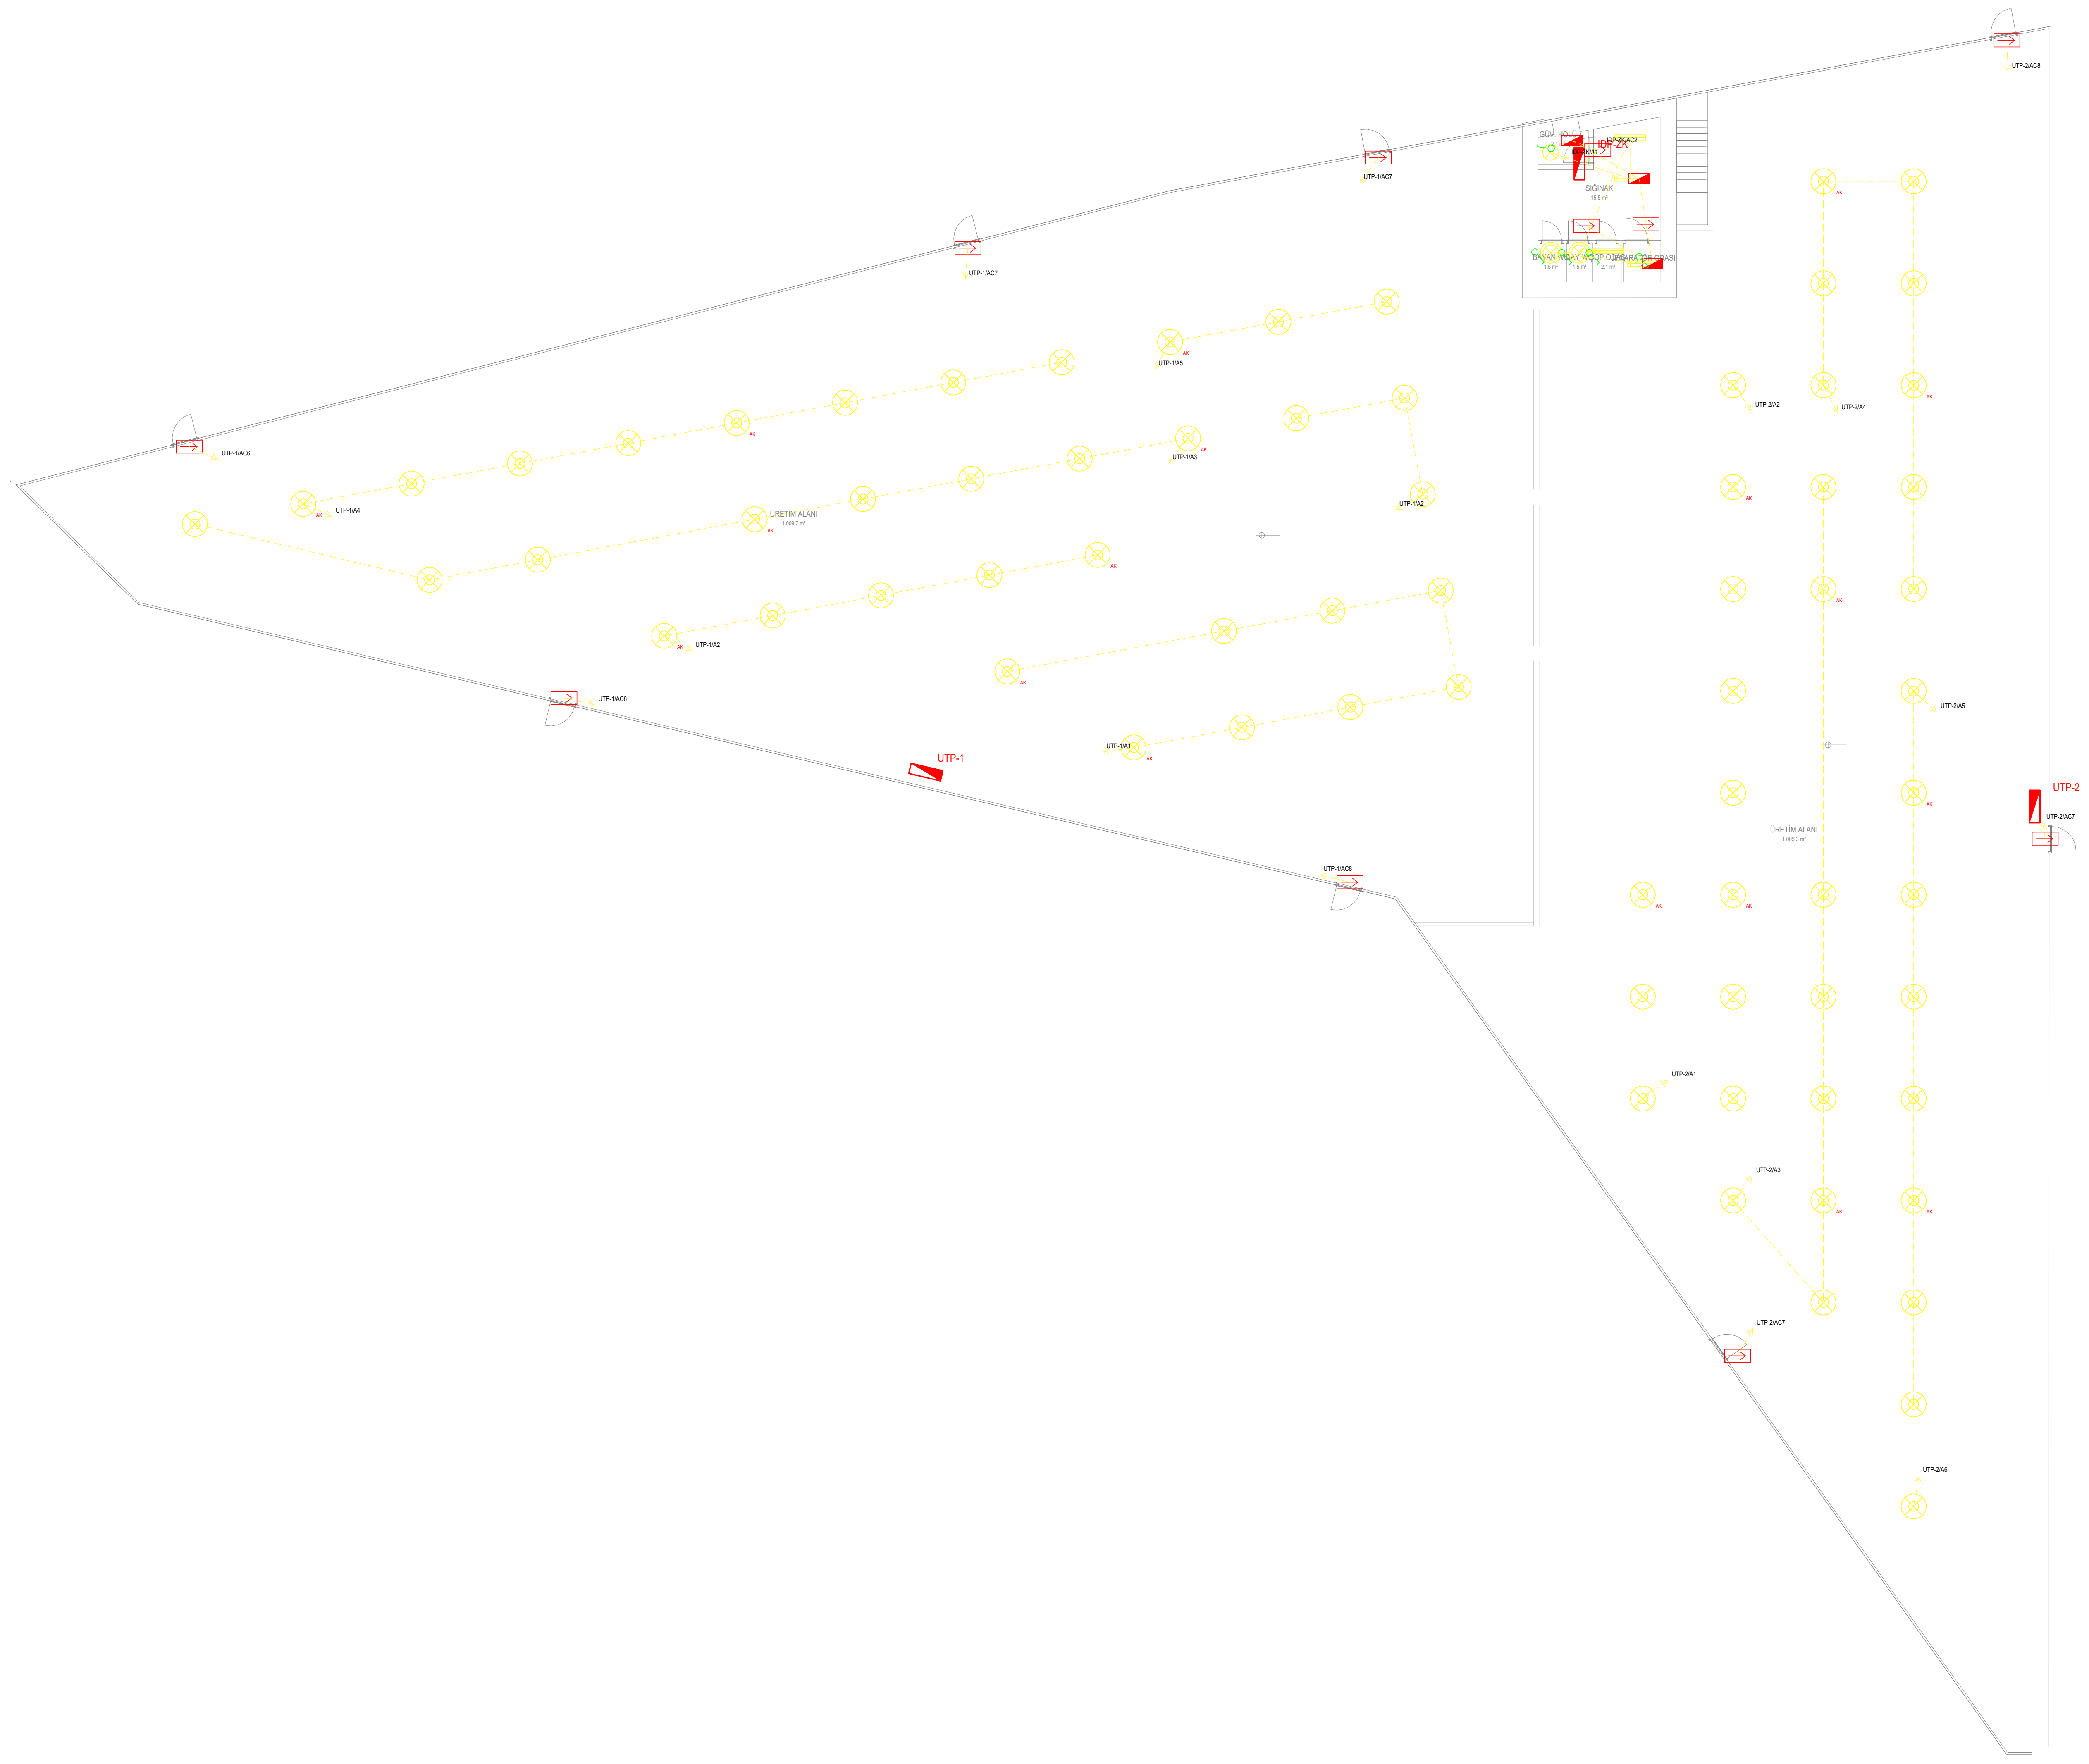

LEJANT

⊗	LED yüksek tavan (highbay) armatürü 150 W, 21.000 lm, IP65
☒	LED panel armatür 60x60, 36 W, 3.600 lm, UGR<19
⊗	LED downlight 18 W, 1.800 lm, IP20
⊗	LED downlight 12 W, 1.200 lm, IP44 (ıslak hacim)
▭	LED etanj armatür 36 W, 4.000 lm, IP65
◪	LED acil aydınlatma armatürü 3 W, 3 saat, sürekli/sürekli olmayan
⇥	LED çıkış/yönlendirme armatürü 3 W, 3 saat
	AK: 3 saat acil kitli armatür (sürekli faz ile beslenir)
⌐o	Adi anahtar (h=110 cm)
<o	Komütatör anahtar
⌐o⌐	Vavien anahtar
◪	Tali dağıtım panosu (UTP / İDP)
— — —	Aydınlatma linyesi, ok: panoya dönüş, etiket PANO/LİNYE

AYDINLATMA TESİSATI PLANI

ZEMİN KAT PLANI - Ö: 1/100

Parsel 2 | BROSCO İTHALAT İHRACAT VE TİCARET ANONİM ŞİRKETİ

CLD - 19.10.2026 - mimari altlık: BROSCO 2 NOLU PARSEL MİMARİ.dwg

İŞİN ADI	ELEKTRİK İÇ TESİSAT PROJESİ
YAPI SAHİBİ	BROSCO İTHALAT İHRACAT VE TİCARET ANONİM ŞİRKETİ
ADRES	YUKARI MAHALLE / KEMALPAŞA / İZMİR - Ada: ...... Parsel: 2
PAFTA ADI	AYDINLATMA TESİSATI PLANI - ZEMİN KAT PLANI
ÖLÇEK / TARİH / PAFTA NO	1/100 | 19.10.2026 | 01-01
PROJE MÜELLİFİ	Elektrik Mühendisi - Adı Soyadı: ....
ODA SİCİL / SMM NO	EMO Sicil No: .... SMM Belge No: .... İmza: ....

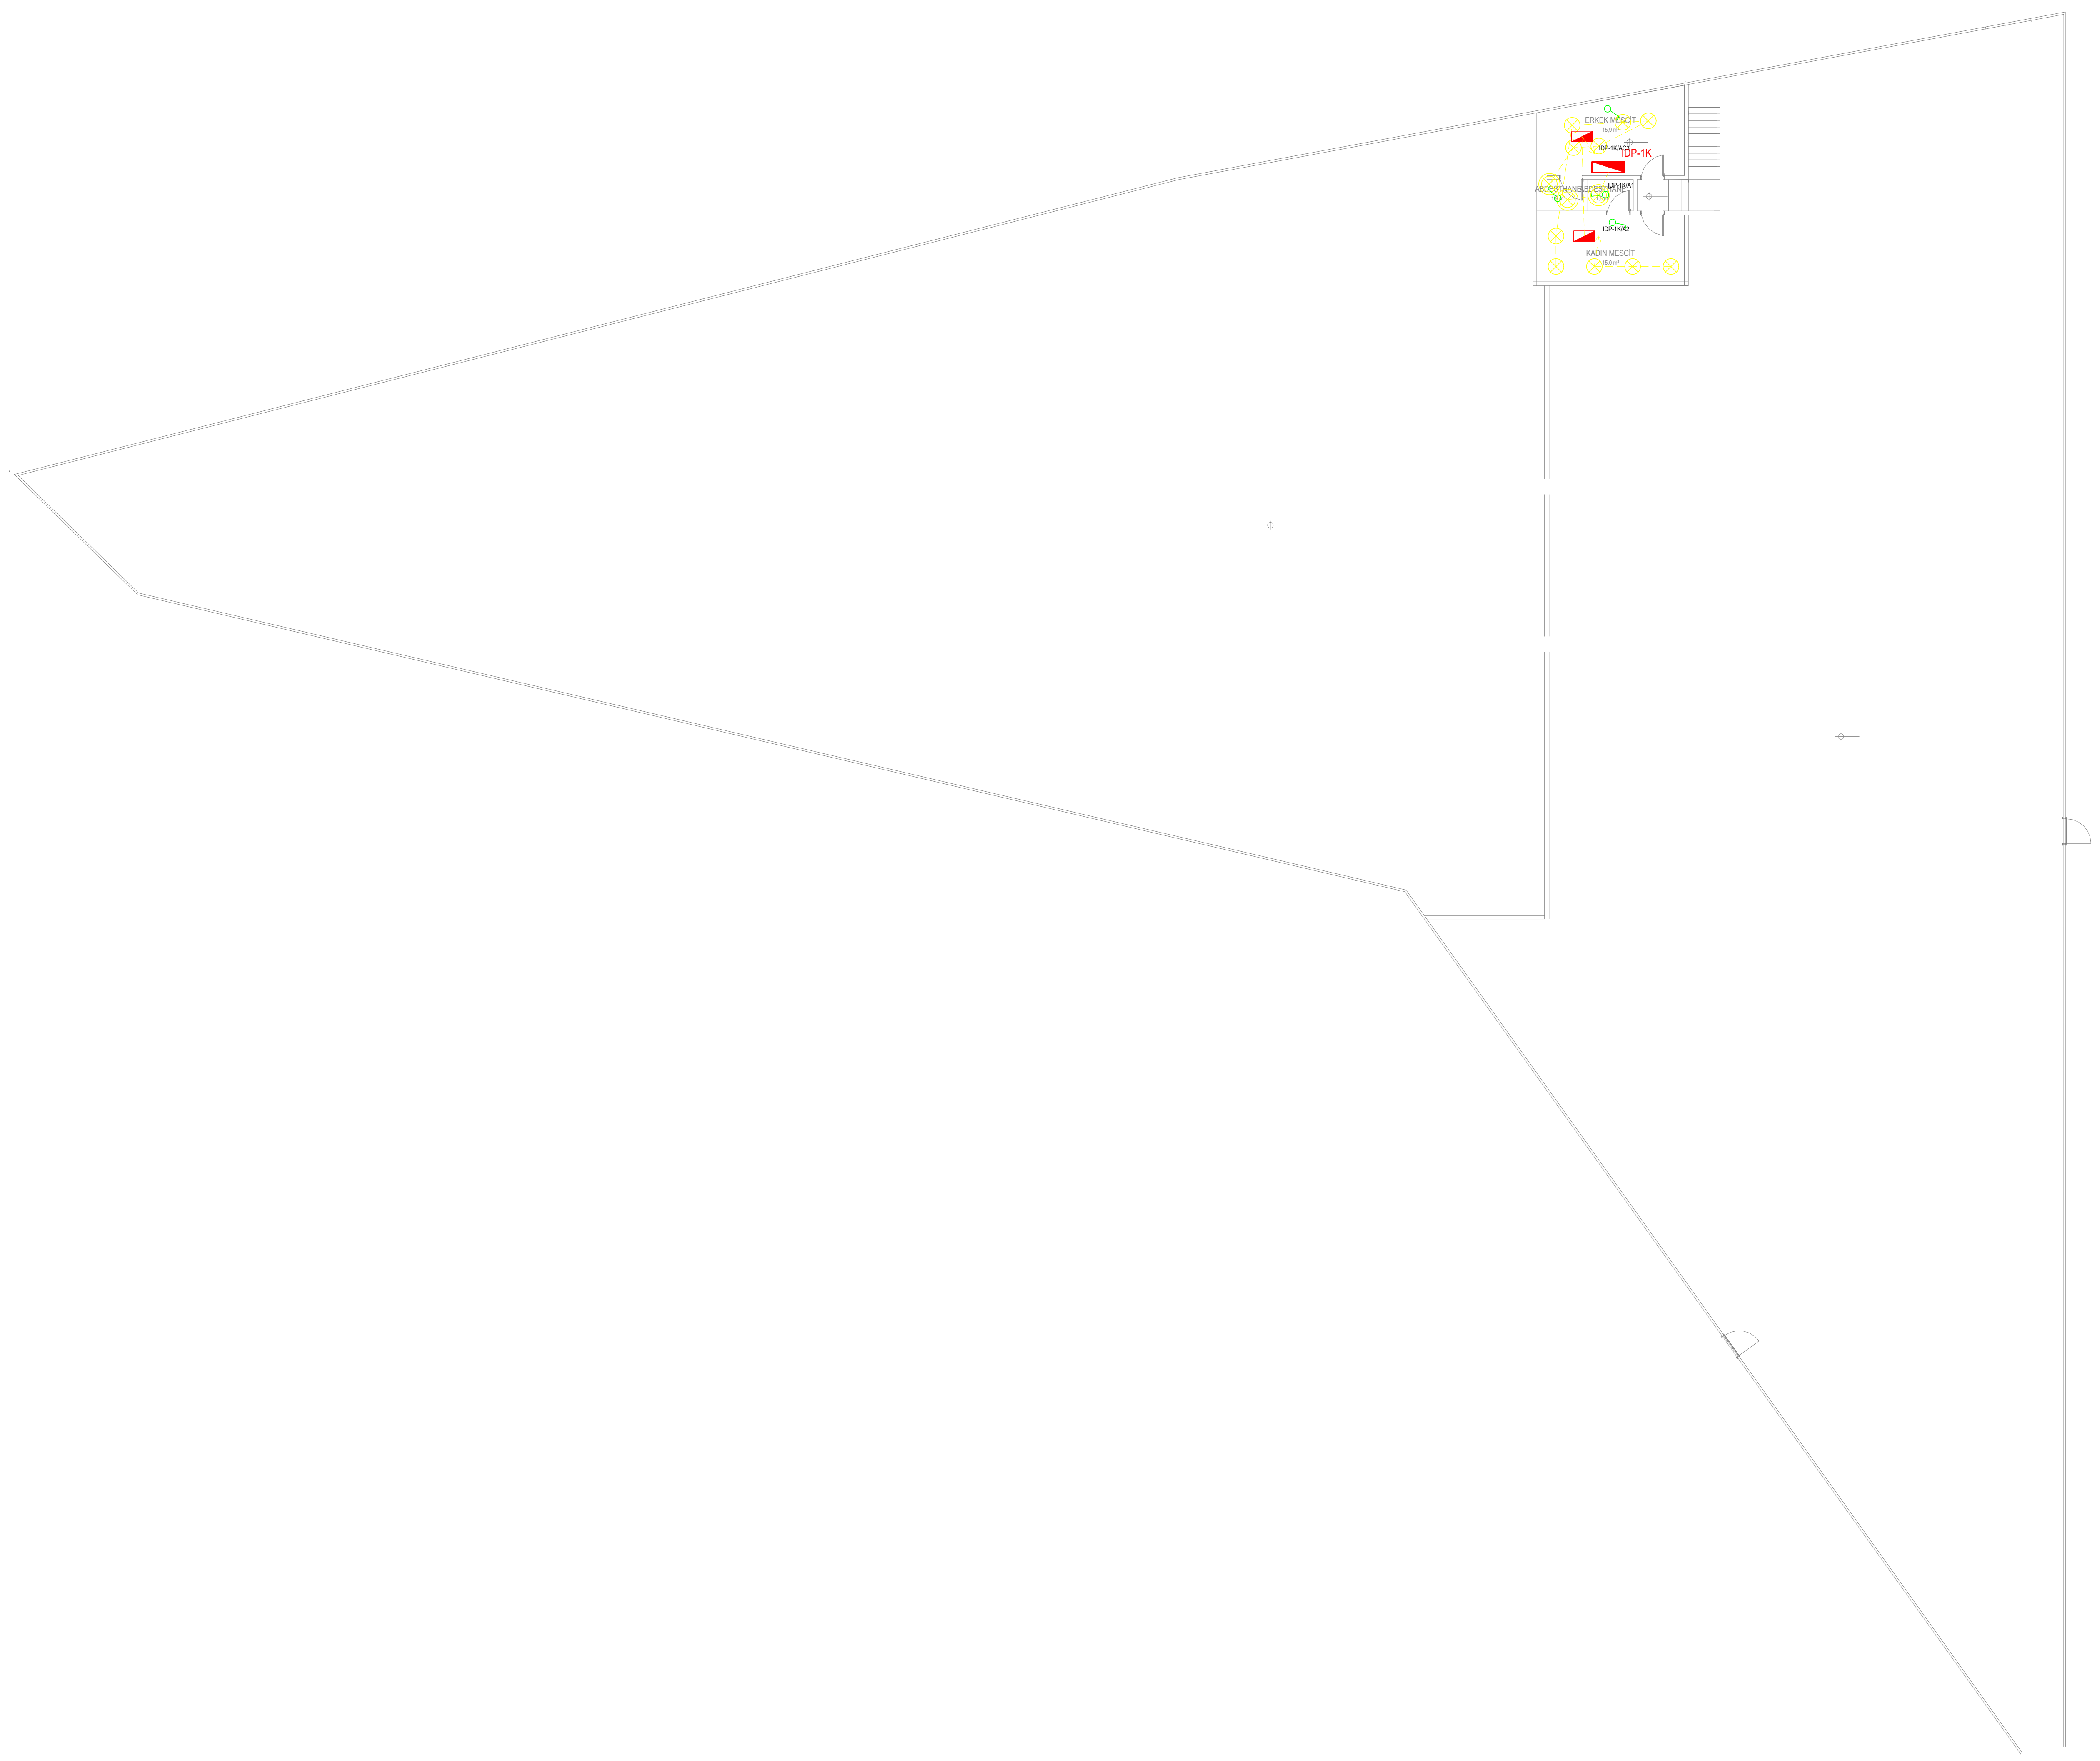

LEJANT

⊗	LED yüksek tavan (highbay) armatürü 150 W, 21.000 lm, IP65
☒	LED panel armatür 60x60, 36 W, 3.600 lm, UGR<19
⊗	LED downlight 18 W, 1.800 lm, IP20
⊗	LED downlight 12 W, 1.200 lm, IP44 (ıslak hacim)
▭	LED etanj armatür 36 W, 4.000 lm, IP65
◪	LED acil aydınlatma armatürü 3 W, 3 saat, sürekli/sürekli olmayan
→	LED çıkış/yönlendirme armatürü 3 W, 3 saat
	AK: 3 saat acil kitli armatür (sürekli faz ile beslenir)
	Adi anahtar (h=110 cm)
	Komütatör anahtar
	Vavien anahtar
◪	Tali dağıtım panosu (UTP / İDP)
— — —	Aydınlatma linyesi, ok: panoya dönüş, etiket PANO/LİNYE

AYDINLATMA TESİSATI PLANI

1. KAT PLANI - Ö: 1/100

Parsel 2 | BROSCO İTHALAT İHRACAT VE TİCARET ANONİM ŞİRKETİ

CLD - 19.10.2026 - mimari altlık: BROSCO 2 NOLU PARSEL MİMARİ.dwg

İŞİN ADI	ELEKTRİK İÇ TESİSAT PROJESİ
YAPI SAHİBİ	BROSCO İTHALAT İHRACAT VE TİCARET ANONİM ŞİRKETİ
ADRES	YUKARI MAHALLE / KEMALPAŞA / İZMİR - Ada: ...... Parsel: 2
PAFTA ADI	AYDINLATMA TESİSATI PLANI - 1. KAT PLANI
ÖLÇEK / TARİH / PAFTA NO	1/100 | 19.10.2026 | 01-02
PROJE MÜELLİFİ	Elektrik Mühendisi - Adı Soyadı: ....
ODA SİCİL / SMM NO	EMO Sicil No: .... SMM Belge No: .... İmza: ....

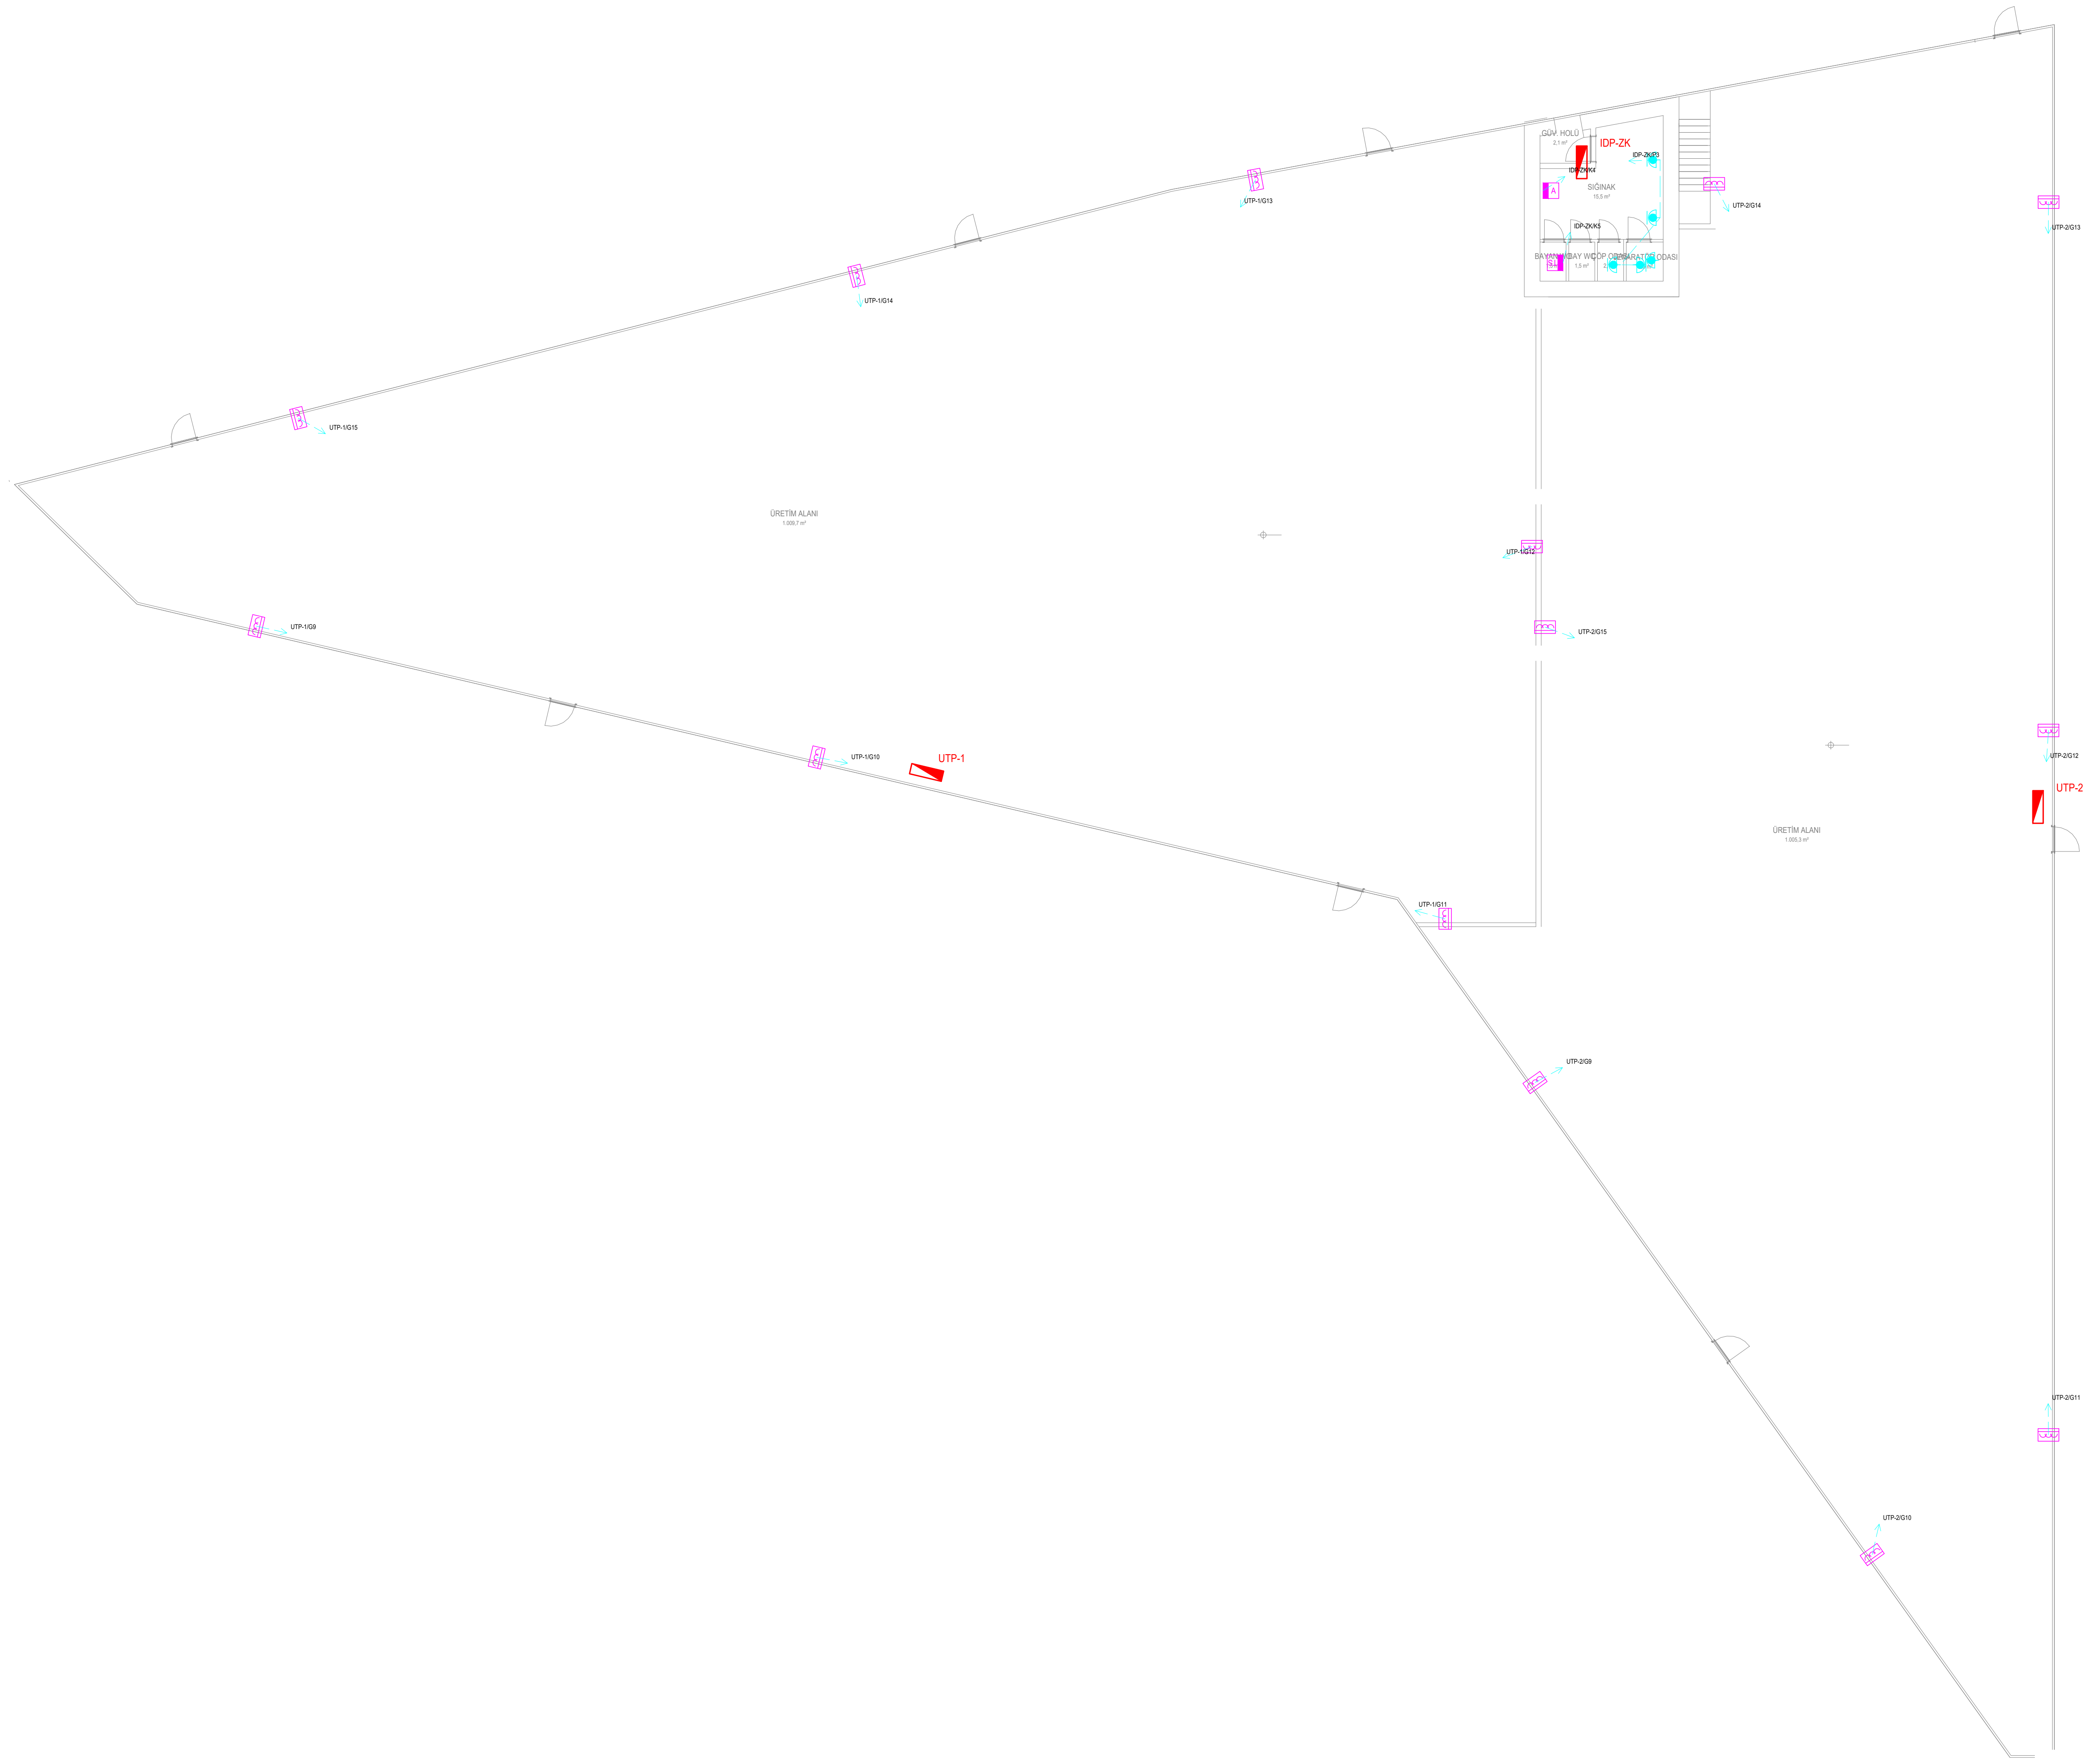

LEJANT

	Topraklı priz 16 A (h=40 cm, tezgah h=110 cm)
U	Bilgisayar prizi (ayrı linye, UPS hazırlığı)
●	Etanj priz IP44
	Endüstriyel priz grubu CEE 32A+16A+2x16A (iç koruma, h=150 cm)
IS	Ani su ısıtıcı çıkışı (IS) - ayrı linye
TS	Elektrikli termosifon çıkışı (TS) - ayrı linye
B	Bulaşık makinesi çıkışı (B) - ayrı linye
A	Havalandırma cihazı / aspiratör çıkışı (A) - ayrı linye
	Tali dağıtım panosu (UTP / İDP)
— —	Priz / kuvvet linyesi, ok: panoya dönüş

PRİZ VE KUVVET TESİSATI PLANI

ZEMİN KAT PLANI - Ö: 1/100

Parsel 2 | BROSCO İTHALAT İHRACAT VE TİCARET ANONİM ŞİRKETİ

CLD - 19.10.2026 - mimari altlık: BROSCO 2 NOLU PARSEL MİMARİ.dwg

İŞİN ADI	ELEKTRİK İÇ TESİSAT PROJESİ
YAPI SAHİBİ	BROSCO İTHALAT İHRACAT VE TİCARET ANONİM ŞİRKETİ
ADRES	YUKARI MAHALLE / KEMALPAŞA / İZMİR - Ada: ...... Parsel: 2
PAFTA ADI	PRİZ VE KUVVET TESİSATI PLANI - ZEMİN KAT PLANI
ÖLÇEK / TARİH / PAFTA NO	1/100 | 19.10.2026 | 01-03
PROJE MÜELLİFİ	Elektrik Mühendisi - Adı Soyadı: ....
ODA SİCİL / SMM NO	EMO Sicil No: .... SMM Belge No: .... İmza: ....

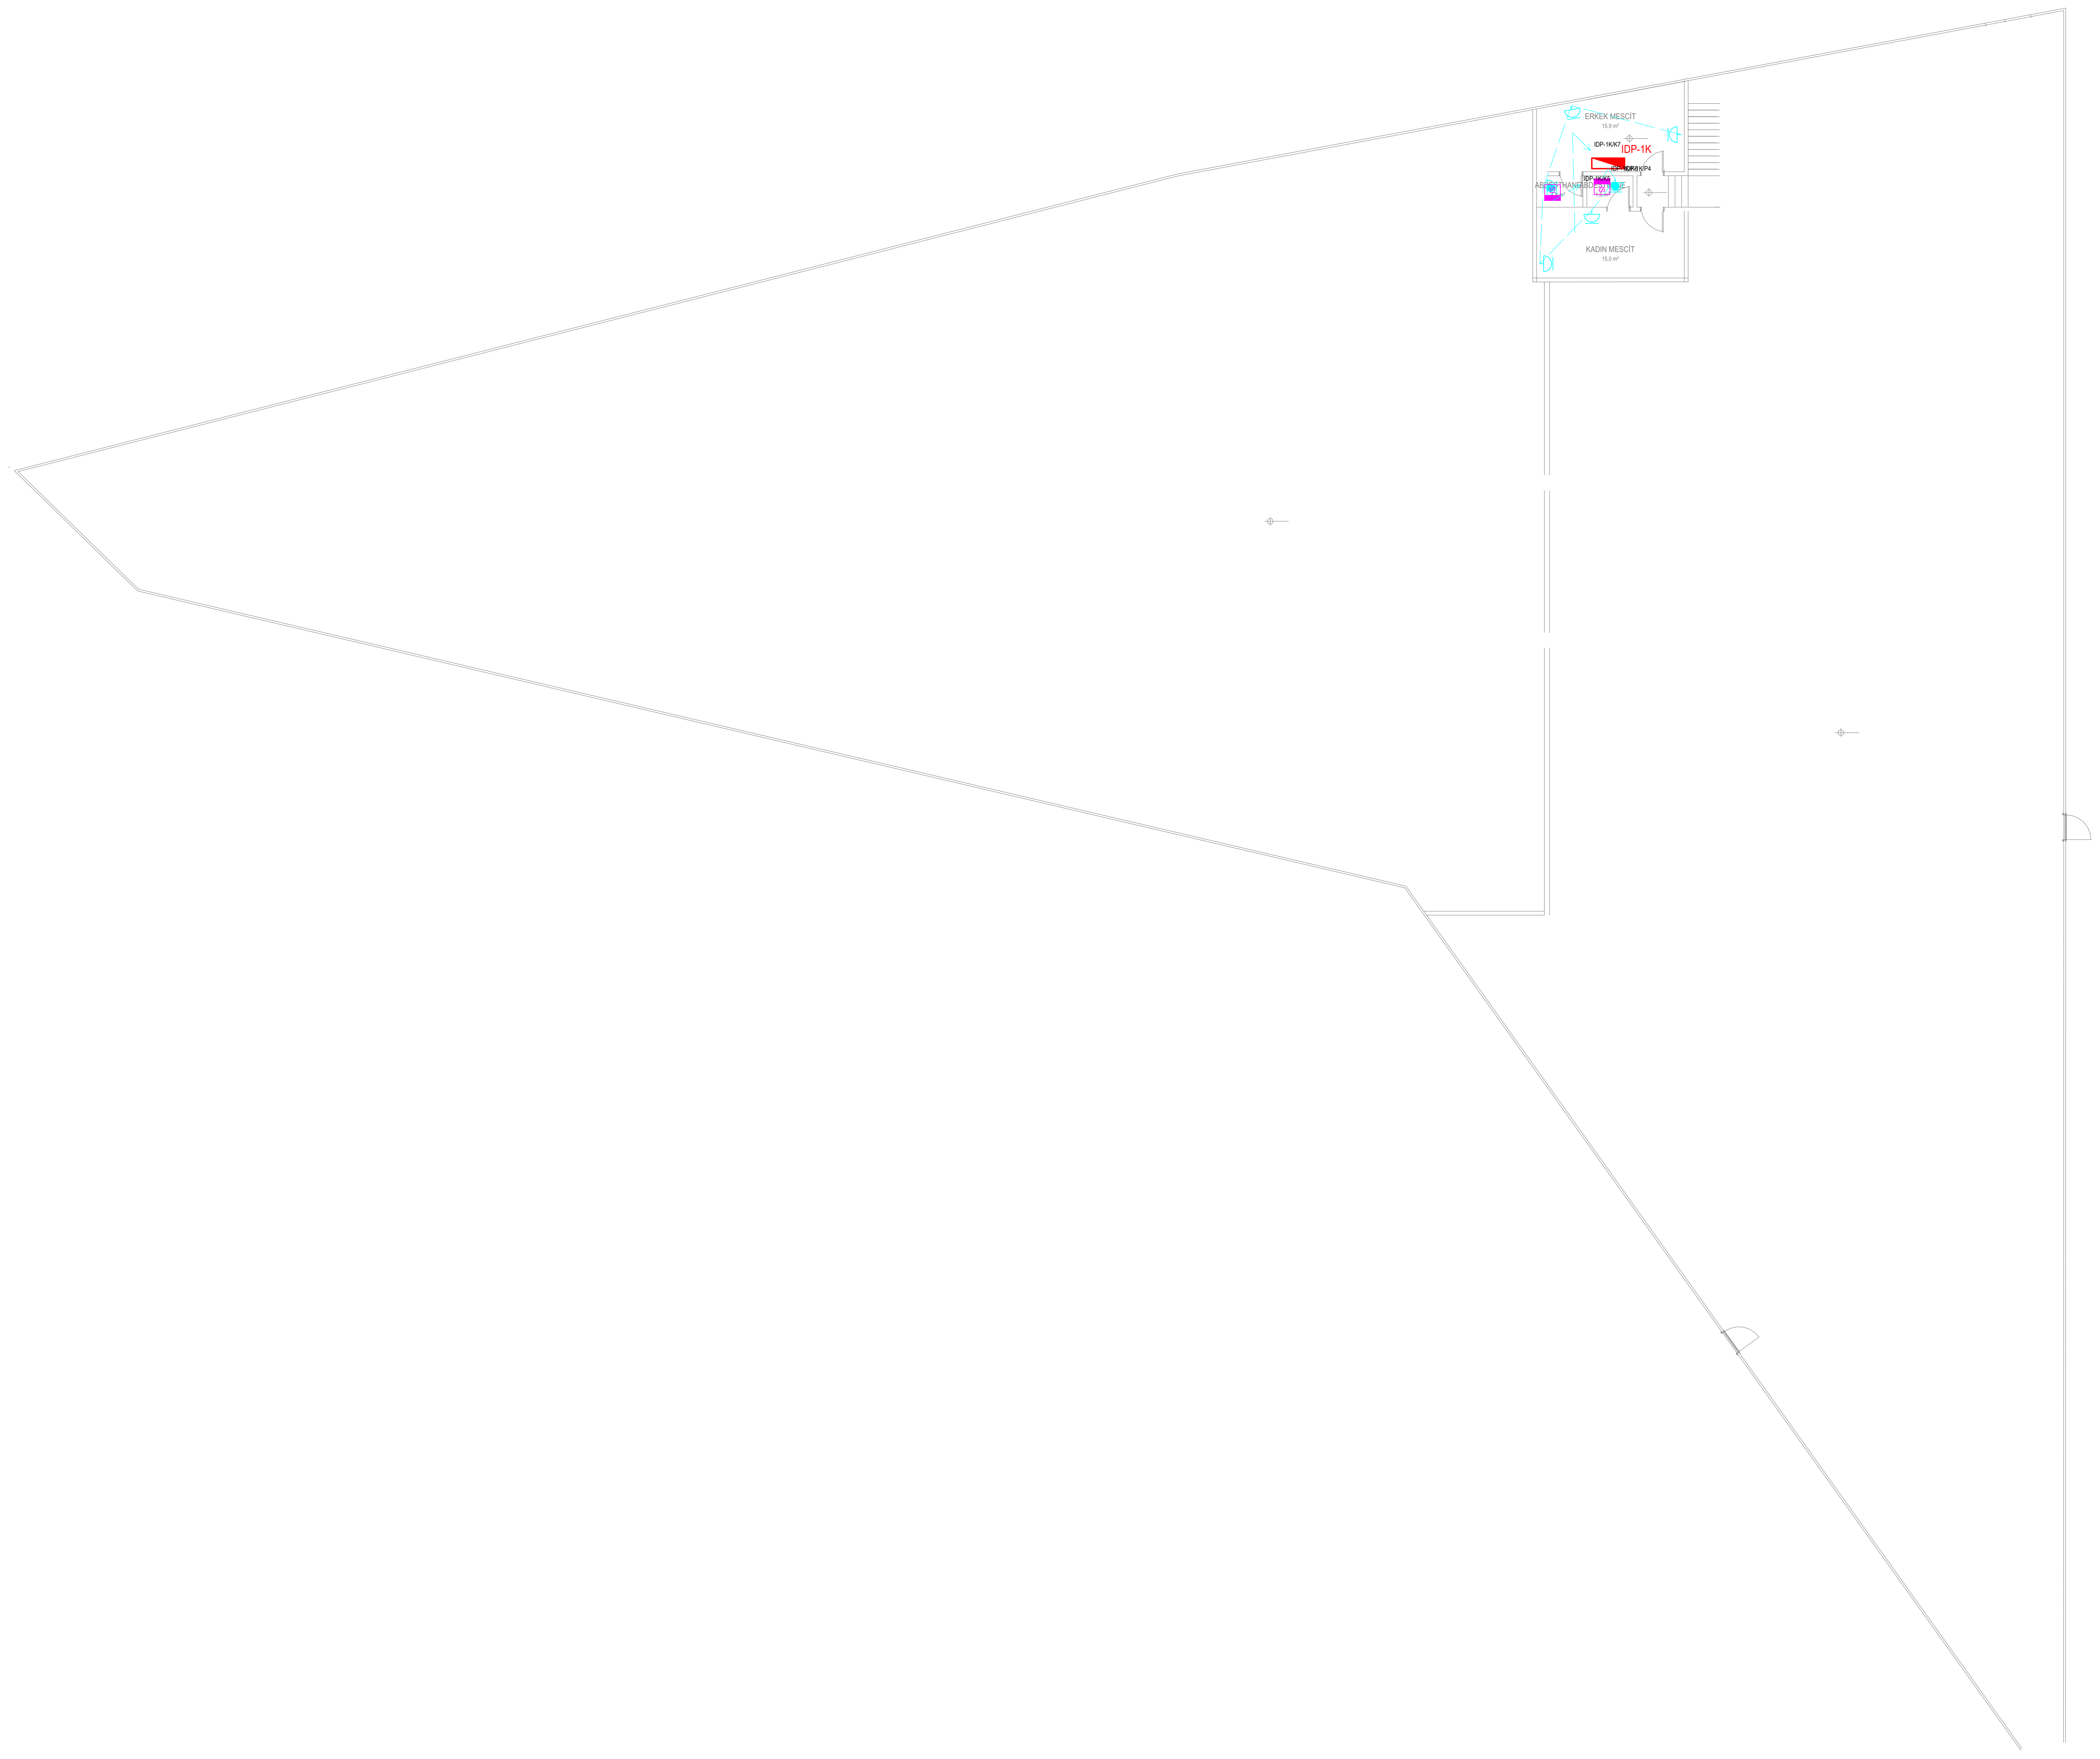

LEJANT

	Topraklı priz 16 A (h=40 cm, tezgah h=110 cm)
U	Bilgisayar prizi (ayrı linye, UPS hazırlığı)
●	Etanj priz IP44
	Endüstriyel priz grubu CEE 32A+16A+2x16A (iç koruma, h=150 cm)
IS	Ani su ısıtıcı çıkışı (IS) - ayrı linye
TS	Elektrikli termosifon çıkışı (TS) - ayrı linye
B	Bulaşık makinesi çıkışı (B) - ayrı linye
A	Havalandırma cihazı / aspiratör çıkışı (A) - ayrı linye
◩	Tali dağıtım panosu (UTP / İDP)
— — —	Priz / kuvvet linyesi, ok: panoya dönüş

PRİZ VE KUVVET TESİSATI PLANI

1. KAT PLANI - Ö: 1/100

Parsel 2 | BROSCO İTHALAT İHRACAT VE TİCARET ANONİM ŞİRKETİ

CLD - 19.10.2026 - mimari altlık: BROSCO 2 NOLU PARSEL MİMARİ.dwg

İŞİN ADI	ELEKTRİK İÇ TESİSAT PROJESİ
YAPI SAHİBİ	BROSCO İTHALAT İHRACAT VE TİCARET ANONİM ŞİRKETİ
ADRES	YUKARI MAHALLE / KEMALPAŞA / İZMİR - Ada: ...... Parsel: 2
PAFTA ADI	PRİZ VE KUVVET TESİSATI PLANI - 1. KAT PLANI
ÖLÇEK / TARİH / PAFTA NO	1/100 | 19.10.2026 | 01-04
PROJE MÜELLİFİ	Elektrik Mühendisi - Adı Soyadı: ....
ODA SİCİL / SMM NO	EMO Sicil No: .... SMM Belge No: .... İmza: ....

LEJANT

⊗	LED yüksek tavan (highbay) armatürü 150 W, 21.000 lm, IP65
⊠	LED panel armatür 60x60, 36 W, 3.600 lm, UGR<19
⊗	LED downlight 18 W, 1.800 lm, IP20
⊗	LED downlight 12 W, 1.200 lm, IP44 (ıslak hacim)
▭	LED etanj armatür 36 W, 4.000 lm, IP65
◪	LED acil aydınlatma armatürü 3 W, 3 saat, sürekli/sürekli olmayan
⇨	LED çıkış/yönlendirme armatürü 3 W, 3 saat
	AK: 3 saat acil kitli armatür (sürekli faz ile beslenir)
○	Adi anahtar (h=110 cm)
○	Komütatör anahtar
○	Vavien anahtar
◩	Tali dağıtım panosu (UTP / İDP)
— — —	Aydınlatma linyesi, ok: panoya dönüş, etiket PANO/LİNYE
◗	Topraklı priz 16 A (h=40 cm, tezgah h=110 cm)
◗ U	Bilgisayar prizi (ayrı linye, UPS hazırlığı)
●	Etanj priz IP44
▭	Endüstriyel priz grubu CEE 32A+16A+2x16A (iç koruma, h=150 cm)
IS	Ani su ısıtıcı çıkışı (IS) - ayrı linye
TS	Elektrikli termosifon çıkışı (TS) - ayrı linye
B	Bulaşık makinesi çıkışı (B) - ayrı linye
A	Havalandırma cihazı / aspiratör çıkışı (A) - ayrı linye
— — —	Priz / kuvvet linyesi, ok: panoya dönüş

LİNYE LİSTESİ (1)

PANO	LİNYE	TÜR	AÇIKLAMA	ADET	GÜÇ (W)	FAZ	SİGORTA	KAÇAK AKIM	KABLO	L (m)	%e
IDP-ZK	A1	Aydınlatma	Aydınlatma	7	186	T	B10A	30 mA	NYM 3x1,5 mm²	23,6	0,20
IDP-ZK	AC2	Acil ayd.	Acil aydınlatma / yönlendirme	6	18	T	B10A	30 mA	NYM 3x1,5 mm²	15,6	0,01
IDP-ZK	P3	Priz	Priz	5	1.500	S	B16A	30 mA	NYM 3x2,5 mm²	13,2	0,53
IDP-ZK	K4	Kuvvet	Sığınak havalandırma cihazı	1	750	T	B10A	30 mA	NYM 3x1,5 mm²	5,3	0,18
IDP-ZK	K5	Kuvvet	Elektrikli termosifon 80 L 2 kW	1	2.000	R	B16A	30 mA	NYM 3x2,5 mm²	7,6	0,41
UTP-2	A1	Aydınlatma	Aydınlatma (yüksek tavan, AK: sürekli faz)	3	450	S	B10A	30 mA	NYM 4x1,5 mm²	36,8	0,74
UTP-2	A2	Aydınlatma	Aydınlatma (yüksek tavan, AK: sürekli faz)	8	1.200	R	B16A	30 mA	NYM 4x4 mm²	60,5	1,23
UTP-2	A3	Aydınlatma	Aydınlatma (yüksek tavan, AK: sürekli faz)	8	1.200	S	B16A	30 mA	NYM 4x4 mm²	70,1	1,42
UTP-2	A4	Aydınlatma	Aydınlatma (yüksek tavan, AK: sürekli faz)	8	1.200	T	B16A	30 mA	NYM 4x4 mm²	57,9	1,17
UTP-2	A5	Aydınlatma	Aydınlatma (yüksek tavan, AK: sürekli faz)	8	1.200	R	B16A	30 mA	NYM 4x2,5 mm²	45,1	1,46
UTP-2	A6	Aydınlatma	Aydınlatma (yüksek tavan)	1	150	T	B10A	30 mA	NYM 3x1,5 mm²	37,4	0,25
UTP-2	AC7	Acil ayd.	Acil aydınlatma / yönlendirme	2	6	T	B10A	30 mA	NYM 3x1,5 mm²	31,0	0,01
UTP-2	AC8	Acil ayd.	Acil aydınlatma / yönlendirme	1	3	T	B10A	30 mA	NYM 3x1,5 mm²	36,9	0,00
UTP-2	G9	End. priz	End. priz grubu (4P C32+C16+2xB16)	1	5.000	RST	C32A	30 mA A tipi (kutu içi)	NYM 5x10 mm²	28,5	0,35
UTP-2	G10	End. priz	End. priz grubu (4P C32+C16+2xB16)	1	5.000	RST	C32A	30 mA A tipi (kutu içi)	NYM 5x10 mm²	36,8	0,45
UTP-2	G11	End. priz	End. priz grubu (4P C32+C16+2xB16)	1	5.000	RST	C32A	30 mA A tipi (kutu içi)	NYM 5x10 mm²	30,7	0,38
UTP-2	G12	End. priz	End. priz grubu (4P C32+C16+2xB16)	1	5.000	RST	C32A	30 mA A tipi (kutu içi)	NYM 5x10 mm²	6,4	0,08
UTP-2	G13	End. priz	End. priz grubu (4P C32+C16+2xB16)	1	5.000	RST	C32A	30 mA A tipi (kutu içi)	NYM 5x10 mm²	29,6	0,36
UTP-2	G14	End. priz	End. priz grubu (4P C32+C16+2xB16)	1	5.000	RST	C32A	30 mA A tipi (kutu içi)	NYM 5x10 mm²	34,0	0,42
UTP-2	G15	End. priz	End. priz grubu (4P C32+C16+2xB16)	1	5.000	RST	C32A	30 mA A tipi (kutu içi)	NYM 5x10 mm²	26,3	0,32
UTP-2	K16	Kuvvet	Aydınlatma kumanda (kontaktör/saat rölesi)	1	50	T	B10A	30 mA	NYM 3x1,5 mm²	3,0	0,01
UTP-2	K17	Kuvvet	Seksiyonel kapı motoru (L≈25 m kabul)	1	750	RST	C10A	300 mA	NYM 5x1,5 mm²	25,0	0,14
UTP-1	A1	Aydınlatma	Aydınlatma (yüksek tavan, AK: sürekli faz)	8	1.200	R	B16A	30 mA	NYM 4x4 mm²	53,7	1,09
UTP-1	A2	Aydınlatma	Aydınlatma (yüksek tavan, AK: sürekli faz)	8	1.200	S	B16A	30 mA	NYM 4x4 mm²	62,4	1,26
UTP-1	A3	Aydınlatma	Aydınlatma (yüksek tavan, AK: sürekli faz)	8	1.200	T	B16A	30 mA	NYM 4x4 mm²	69,7	1,41
UTP-1	A4	Aydınlatma	Aydınlatma (yüksek tavan, AK: sürekli faz)	8	1.200	R	B16A	30 mA	NYM 4x4 mm²	70,1	1,42
UTP-1	A5	Aydınlatma	Aydınlatma (yüksek tavan, AK: sürekli faz)	3	450	S	B10A	30 mA	NYM 4x1,5 mm²	37,8	0,77
UTP-1	AC6	Acil ayd.	Acil aydınlatma / yönlendirme	2	6	T	B10A	30 mA	NYM 3x1,5 mm²	39,2	0,01
UTP-1	AC7	Acil ayd.	Acil aydınlatma / yönlendirme	2	6	T	B10A	30 mA	NYM 3x1,5 mm²	45,0	0,01
UTP-1	AC8	Acil ayd.	Acil aydınlatma / yönlendirme	1	3	T	B10A	30 mA	NYM 3x1,5 mm²	22,3	0,00
UTP-1	G9	End. priz	End. priz grubu (4P C32+C16+2xB16)	1	5.000	RST	C32A	30 mA A tipi (kutu içi)	NYM 5x10 mm²	33,2	0,41
UTP-1	G10	End. priz	End. priz grubu (4P C32+C16+2xB16)	1	5.000	RST	C32A	30 mA A tipi (kutu içi)	NYM 5x10 mm²	7,9	0,10
UTP-1	G11	End. priz	End. priz grubu (4P C32+C16+2xB16)	1	5.000	RST	C32A	30 mA A tipi (kutu içi)	NYM 5x10 mm²	26,7	0,33
UTP-1	G12	End. priz	End. priz grubu (4P C32+C16+2xB16)	1	5.000	RST	C32A	30 mA A tipi (kutu içi)	NYM 5x10 mm²	31,6	0,39
UTP-1	G13	End. priz	End. priz grubu (4P C32+C16+2xB16)	1	5.000	RST	C32A	30 mA A tipi (kutu içi)	NYM 5x10 mm²	33,1	0,41
UTP-1	G14	End. priz	End. priz grubu (4P C32+C16+2xB16)	1	5.000	RST	C32A	30 mA A tipi (kutu içi)	NYM 5x10 mm²	25,3	0,31
UTP-1	G15	End. priz	End. priz grubu (4P C32+C16+2xB16)	1	5.000	RST	C32A	30 mA A tipi (kutu içi)	NYM 5x10 mm²	34,8	0,43
UTP-1	K16	Kuvvet	Aydınlatma kumanda (kontaktör/saat rölesi)	1	50	T	B10A	30 mA	NYM 3x1,5 mm²	3,0	0,01
UTP-1	K17	Kuvvet	Seksiyonel kapı motoru (L≈25 m kabul)	1	750	RST	C10A	300 mA	NYM 5x1,5 mm²	25,0	0,14
IDP-1K	A1	Aydınlatma	Aydınlatma	10	162	T	B10A	30 mA	NYM 3x1,5 mm²	21,6	0,16
IDP-1K	A2	Aydınlatma	Aydınlatma	3	54	T	B10A	30 mA	NYM 3x1,5 mm²	10,5	0,03
IDP-1K	AC3	Acil ayd.	Acil aydınlatma / yönlendirme	2	6	T	B10A	30 mA	NYM 3x1,5 mm²	9,3	0,00
IDP-1K	P4	Priz	Priz	6	1.800	T	B16A	30 mA	NYM 3x2,5 mm²	20,6	1,00
IDP-1K	K5	Kuvvet	Ani su ısıtıcı 3,5 kW	1	3.500	R	B25A	30 mA	NYM 3x4 mm²	5,8	0,34
IDP-1K	K6	Kuvvet	Ani su ısıtıcı 3,5 kW	1	3.500	S	B25A	30 mA	NYM 3x4 mm²	3,5	0,21

LİNYE LİSTESİ (2)

PANO	LİNYE	TÜR	AÇIKLAMA	ADET	GÜÇ (W)	FAZ	SİGORTA	KAÇAK AKIM	KABLO	L (m)	%e
IDP-1K	K7	Kuvvet	VRF iç üniteleri besleme	2	220	T	B10A	30 mA A tipi	NYM 3x1,5 mm²	9,6	0,09

NOTLAR

1- Tesisat Elektrik İç Tesisleri Yönetmeliği, TS HD 60364 ve TS EN 12464-1 esas alınarak hesaplanmıştır.
2- Aydınlatma ve priz tesisatı ayrı paftalarda gösterilmiştir; linye etiketi "PANO/LİNYE", ok yönü panoyu gösterir.
3- Kesitler IEC 60364-5-52 C yöntemi x 0,80 (ofis) / x 0,71 (üretim holü tavası, 40 °C) ile seçilmiştir; gerilim düşümü aydınlatma ve prizde ≤ %1,5, kuvvette ≤ %3 olacak şekilde linyeler bölünmüştür.
4- Kaçak akım: tüm tek fazlı son devreler (priz, aydınlatma, ıslak hacim, özel çıkış) 30 mA, bilgisayar/VRF A tipi; 3 fazlı motor devreleri 300 mA; pano girişleri 300 mA S (seçici) - TS HD 60364-4-41 411.3.3, EMO.
5- Ofis ve ıslak hacimlerde sıva altı spiral boru, üretim alanında galvaniz kablo tavası / boru kullanılacaktır.
6- "AK" acil kitli armatürler kontaktör öncesinden sürekli faz ile beslenir (NYM 4x..: L anahtarlı + L sürekli, TS EN 50172).
7- Acil ve yönlendirme armatürleri 3 saat bataryalıdır (Binaların Yangından Korunması Hakkında Yönetmelik, TS EN 1838).
8- Endüstriyel priz grubu kutusu içinde 4P C32, C16 ve 2xB16 sigortalar ile 30 mA (A tipi) kaçak akım rölesi bulunur.
9- Anahtarlar sahada kapı açılış yönüne göre kapı kanadının arkasında kalmayacak şekilde yerleştirilecektir.
10- Üretim alanı aydınlatması tali panodan kontaktör + saat rölesi ile kumanda edilir.

HESAP TABLOLARI, CETVELLER VE NOTLAR

ELEKTRİK İÇ TESİSAT PROJESİ - Ölçeksiz

İŞİN ADI	ELEKTRİK İÇ TESİSAT PROJESİ
YAPI SAHİBİ	BROSCO İTHALAT İHRACAT VE TİCARET ANONİM ŞİRKETİ
ADRES	YUKARI MAHALLE / KEMALPAŞA / İZMİR - Ada: ...... Parsel: 2
PAFTA ADI	HESAP TABLOLARI VE NOTLAR
ÖLÇEK / TARİH / PAFTA NO	Ölçeksiz | 19.10.2026 | 01-05
PROJE MÜELLİFİ	Elektrik Mühendisi - Adı Soyadı: ....
ODA SİCİL / SMM NO	EMO Sicil No: .... SMM Belge No: .... İmza: ....