
LEJANT

- LED yüksek tavan (highbay) armatürü 150 W, 21.000 lm, IP65
- LED panel armatür 60x60, 36 W, 3.600 lm, UGR<19
- LED downlight 18 W, 1.800 lm, IP20
- LED downlight 12 W, 1.200 lm, IP44 (islak hacim)
- LED etanj armatür 36 W, 4.000 lm, IP65
- LED acil aydınlatma armatürü 3 W, 3 saat, sürekli/sürekli olmayan
- LED çıkış/yönlendirme armatürü 3 W, 3 saat
- AK: 3 saat acil kitli armatür (sürekli faz ile beslenir)
- Adi anahtar (h=110 cm)
- Komütatör anahtar
- Vavien anahtar
- Tali dağıtım panosu (UTP / İDP)
- Aydınlatma linyesi, ok: panoya dönüş, etiket PANO/LİNYE

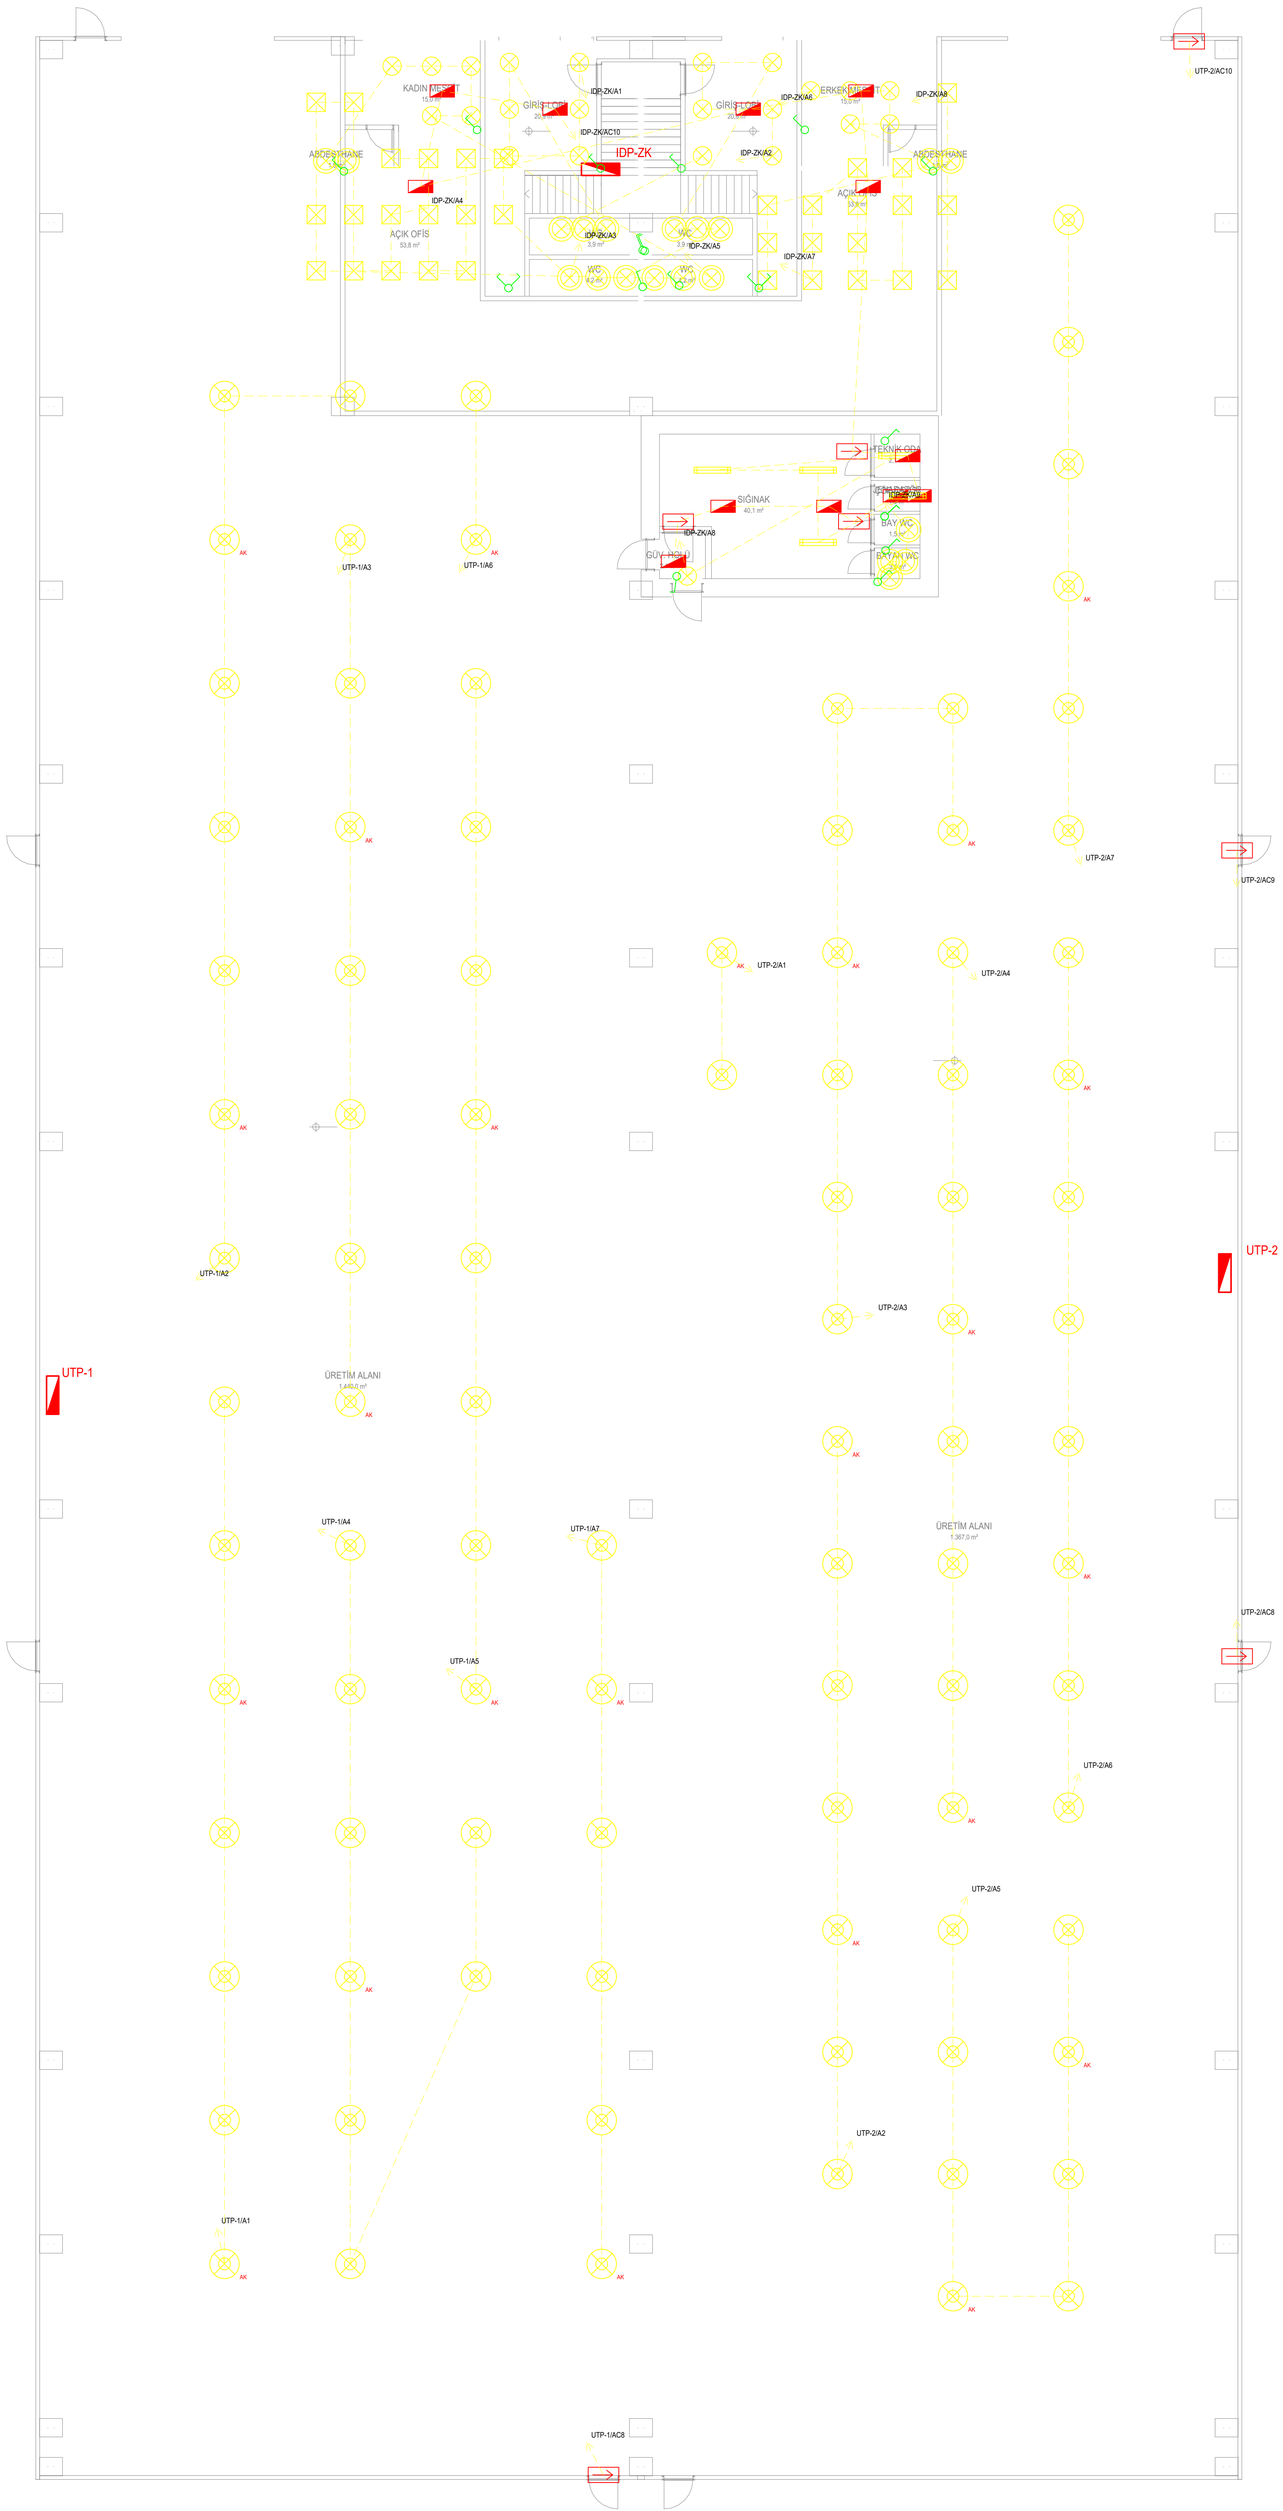


AYDINLATMA TESİSATI PLANI

ZEMİN KAT PLANI - Ö: 1/100

Parsel 3 | BROSCO İTHALAT İHRACAT VE TİCARET ANONİM ŞİRKETİ

CLD - 19.10.2026 - mimari altlık: BROSCO 3 NOLU PARSEL MİMARİ.dwg

İŞİN ADI	ELEKTRİK İÇ TESİSAT PROJESİ
YAPI SAHİBİ	BROSCO İTHALAT İHRACAT VE TİCARET ANONİM ŞİRKETİ
ADRES	ULUCAK / KEMALPAŞA / İZMİR - Ada: ..... Parsel: 3
PAFTA ADI	AYDINLATMA TESİSATI PLANI - ZEMİN KAT PLANI
ÖLÇEK / TARİH / PAFTA NO	1/100 | 19.10.2026 | 01-01
PROJE MÜELLİFİ	Elektrik Mühendisi - Adı Soyadı: .....
ODA SİCİL / SMM NO	EMO Sicil No: ..... SMM Belge No: ..... İmza: .....

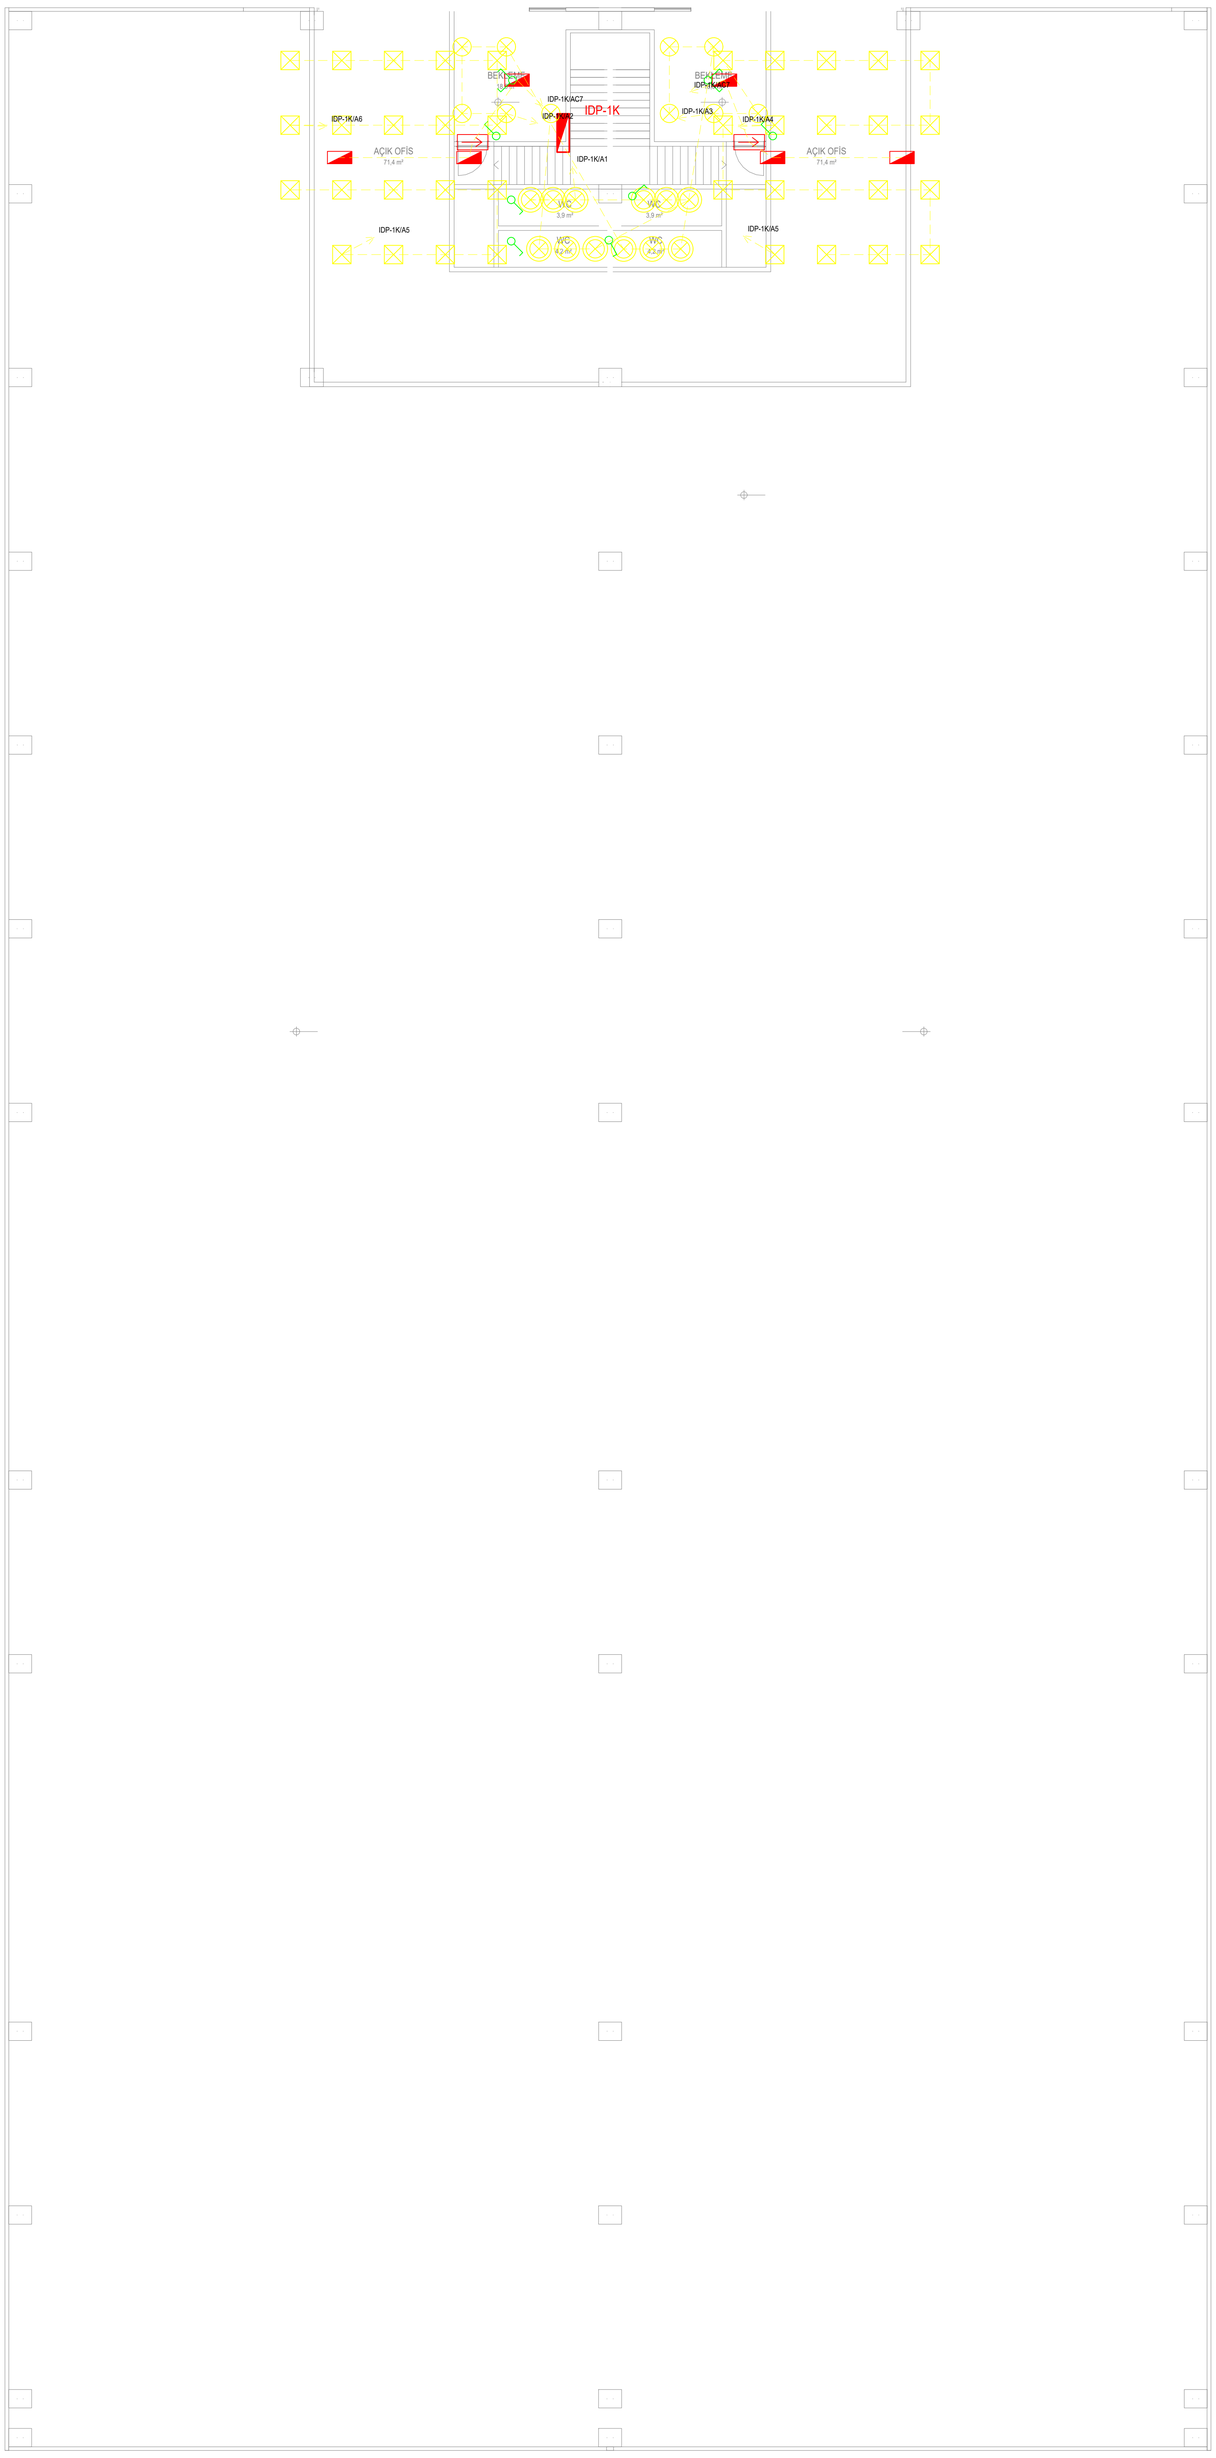

LEJANT

- LED yüksek tavan (highbay) armatürü 150 W, 21.000 lm, IP65
- LED panel armatür 60x60, 36 W, 3.600 lm, UGR<19
- LED downlight 18 W, 1.800 lm, IP20
- LED downlight 12 W, 1.200 lm, IP44 (ıslak hacim)
- LED etanj armatür 36 W, 4.000 lm, IP65
- LED acil aydınlatma armatürü 3 W, 3 saat, sürekli/sürekli olmayan
- LED çıkış/yönlendirme armatürü 3 W, 3 saat
- AK: 3 saat acil kitli armatür (sürekli faz ile beslenir)
- Adi anahtar (h=110 cm)
- Komütatör anahtar
- Vavien anahtar
- Tali dağıtım panosu (UTP / IDP)
- Aydınlatma linyesi, ok: panoya dönüş, etiket PANO/LİNYE

AYDINLATMA TESİSATI PLANI

1. KAT PLANI - Ö: 1/100


Parsel 3 | BROSCO İTHALAT İHRACAT VE TİCARET ANONİM ŞİRKETİ

CLD - 19.10.2026 - mimari altlık: BROSCO 3 NOLU PARSEL MİMARİ.dwg

İŞİN ADI	ELEKTRİK İÇ TESİSAT PROJESİ
YAPI SAHİBİ	BROSCO İTHALAT İHRACAT VE TİCARET ANONİM ŞİRKETİ
ADRES	ULUCAK / KEMALPAŞA / İZMİR - Ada: ..... Parsel: 3
PAFTA ADI	AYDINLATMA TESİSATI PLANI - 1. KAT PLANI
ÖLÇEK / TARİH / PAFTA NO	1/100 | 19.10.2026 | 01-02
PROJE MÜELLİFİ	Elektrik Mühendisi - Adı Soyadı: .....
ODA SİCİL / SMM NO	EMO Sicil No: ..... SMM Belge No: ..... İmza: .....

LEJANT

- Topraklı priz 16 A (h=40 cm, tezgah h=110 cm)
- Bilgisayar prizi (ayrı linye, UPS hazırlığı)
- Etanj priz IP44
- Endüstriyel priz grubu CEE 32A+16A+2x16A (iç koruma, h=150 cm)
- IS — Ani su ısıtıcı çıkışı (IS) - ayrı linye
- TS — Elektrikli termosifon çıkışı (TS) - ayrı linye
- B — Bulaşık makinesi çıkışı (B) - ayrı linye
- A — Havalandırma cihazı / aspiratör çıkışı (A) - ayrı linye
- Tali dağıtım panosu (UTP / İDP)
- Priz / kuvvet linyesi, ok: panoya dönüş

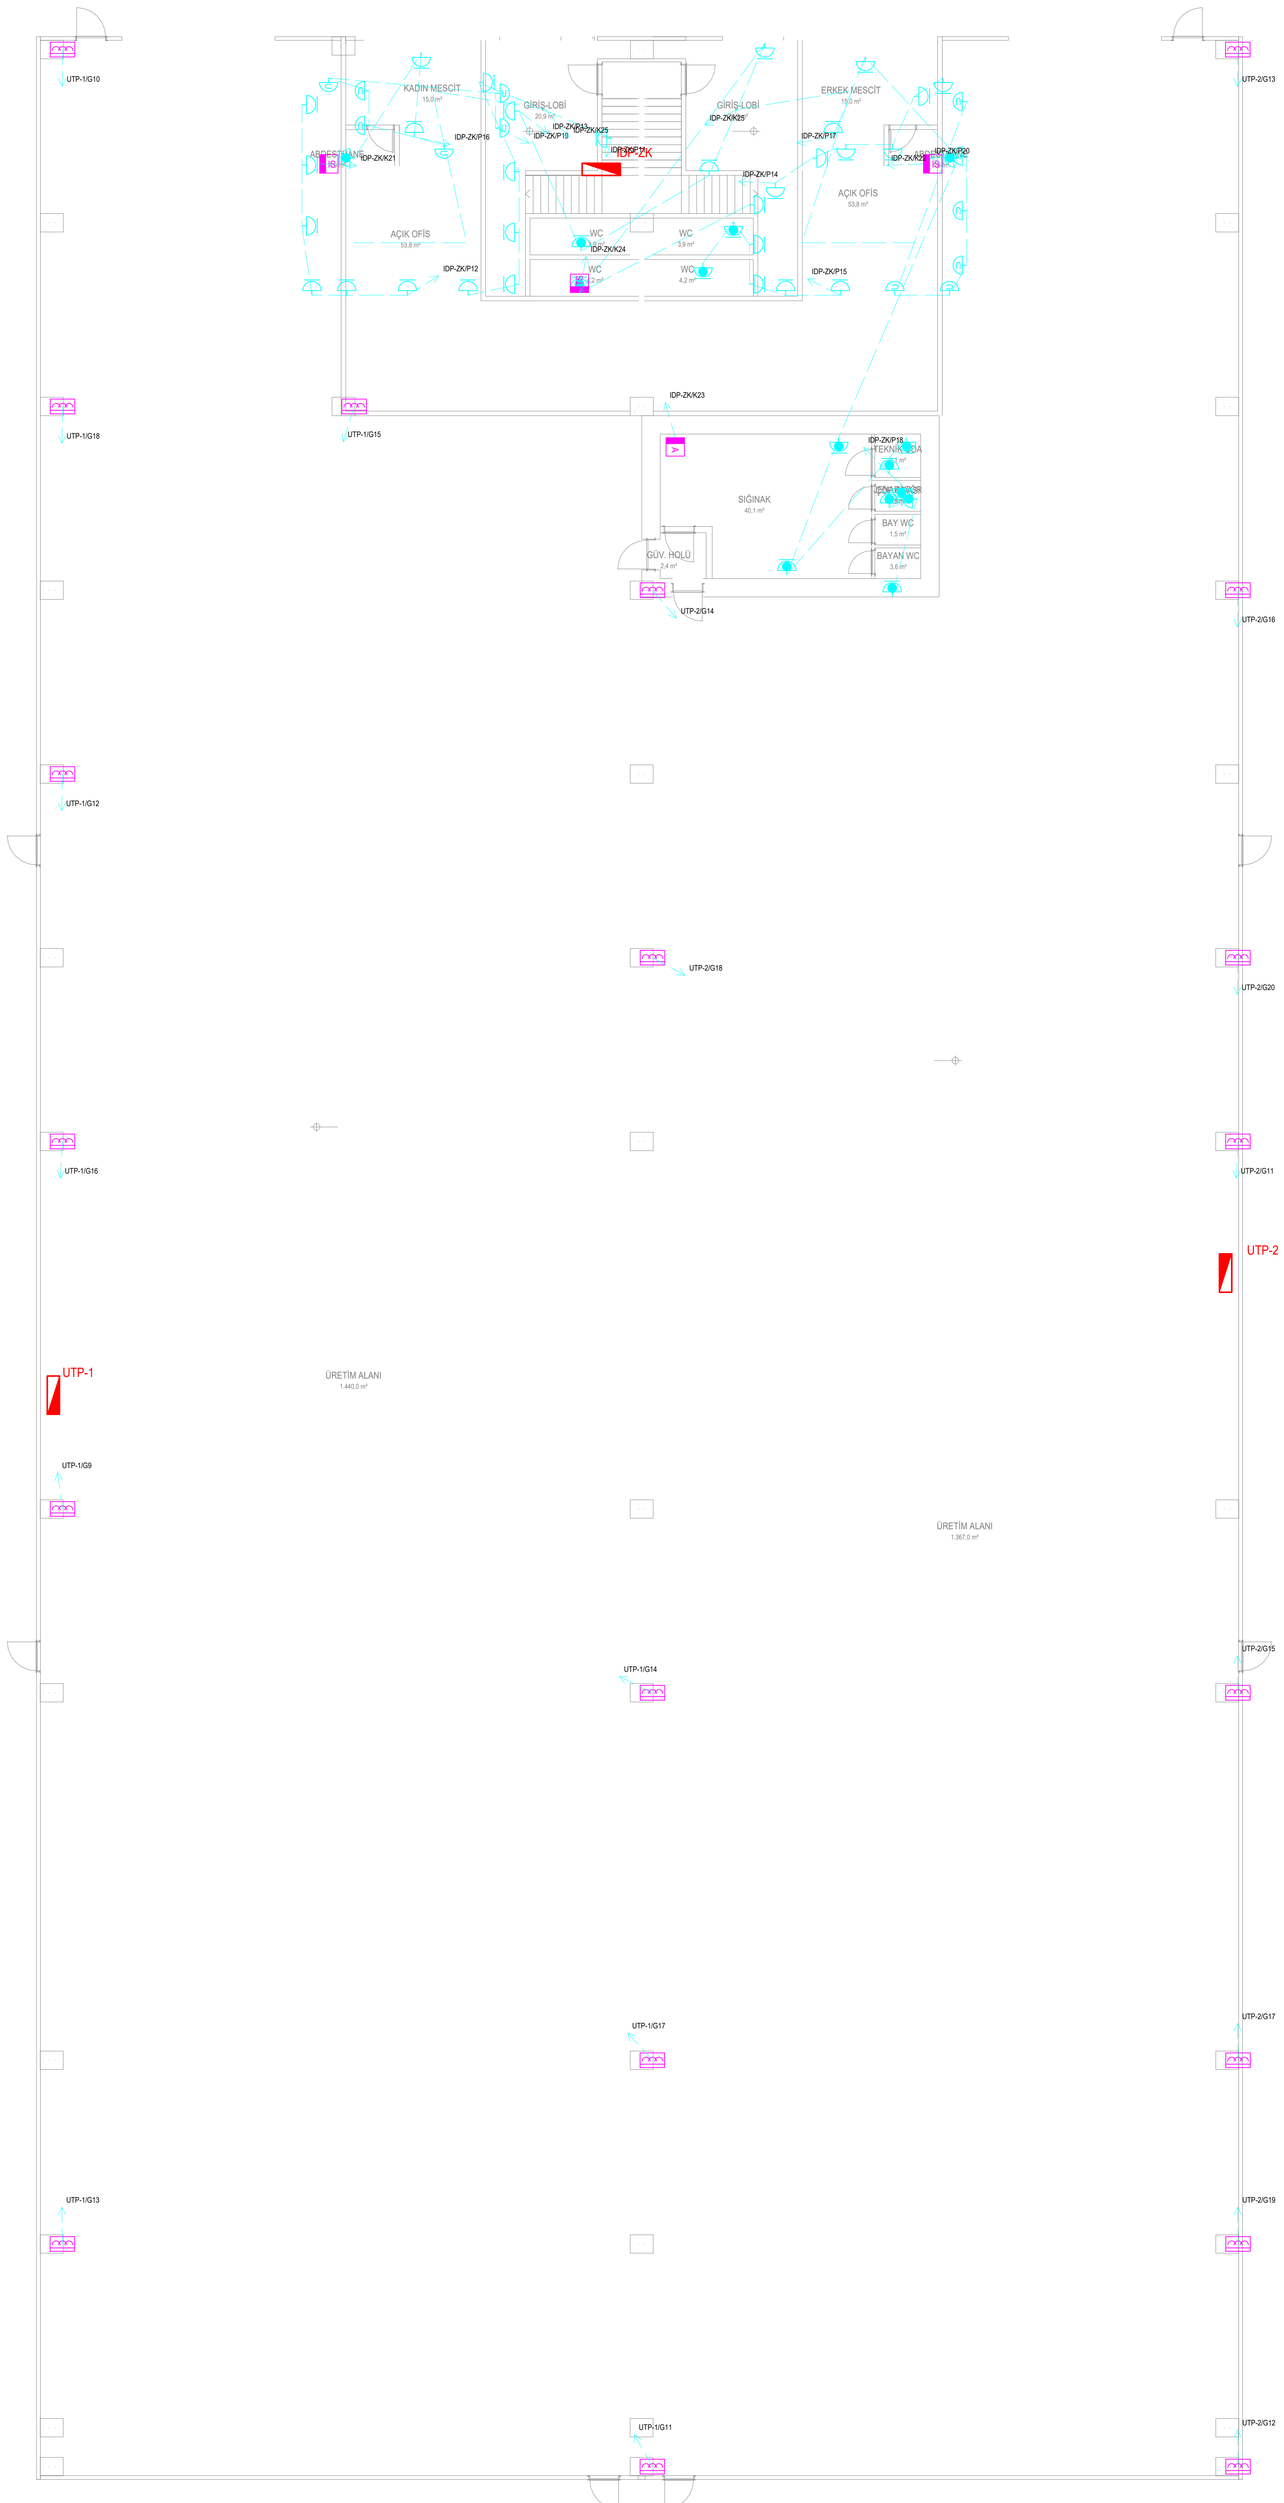


PRİZ VE KUVVET TESİSATI PLANI

ZEMİN KAT PLANI - Ö: 1/100

Parsel 3 | BROSCO İTHALAT İHRACAT VE TİCARET ANONİM ŞİRKETİ

CLD - 19.10.2026 - mimari altık: BROSCO 3 NOLU PARSEL MİMARİ.dwg

İŞİN ADI	ELEKTRİK İÇ TESİSAT PROJESİ
YAPI SAHİBİ	BROSCO İTHALAT İHRACAT VE TİCARET ANONİM ŞİRKETİ
ADRES	ULUCAK / KEMALPAŞA / İZMİR - Ada: ..... Parsel: 3
PAFTA ADI	PRİZ VE KUVVET TESİSATI PLANI - ZEMİN KAT PLANI
ÖLÇEK / TARİH / PAFTA NO	1/100 | 19.10.2026 | 01-03
PROJE MÜELLİFİ	Elektrik Mühendisi - Adı Soyadı: .....
ODA SİCİL / SMM NO	EMO Sicil No: ..... SMM Belge No: ..... İmza: .....

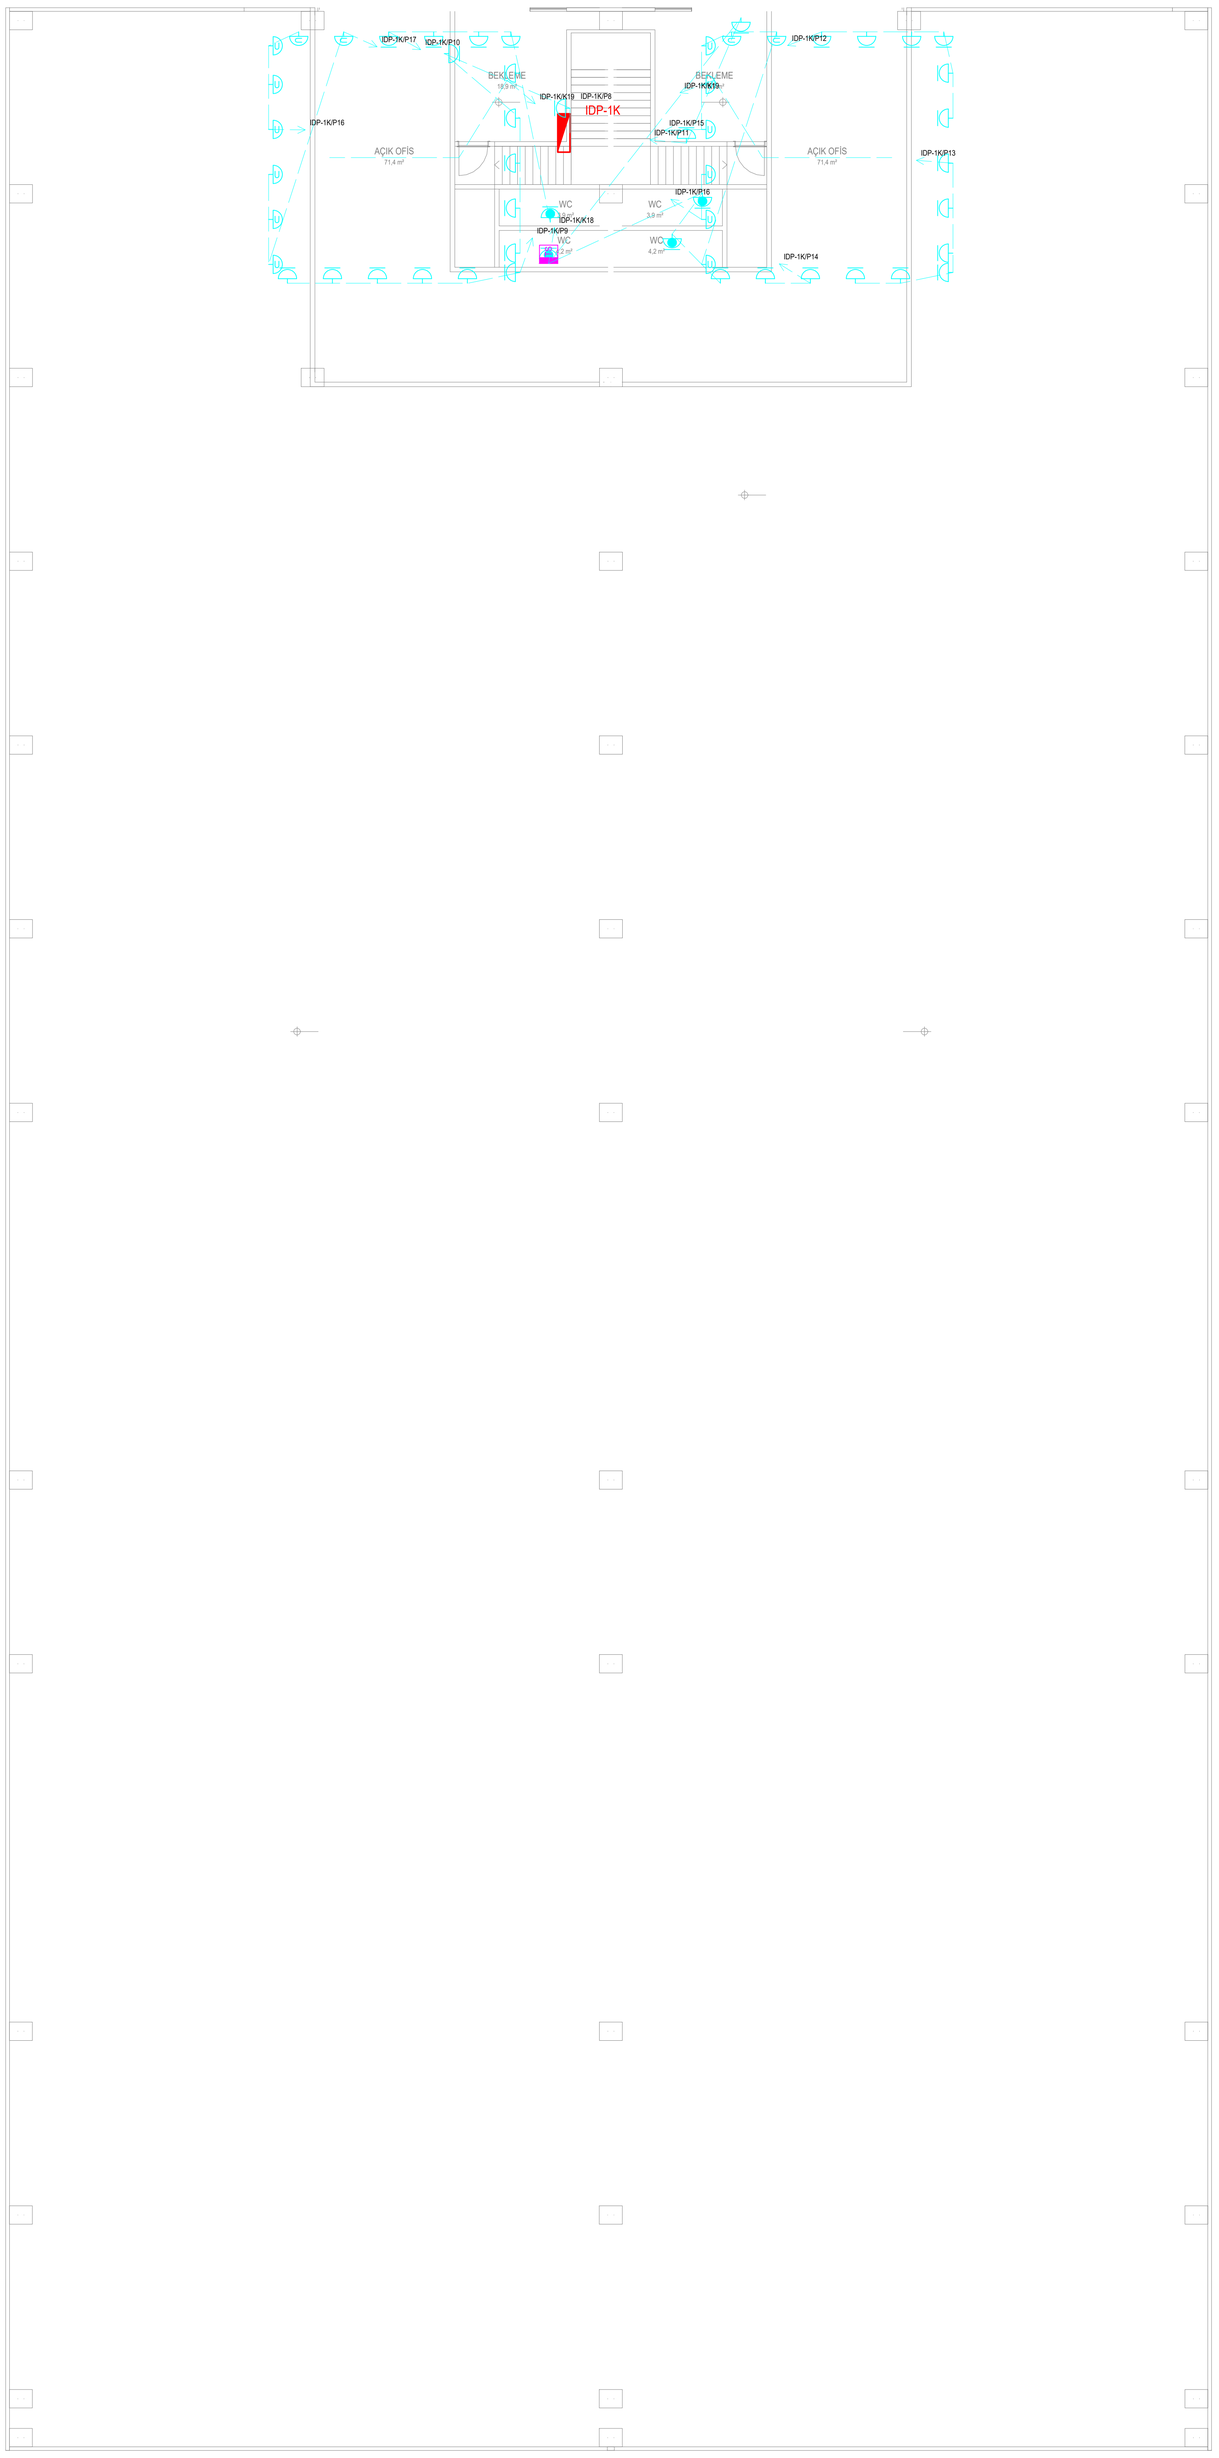

LEJANT

- Topraklı priz 16 A (h=40 cm, tezgah h=110 cm)
- Bilgisayar prizi (ayrı linye, UPS hazırlığı)
- Etanj priz IP44
- Endüstriyel priz grubu CEE 32A+16A+2x16A (iç koruma, h=150 cm)
- IS — Ani su ısıtıcı çıkışı (IS) - ayrı linye
- TS — Elektrikli termosifon çıkışı (TS) - ayrı linye
- B — Bulaşık makinesi çıkışı (B) - ayrı linye
- A — Havalandırma cihazı / aspiratör çıkışı (A) - ayrı linye
- Tali dağıtım panosu (UTP / İDP)
- Priz / kuvvet linyesi, ok: panoya dönüş

PRİZ VE KUVVET TESİSATI PLANI

1. KAT PLANI - Ö: 1/100

Parsel 3 | BROSCO İTHALAT İHRACAT VE TİCARET ANONİM ŞİRKETİ

CLD - 19.10.2026 - mimari altlık: BROSCO 3 NOLU PARSEL MİMARİ.dwg

İŞİN ADI	ELEKTRİK İÇ TESİSAT PROJESİ
YAPI SAHİBİ	BROSCO İTHALAT İHRACAT VE TİCARET ANONİM ŞİRKETİ
ADRES	ULUCAK / KEMALPAŞA / İZMİR - Ada: ..... Parsel: 3
PAFTA ADI	PRİZ VE KUVVET TESİSATI PLANI - 1. KAT PLANI
ÖLÇEK / TARİH / PAFTA NO	1/100 | 19.10.2026 | 01-04
PROJE MÜELLİFİ	Elektrik Mühendisi - Adı Soyadı: .....
ODA SİCİL / SMM NO	EMO Sicil No: ..... SMM Belge No: ..... İmza: .....

LEJANT

- LED yüksek tavan (highbay) armatürü 150 W, 21.000 lm, IP65
- LED panel armatür 60x60, 36 W, 3.600 lm, UGR<19
- LED downlight 18 W, 1.800 lm, IP20
- LED downlight 12 W, 1.200 lm, IP44 (ıslak hacim)
- LED etanj armatür 36 W, 4.000 lm, IP65
- LED acil aydınlatma armatürü 3 W, 3 saat, sürekli/sürekli olmayan
- LED çıkış/yönlendirme armatürü 3 W, 3 saat
- AK: 3 saat acil kitli armatür (sürekli faz ile beslenir)
- Adi anahtar (h=110 cm)
- Komütatör anahtar
- Vavien anahtar
- Tali dağıtım panosu (UTP / İDP)
- Aydınlatma linyesi, ok: panoya dönüş, etiket PANO/LİNYE
- Topraklı priz 16 A (h=40 cm, tezgah h=110 cm)
- Bilgisayar prizi (ayrı linye, UPS hazırlığı)
- Etanj priz IP44
- Endüstriyel priz grubu CEE 32A+16A+2x16A (iç koruma, h=150 cm)
- IS — Ani su ısıtıcı çıkışı (IS) - ayrı linye
- TS — Elektrikli termosifon çıkışı (TS) - ayrı linye
- B — Bulaşık makinesi çıkışı (B) - ayrı linye
- A — Havalandırma cihazı / aspiratör çıkışı (A) - ayrı linye
- Priz / kuvvet linyesi, ok: panoya dönüş

LİNYE LİSTESİ (1)

PANO	LİNYE	TÜR	AÇIKLAMA	ADET	GÜÇ (W)	FAZ	SİGORTA	KAÇAK AKIM	KABLO	L (m)	%e
IDP-ZK	A1	Aydınlatma	Aydınlatma	10	162	S	B10A	30 mA	NYM 3x1,5 mm²	31,8	0,23
IDP-ZK	A2	Aydınlatma	Aydınlatma	10	150	R	B10A	30 mA	NYM 3x1,5 mm²	32,3	0,22
IDP-ZK	A3	Aydınlatma	Aydınlatma	10	336	R	B10A	30 mA	NYM 3x1,5 mm²	25,2	0,38
IDP-ZK	A4	Aydınlatma	Aydınlatma	10	312	R	B10A	30 mA	NYM 3x1,5 mm²	42,3	0,59
IDP-ZK	A5	Aydınlatma	Aydınlatma	8	126	T	B10A	30 mA	NYM 3x1,5 mm²	32,3	0,18
IDP-ZK	A6	Aydınlatma	Aydınlatma	10	222	T	B10A	30 mA	NYM 3x1,5 mm²	31,2	0,31
IDP-ZK	A7	Aydınlatma	Aydınlatma	10	360	S	B10A	30 mA	NYM 3x1,5 mm²	27,0	0,44
IDP-ZK	A8	Aydınlatma	Aydınlatma	10	342	T	B10A	30 mA	NYM 3x1,5 mm²	64,7	1,00
IDP-ZK	A9	Aydınlatma	Aydınlatma	4	48	S	B10A	30 mA	NYM 3x1,5 mm²	23,0	0,05
IDP-ZK	AC10	Acil ayd.	Acil aydınlatma / yönlendirme	15	45	R	B10A	30 mA	NYM 3x1,5 mm²	59,2	0,12
IDP-ZK	P11	Priz	Priz	6	1.800	T	B16A	30 mA	NYM 3x2,5 mm²	19,7	0,96
IDP-ZK	P12	Priz	Priz	6	1.800	R	B16A	30 mA	NYM 3x2,5 mm²	22,3	1,09
IDP-ZK	P13	Priz	Priz	6	1.800	S	B16A	30 mA	NYM 3x4 mm²	42,5	1,29
IDP-ZK	P14	Priz	Priz	6	1.800	T	B16A	30 mA	NYM 3x2,5 mm²	17,6	0,86
IDP-ZK	P15	Priz	Priz	6	1.800	R	B16A	30 mA	NYM 3x2,5 mm²	21,0	1,02
IDP-ZK	P16	Priz	Priz	3	900	T	B16A	30 mA	NYM 3x2,5 mm²	18,0	0,44
IDP-ZK	P17	Priz	Priz	6	1.800	S	B16A	30 mA	NYM 3x4 mm²	44,0	1,34
IDP-ZK	P18	Priz	Priz	5	1.500	S	B16A	30 mA	NYM 3x2,5 mm²	25,0	1,01
IDP-ZK	P19	Priz	Bilgisayar prizi (UPS hazırlığı)	6	1.800	T	B16A	30 mA A tipi	NYM 3x2,5 mm²	20,8	1,01
IDP-ZK	P20	Priz	Bilgisayar prizi (UPS hazırlığı)	6	1.800	R	B16A	30 mA A tipi	NYM 3x4 mm²	31,9	0,97
IDP-ZK	K21	Kuvvet	Ani su ısıtıcı 3,5 kW	1	3.500	R	B25A	30 mA	NYM 3x4 mm²	13,6	0,80
IDP-ZK	K22	Kuvvet	Ani su ısıtıcı 3,5 kW	1	3.500	S	B25A	30 mA	NYM 3x4 mm²	15,1	0,89
IDP-ZK	K23	Kuvvet	Sığınak havalandırma cihazı	1	750	T	B10A	30 mA	NYM 3x1,5 mm²	13,2	0,45
IDP-ZK	K24	Kuvvet	Elektrikli termosifon 80 L 2 kW	1	2.000	T	B16A	30 mA	NYM 3x2,5 mm²	7,5	0,40
IDP-ZK	K25	Kuvvet	VRF iç üniteleri besleme	8	580	S	B10A	30 mA A tipi	NYM 3x1,5 mm²	50,4	1,31
UTP-2	A1	Aydınlatma	Aydınlatma (yüksek tavan, AK: sürekli faz)	2	300	T	B10A	30 mA	NYM 4x1,5 mm²	33,2	0,45
UTP-2	A2	Aydınlatma	Aydınlatma (yüksek tavan, AK: sürekli faz)	7	1.050	S	B16A	30 mA	NYM 4x4 mm²	70,4	1,25
UTP-2	A3	Aydınlatma	Aydınlatma (yüksek tavan, AK: sürekli faz)	8	1.200	R	B16A	30 mA	NYM 4x4 mm²	52,7	1,07
UTP-2	A4	Aydınlatma	Aydınlatma (yüksek tavan, AK: sürekli faz)	8	1.200	S	B16A	30 mA	NYM 4x4 mm²	54,0	1,09
UTP-2	A5	Aydınlatma	Aydınlatma (yüksek tavan, AK: sürekli faz)	8	1.200	T	B16A	30 mA	NYM 4x4 mm²	64,6	1,31
UTP-2	A6	Aydınlatma	Aydınlatma (yüksek tavan, AK: sürekli faz)	8	1.200	R	B16A	30 mA	NYM 4x4 mm²	59,1	1,20
UTP-2	A7	Aydınlatma	Aydınlatma (yüksek tavan, AK: sürekli faz)	6	900	T	B10A	30 mA	NYM 4x2,5 mm²	46,6	1,13
UTP-2	AC8	Acil ayd.	Acil aydınlatma / yönlendirme	1	3	S	B10A	30 mA	NYM 3x1,5 mm²	17,4	0,00
UTP-2	AC9	Acil ayd.	Acil aydınlatma / yönlendirme	1	3	S	B10A	30 mA	NYM 3x1,5 mm²	18,9	0,00
UTP-2	AC10	Acil ayd.	Acil aydınlatma / yönlendirme	1	3	S	B10A	30 mA	NYM 3x1,5 mm²	49,3	0,01
UTP-2	G11	End. priz	End. priz grubu (4P C32+C16+2xB16)	1	5.000	RST	C32A	30 mA A tipi (kutu içi)	NYM 5x10 mm²	7,9	0,10
UTP-2	G12	End. priz	End. priz grubu (4P C32+C16+2xB16)	1	5.000	RST	C32A	30 mA A tipi (kutu içi)	NYM 5x10 mm²	47,8	0,59
UTP-2	G13	End. priz	End. priz grubu (4P C32+C16+2xB16)	1	5.000	RST	C32A	30 mA A tipi (kutu içi)	NYM 5x10 mm²	48,9	0,60
UTP-2	G14	End. priz	End. priz grubu (4P C32+C16+2xB16)	1	5.000	RST	C32A	30 mA A tipi (kutu içi)	NYM 5x10 mm²	36,6	0,45
UTP-2	G15	End. priz	End. priz grubu (4P C32+C16+2xB16)	1	5.000	RST	C32A	30 mA A tipi (kutu içi)	NYM 5x10 mm²	18,8	0,23
UTP-2	G16	End. priz	End. priz grubu (4P C32+C16+2xB16)	1	5.000	RST	C32A	30 mA A tipi (kutu içi)	NYM 5x10 mm²	28,6	0,35
UTP-2	G17	End. priz	End. priz grubu (4P C32+C16+2xB16)	1	5.000	RST	C32A	30 mA A tipi (kutu içi)	NYM 5x10 mm²	32,6	0,40
UTP-2	G18	End. priz	End. priz grubu (4P C32+C16+2xB16)	1	5.000	RST	C32A	30 mA A tipi (kutu içi)	NYM 5x10 mm²	27,8	0,34
UTP-2	G19	End. priz	End. priz grubu (4P C32+C16+2xB16)	1	5.000	RST	C32A	30 mA A tipi (kutu içi)	NYM 5x10 mm²	39,5	0,48
UTP-2	G20	End. priz	End. priz grubu (4P C32+C16+2xB16)	1	5.000	RST	C32A	30 mA A tipi (kutu içi)	NYM 5x10 mm²	14,8	0,18

LİNYE LİSTESİ (2)

PANO	LİNYE	TÜR	AÇIKLAMA	ADET	GÜÇ (W)	FAZ	SİGORTA	KAÇAK AKIM	KABLO	L (m)	%e
UTP-2	K21	Kuvvet	Aydınlatma kumanda (kontaktör/saat rölesi)	1	50	S	B10A	30 mA	NYM 3x1,5 mm²	3,0	0,01
UTP-2	K22	Kuvvet	Seksiyonel kapı motoru (L≈25 m kabul)	1	750	RST	C10A	300 mA	NYM 5x1,5 mm²	25,0	0,14
UTP-1	A1	Aydınlatma	Aydınlatma (yüksek tavan, AK: sürekli faz)	7	1.050	R	B16A	30 mA	NYM 4x4 mm²	71,7	1,27
UTP-1	A2	Aydınlatma	Aydınlatma (yüksek tavan, AK: sürekli faz)	8	1.200	R	B16A	30 mA	NYM 4x4 mm²	51,5	1,04
UTP-1	A3	Aydınlatma	Aydınlatma (yüksek tavan, AK: sürekli faz)	7	1.050	S	B16A	30 mA	NYM 4x4 mm²	72,5	1,28
UTP-1	A4	Aydınlatma	Aydınlatma (yüksek tavan, AK: sürekli faz)	8	1.200	S	B16A	30 mA	NYM 4x4 mm²	62,9	1,27
UTP-1	A5	Aydınlatma	Aydınlatma (yüksek tavan, AK: sürekli faz)	8	1.200	T	B16A	30 mA	NYM 4x4 mm²	63,3	1,28
UTP-1	A6	Aydınlatma	Aydınlatma (yüksek tavan, AK: sürekli faz)	2	300	T	B10A	30 mA	NYM 4x1,5 mm²	47,3	0,64
UTP-1	A7	Aydınlatma	Aydınlatma (yüksek tavan, AK: sürekli faz)	6	900	T	B10A	30 mA	NYM 4x2,5 mm²	54,6	1,33
UTP-1	AC8	Acil ayd.	Acil aydınlatma / yönlendirme	1	3	S	B10A	30 mA	NYM 3x1,5 mm²	48,6	0,01
UTP-1	G9	End. priz	End. priz grubu (4P C32+C16+2xB16)	1	5.000	RST	C32A	30 mA A tipi (kutu içi)	NYM 5x10 mm²	7,3	0,09
UTP-1	G10	End. priz	End. priz grubu (4P C32+C16+2xB16)	1	5.000	RST	C32A	30 mA A tipi (kutu içi)	NYM 5x10 mm²	53,5	0,66
UTP-1	G11	End. priz	End. priz grubu (4P C32+C16+2xB16)	1	5.000	RST	C32A	30 mA A tipi (kutu içi)	NYM 5x10 mm²	49,2	0,60
UTP-1	G12	End. priz	End. priz grubu (4P C32+C16+2xB16)	1	5.000	RST	C32A	30 mA A tipi (kutu içi)	NYM 5x10 mm²	26,3	0,32
UTP-1	G13	End. priz	End. priz grubu (4P C32+C16+2xB16)	1	5.000	RST	C32A	30 mA A tipi (kutu içi)	NYM 5x10 mm²	34,9	0,43
UTP-1	G14	End. priz	End. priz grubu (4P C32+C16+2xB16)	1	5.000	RST	C32A	30 mA A tipi (kutu içi)	NYM 5x10 mm²	28,3	0,35
UTP-1	G15	End. priz	End. priz grubu (4P C32+C16+2xB16)	1	5.000	RST	C32A	30 mA A tipi (kutu içi)	NYM 5x10 mm²	41,9	0,51
UTP-1	G16	End. priz	End. priz grubu (4P C32+C16+2xB16)	1	5.000	RST	C32A	30 mA A tipi (kutu içi)	NYM 5x10 mm²	12,5	0,15
UTP-1	G17	End. priz	End. priz grubu (4P C32+C16+2xB16)	1	5.000	RST	C32A	30 mA A tipi (kutu içi)	NYM 5x10 mm²	36,8	0,45
UTP-1	G18	End. priz	End. priz grubu (4P C32+C16+2xB16)	1	5.000	RST	C32A	30 mA A tipi (kutu içi)	NYM 5x10 mm²	40,1	0,49
UTP-1	K19	Kuvvet	Aydınlatma kumanda (kontaktör/saat rölesi)	1	50	R	B10A	30 mA	NYM 3x1,5 mm²	3,0	0,01
UTP-1	K20	Kuvvet	Seksiyonel kapı motoru (L≈25 m kabul)	1	750	RST	C10A	300 mA	NYM 5x1,5 mm²	25,0	0,14
IDP-1K	A1	Aydınlatma	Aydınlatma	10	126	T	B10A	30 mA	NYM 3x1,5 mm²	24,4	0,14
IDP-1K	A2	Aydınlatma	Aydınlatma	10	162	S	B10A	30 mA	NYM 3x1,5 mm²	34,1	0,25
IDP-1K	A3	Aydınlatma	Aydınlatma	10	324	R	B10A	30 mA	NYM 3x1,5 mm²	26,6	0,39
IDP-1K	A4	Aydınlatma	Aydınlatma	10	360	T	B10A	30 mA	NYM 3x1,5 mm²	29,2	0,47
IDP-1K	A5	Aydınlatma	Aydınlatma	10	360	R	B10A	30 mA	NYM 3x1,5 mm²	44,3	0,72
IDP-1K	A6	Aydınlatma	Aydınlatma	10	360	T	B10A	30 mA	NYM 3x1,5 mm²	31,5	0,51
IDP-1K	AC7	Acil ayd.	Acil aydınlatma / yönlendirme	8	24	R	B10A	30 mA	NYM 3x1,5 mm²	37,3	0,04
IDP-1K	P8	Priz	Priz	6	1.800	S	B16A	30 mA	NYM 3x2,5 mm²	17,9	0,87
IDP-1K	P9	Priz	Priz	6	1.800	T	B16A	30 mA	NYM 3x2,5 mm²	17,3	0,84
IDP-1K	P10	Priz	Priz	6	1.800	S	B16A	30 mA	NYM 3x2,5 mm²	22,7	1,10
IDP-1K	P11	Priz	Priz	6	1.800	T	B16A	30 mA	NYM 3x4 mm²	35,1	1,07
IDP-1K	P12	Priz	Priz	6	1.800	R	B16A	30 mA	NYM 3x2,5 mm²	21,0	1,02
IDP-1K	P13	Priz	Priz	6	1.800	S	B16A	30 mA	NYM 3x2,5 mm²	25,2	1,23
IDP-1K	P14	Priz	Priz	2	600	T	B16A	30 mA	NYM 3x2,5 mm²	15,3	0,25
IDP-1K	P15	Priz	Bilgisayar prizi (UPS hazırlığı)	6	1.800	T	B16A	30 mA A tipi	NYM 3x2,5 mm²	23,2	1,13
IDP-1K	P16	Priz	Bilgisayar prizi (UPS hazırlığı)	6	1.800	R	B16A	30 mA A tipi	NYM 3x4 mm²	31,3	0,95
IDP-1K	P17	Priz	Bilgisayar prizi (UPS hazırlığı)	4	1.200	S	B16A	30 mA A tipi	NYM 3x2,5 mm²	24,9	0,81
IDP-1K	K18	Kuvvet	Elektrikli termosifon 80 L 2 kW	1	2.000	R	B16A	30 mA	NYM 3x2,5 mm²	8,0	0,43
IDP-1K	K19	Kuvvet	VRF iç üniteleri besleme	6	460	R	B10A	30 mA A tipi	NYM 3x1,5 mm²	37,4	0,77

NOTLAR

1- Tesisat Elektrik İç Tesisleri Yönetmeliği, TS HD 60364 ve TS EN 12464-1 esas alınarak hesaplanmıştır.
2- Aydınlatma ve priz tesisatı ayrı paftalarda gösterilmiştir; linye etiketi "PANO/LİNYE", ok yönü panoyu gösterir.
3- Kesitler IEC 60364-5-52 C yöntemi x 0,80 (ofis) / x 0,71 (üretim holü tavası, 40 °C) ile seçilmiştir; gerilim düşümü aydınlatma ve prizde ≤ %1,5, kuvvette ≤ %3 olacak şekilde linyeler bölünmüştür.
4- Kaçak akım: tüm tek fazlı son devreler (priz, aydınlatma, ıslak hacim, özel çıkış) 30 mA, bilgisayar/VRF A tipi; 3 fazlı motor devreleri 300 mA; pano girişleri 300 mA S (seçici) - TS HD 60364-4-41 411.3.3, EMO.
5- Ofis ve ıslak hacimlerde sıva altı spiral boru, üretim alanında galvaniz kablo tavası / boru kullanılacaktır.
6- "AK" acil kitli armatürler kontaktör öncesinden sürekli faz ile beslenir (NYM 4x..: L anahtarlı + L sürekli, TS EN 50172).
7- Acil ve yönlendirme armatürleri 3 saat bataryalıdır (Binaların Yangından Korunması Hakkında Yönetmelik, TS EN 1838).
8- Endüstriyel priz grubu kutusu içinde 4P C32, C16 ve 2xB16 sigortalar ile 30 mA (A tipi) kaçak akım rölesi bulunur.
9- Anahtarlar sahada kapı açılış yönüne göre kapı kanadının arkasında kalmayacak şekilde yerleştirilecektir.
10- Üretim alanı aydınlatması tali panodan kontaktör + saat rölesi ile kumanda edilir.

HESAP TABLOLARI, CETVELLER VE NOTLAR

ELEKTRİK İÇ TESİSAT PROJESİ - Ölçeksiz

İŞİN ADI	ELEKTRİK İÇ TESİSAT PROJESİ
YAPI SAHİBİ	BROSCO İTHALAT İHRACAT VE TİCARET ANONİM ŞİRKETİ
ADRES	ULUCAK / KEMALPAŞA / İZMİR - Ada: ..... Parsel: 3
PAFTA ADI	HESAP TABLOLARI VE NOTLAR
ÖLÇEK / TARİH / PAFTA NO	Ölçeksiz | 19.10.2026 | 01-05
PROJE MÜELLİFİ	Elektrik Mühendisi - Adı Soyadı: .....
ODA SİCİL / SMM NO	EMO Sicil No: ..... SMM Belge No: ..... İmza: .....