
LEJANT

- LED yüksek tavan (highbay) armatürü 150 W, 21.000 lm, IP65
- LED panel armatür 60x60, 36 W, 3.600 lm, UGR<19
- LED downlight 18 W, 1.800 lm, IP20
- LED downlight 12 W, 1.200 lm, IP44 (ıslak hacim)
- LED etanj armatür 36 W, 4.000 lm, IP65
- LED acil aydınlatma armatürü 3 W, 3 saat, sürekli/sürekli olmayan
- LED çıkış/yönlendirme armatürü 3 W, 3 saat
- AK: 3 saat acil kitli armatür (sürekli faz ile beslenir)
- Adi anahtar (h=110 cm)
- Komütatör anahtar
- Vavien anahtar
- Tali dağıtım panosu (UTP / İDP)
- Aydınlatma linyesi, ok: panoya dönüş, etiket PANO/LİNYE

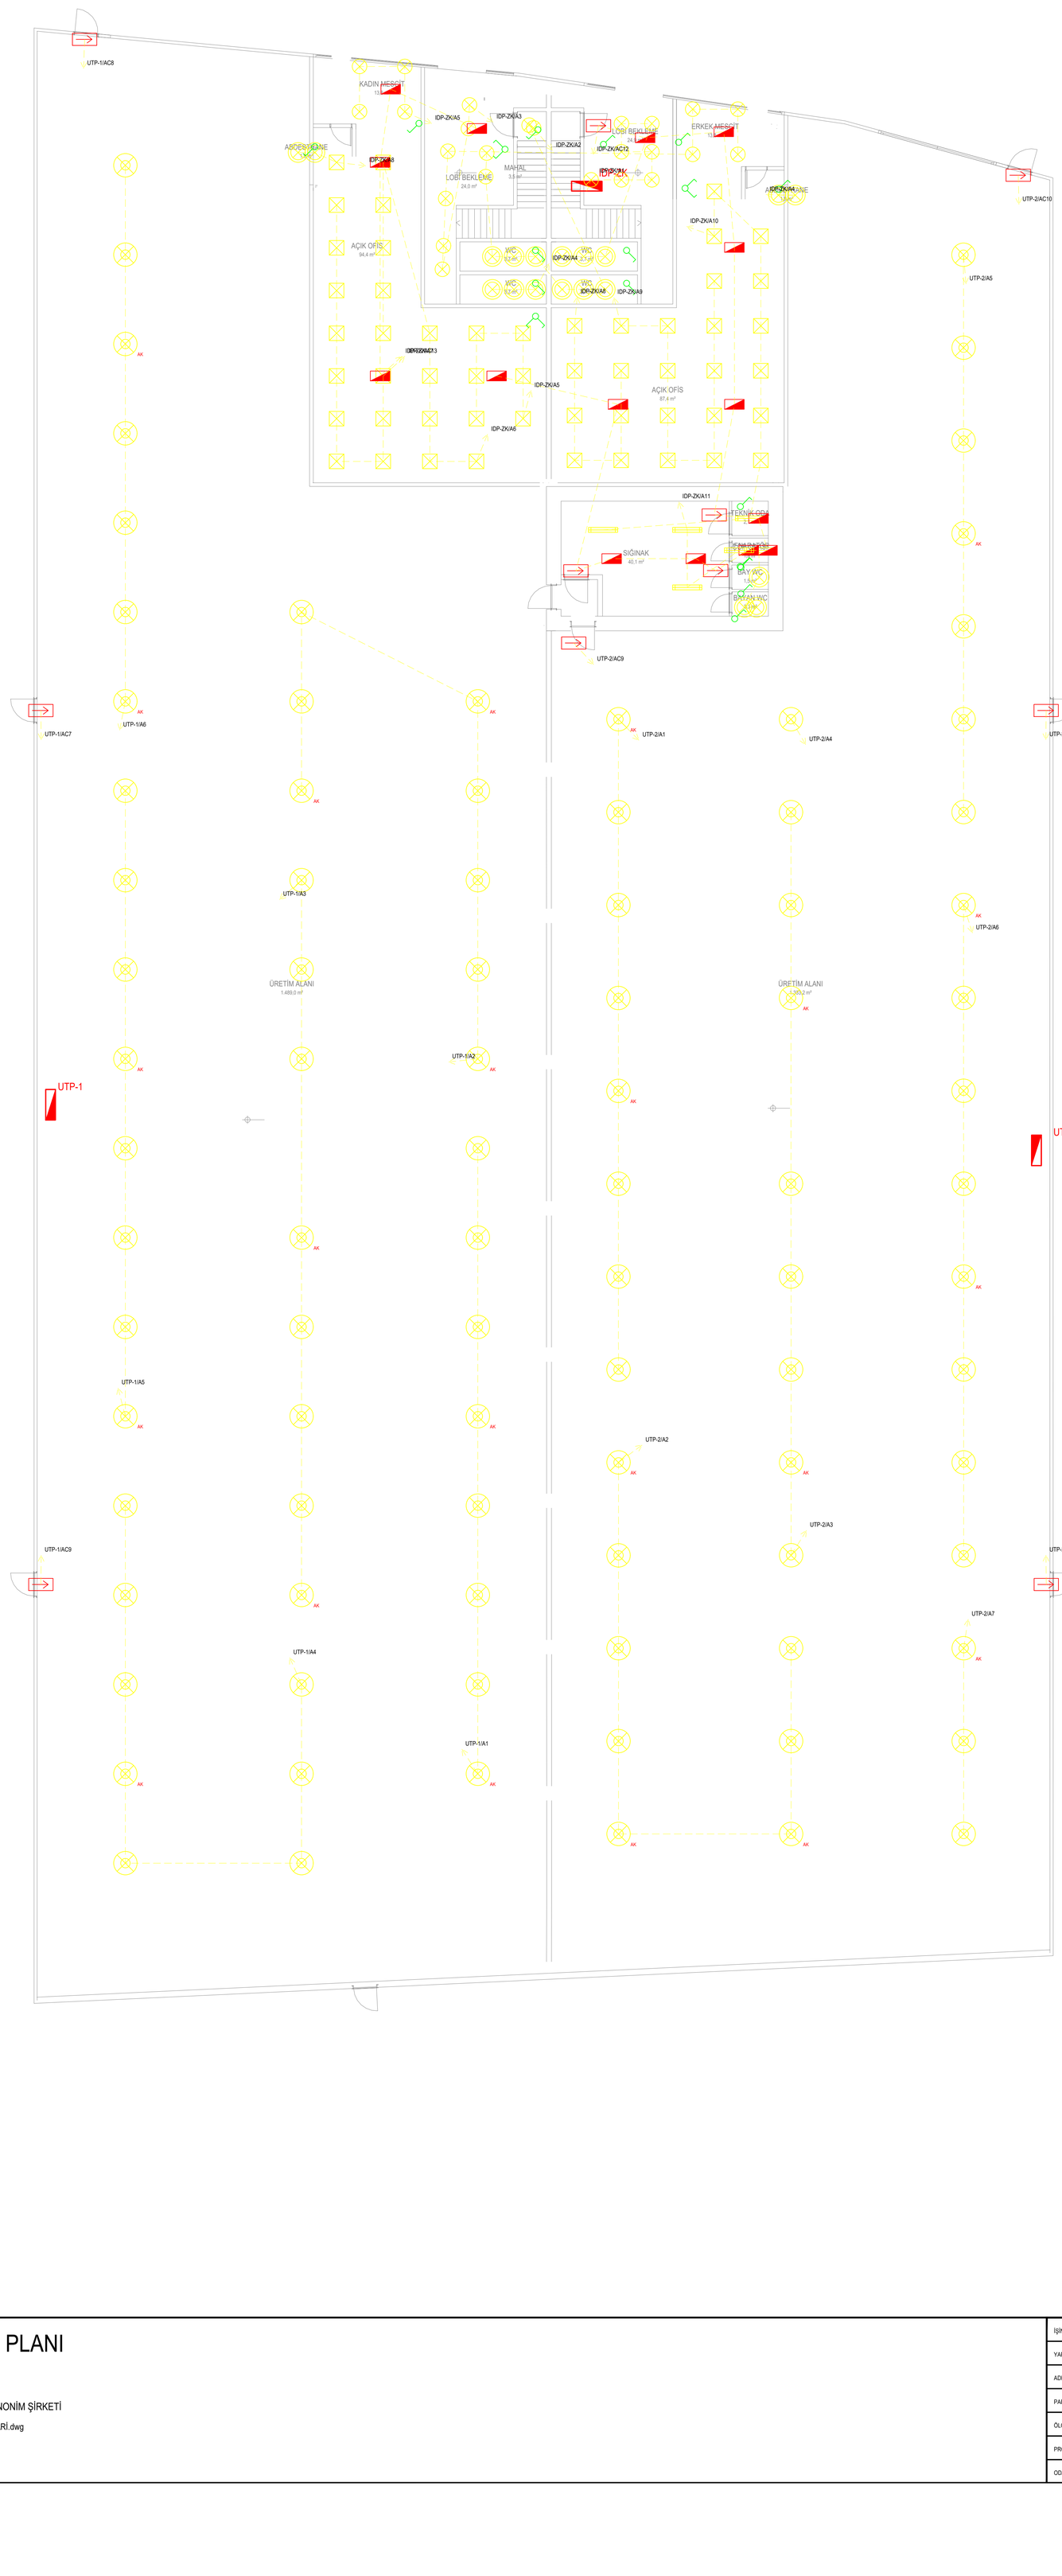


AYDINLATMA TESİSATI PLANI

ZEMİN KAT PLANI - Ö: 1/100

Parsel 4 | BROSCO İTHALAT İHRACAT VE TİCARET ANONİM ŞİRKETİ

CLD - 19.10.2026 - mimari altlık: BROSCO 4 NOLU PARSEL MİMARİ.dwg

İŞİN ADI	ELEKTRİK İÇ TESİSAT PROJESİ
YAPI SAHİBİ	BROSCO İTHALAT İHRACAT VE TİCARET ANONİM ŞİRKETİ
ADRES	ULUCAK / KEMALPAŞA / İZMİR - Ada: ..... Parsel: 4
PAFTA ADI	AYDINLATMA TESİSATI PLANI - ZEMİN KAT PLANI
ÖLÇEK / TARİH / PAFTA NO	1/100 | 19.10.2026 | 01-01
PROJE MÜELLİFİ	Elektrik Mühendisi - Adı Soyadı: .....
ODA SİCİL / SMM NO	EMO Sicil No: ..... SMM Belge No: ..... İmza: .....

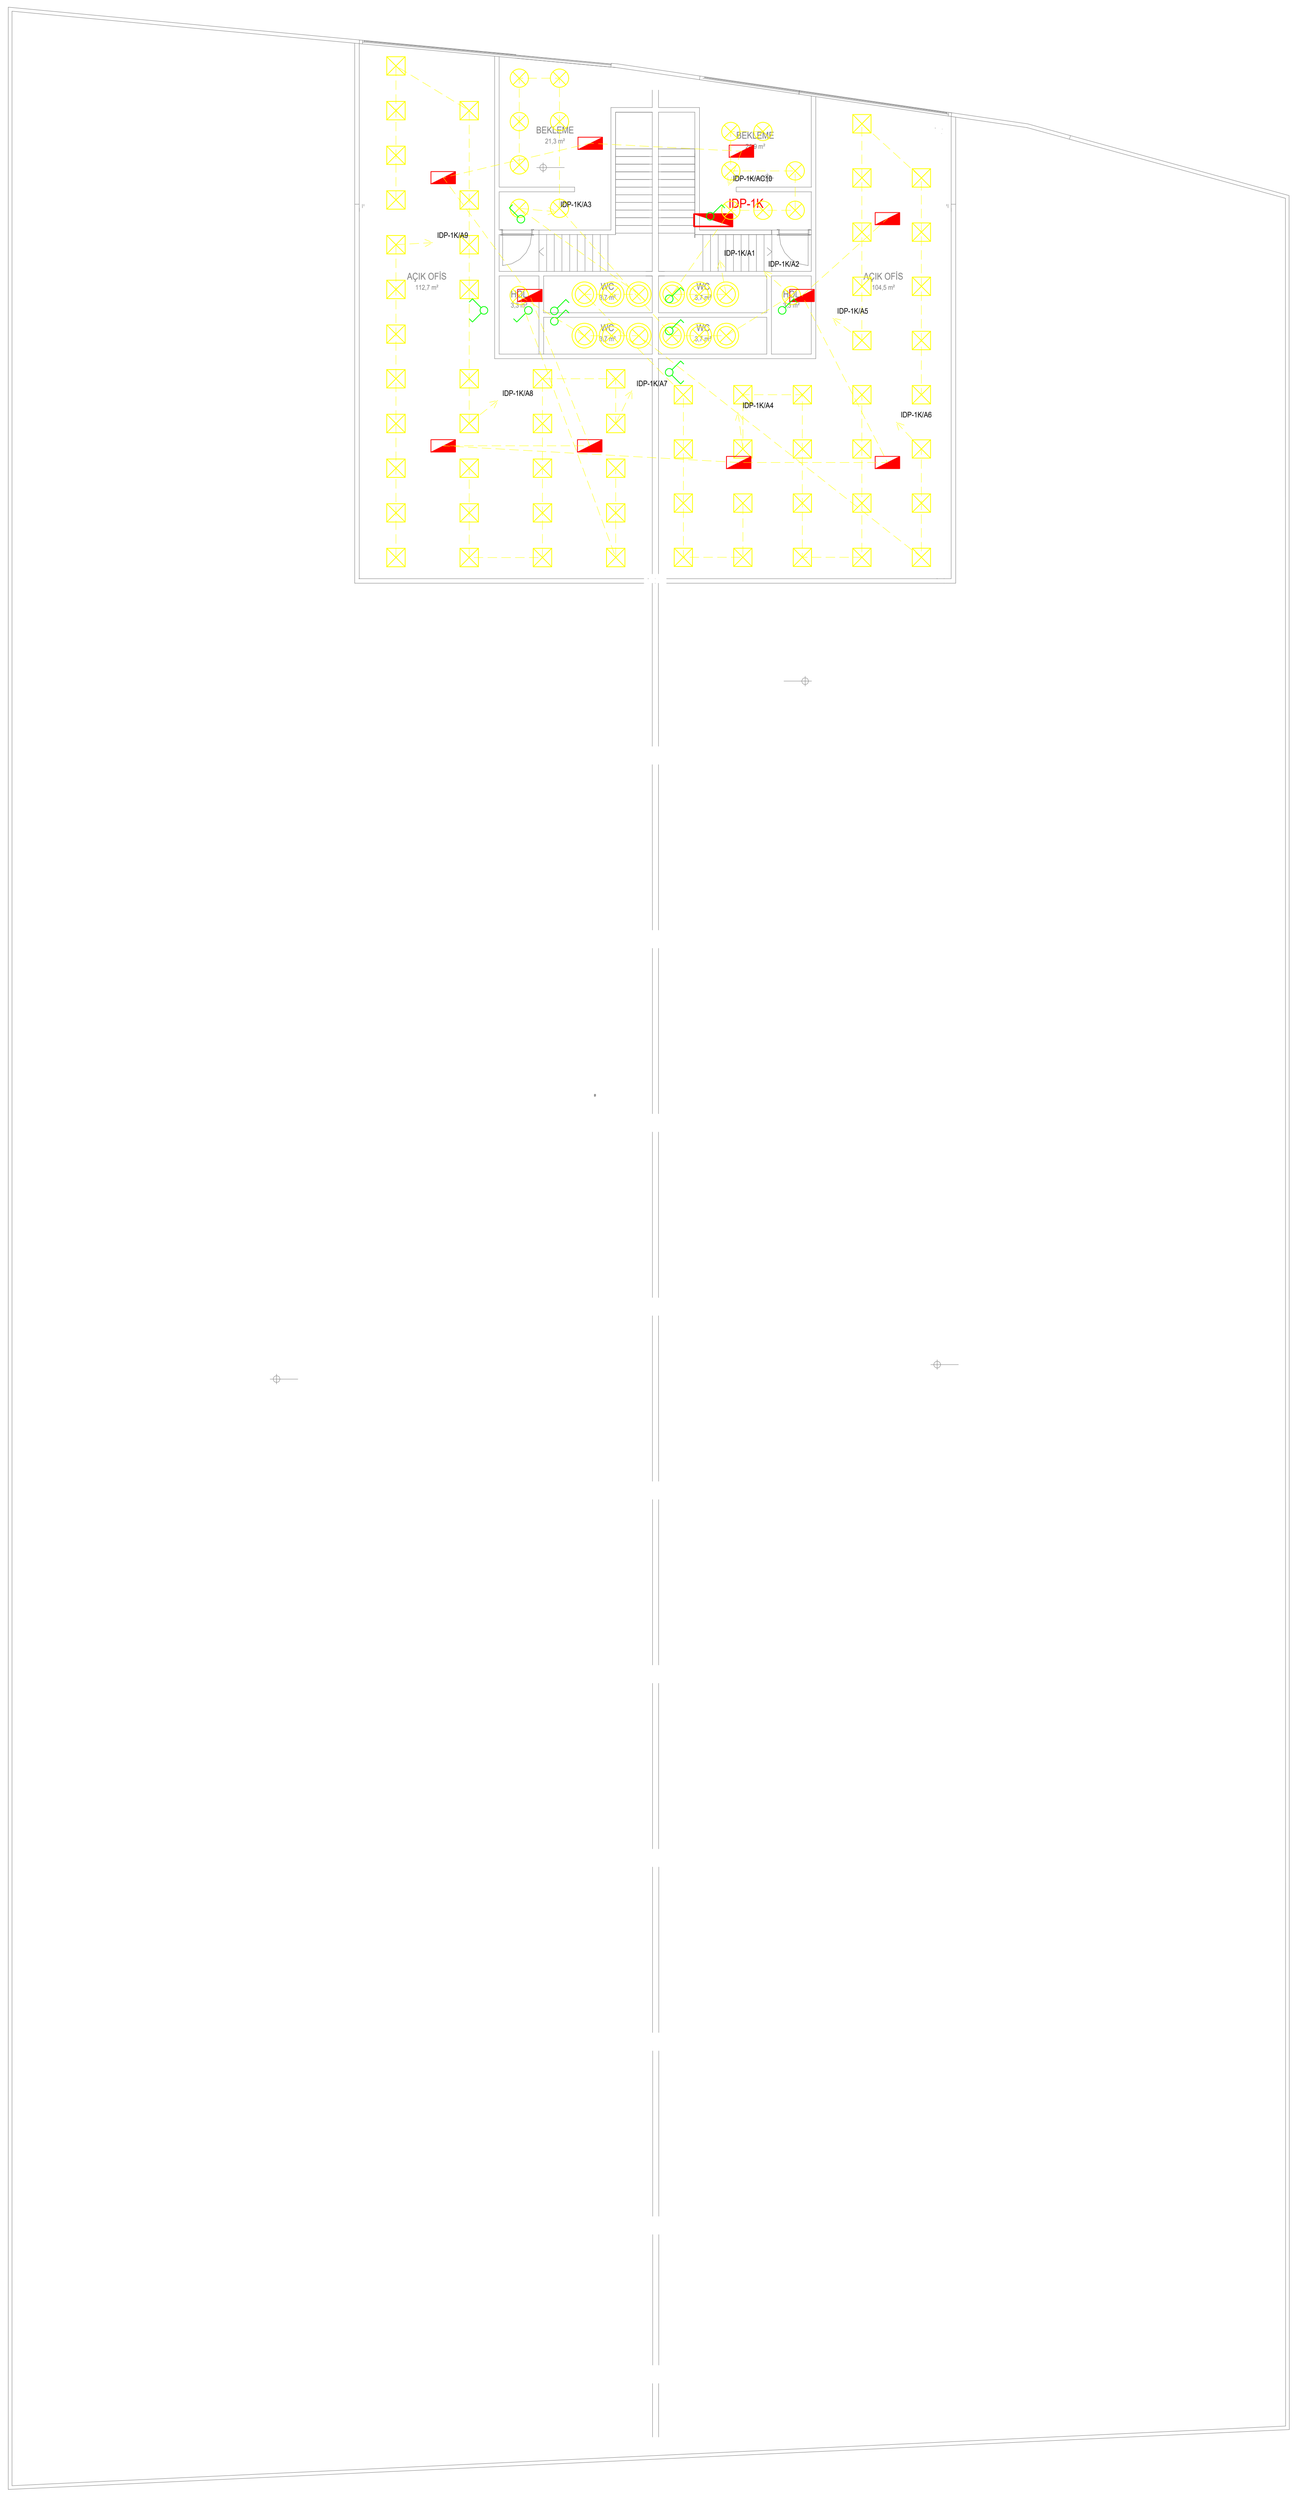

LEJANT

- LED yüksek tavan (highbay) armatürü 150 W, 21.000 lm, IP65
- LED panel armatür 60x60, 36 W, 3.600 lm, UGR<19
- LED downlight 18 W, 1.800 lm, IP20
- LED downlight 12 W, 1.200 lm, IP44 (ıslak hacim)
- LED etanj armatür 36 W, 4.000 lm, IP65
- LED acil aydınlatma armatürü 3 W, 3 saat, sürekli/sürekli olmayan
- LED çıkış/yönlendirme armatürü 3 W, 3 saat
- AK: 3 saat acil kitli armatür (sürekli faz ile beslenir)
- Adi anahtar (h=110 cm)
- Komütatör anahtar
- Vavien anahtar
- Tali dağıtım panosu (UTP / IDP)
- Aydınlatma linyesi, ok: panoya dönüş, etiket PANO/LİNYE

AYDINLATMA TESİSATI PLANI

1. KAT PLANI - Ö: 1/100

Parsel 4 | BROSCO İTHALAT İHRACAT VE TİCARET ANONİM ŞİRKETİ

CLD - 19.10.2026 - mimari altlık: BROSCO 4 NOLU PARSEL MİMARİ.dwg

İŞİN ADI	ELEKTRİK İÇ TESİSAT PROJESİ
YAPI SAHİBİ	BROSCO İTHALAT İHRACAT VE TİCARET ANONİM ŞİRKETİ
ADRES	ULUCAK / KEMALPAŞA / İZMİR - Ada: ..... Parsel: 4
PAFTA ADI	AYDINLATMA TESİSATI PLANI - 1. KAT PLANI
ÖLÇEK / TARİH / PAFTA NO	1/100 | 19.10.2026 | 01-02
PROJE MÜELLİFİ	Elektrik Mühendisi - Adı Soyadı: .....
ODA SİCİL / SMM NO	EMO Sicil No: ..... SMM Belge No: ..... İmza: .....

LEJANT

- Topraklı priz 16 A (h=40 cm, tezgah h=110 cm)
- Bilgisayar prizi (ayrı hinye, UPS hazırlığı)
- Etanj priz IP44
- Endüstriyel priz grubu CEE 32A+16A+2x16A (iç koruma, h=150 cm)
- IS — Ani su ısıtıcı çıkışı (IS) - ayrı hinye
- TS — Elektrikli termosifon çıkışı (TS) - ayrı hinye
- B — Bulaşık makinesi çıkışı (B) - ayrı hinye
- A — Havalandırma cihazı / aspiratör çıkışı (A) - ayrı hinye
- Tali dağıtım panosu (UTP / İDP)
- Priz / kuvvet hinyesi, ok: panoya dönüş


PRİZ VE KUVVET TESİSATI PLANI

ZEMİN KAT PLANI - Ö: 1/100

Parsel 4 | BROSCO İTHALAT İHRACAT VE TİCARET ANONİM ŞİRKETİ

CLD - 19.10.2026 - mimari altlık: BROSCO 4 NOLU PARSEL MİMARİ.dwg

İŞİN ADI	ELEKTRİK İÇ TESİSAT PROJESİ
YAPI SAHİBİ	BROSCO İTHALAT İHRACAT VE TİCARET ANONİM ŞİRKETİ
ADRES	ULUCAK / KEMALPAŞA / İZMİR - Ada: ..... Parsel: 4
PAFTA ADI	PRİZ VE KUVVET TESİSATI PLANI - ZEMİN KAT PLANI
ÖLÇEK / TARİH / PAFTA NO	1/100 | 19.10.2026 | 01-03
PROJE MÜELLİFİ	Elektrik Mühendisi - Adı Soyadı: .....
ODA SİCİL / SMM NO	EMO Sicil No: ..... SMM Belge No: ..... İmza: .....

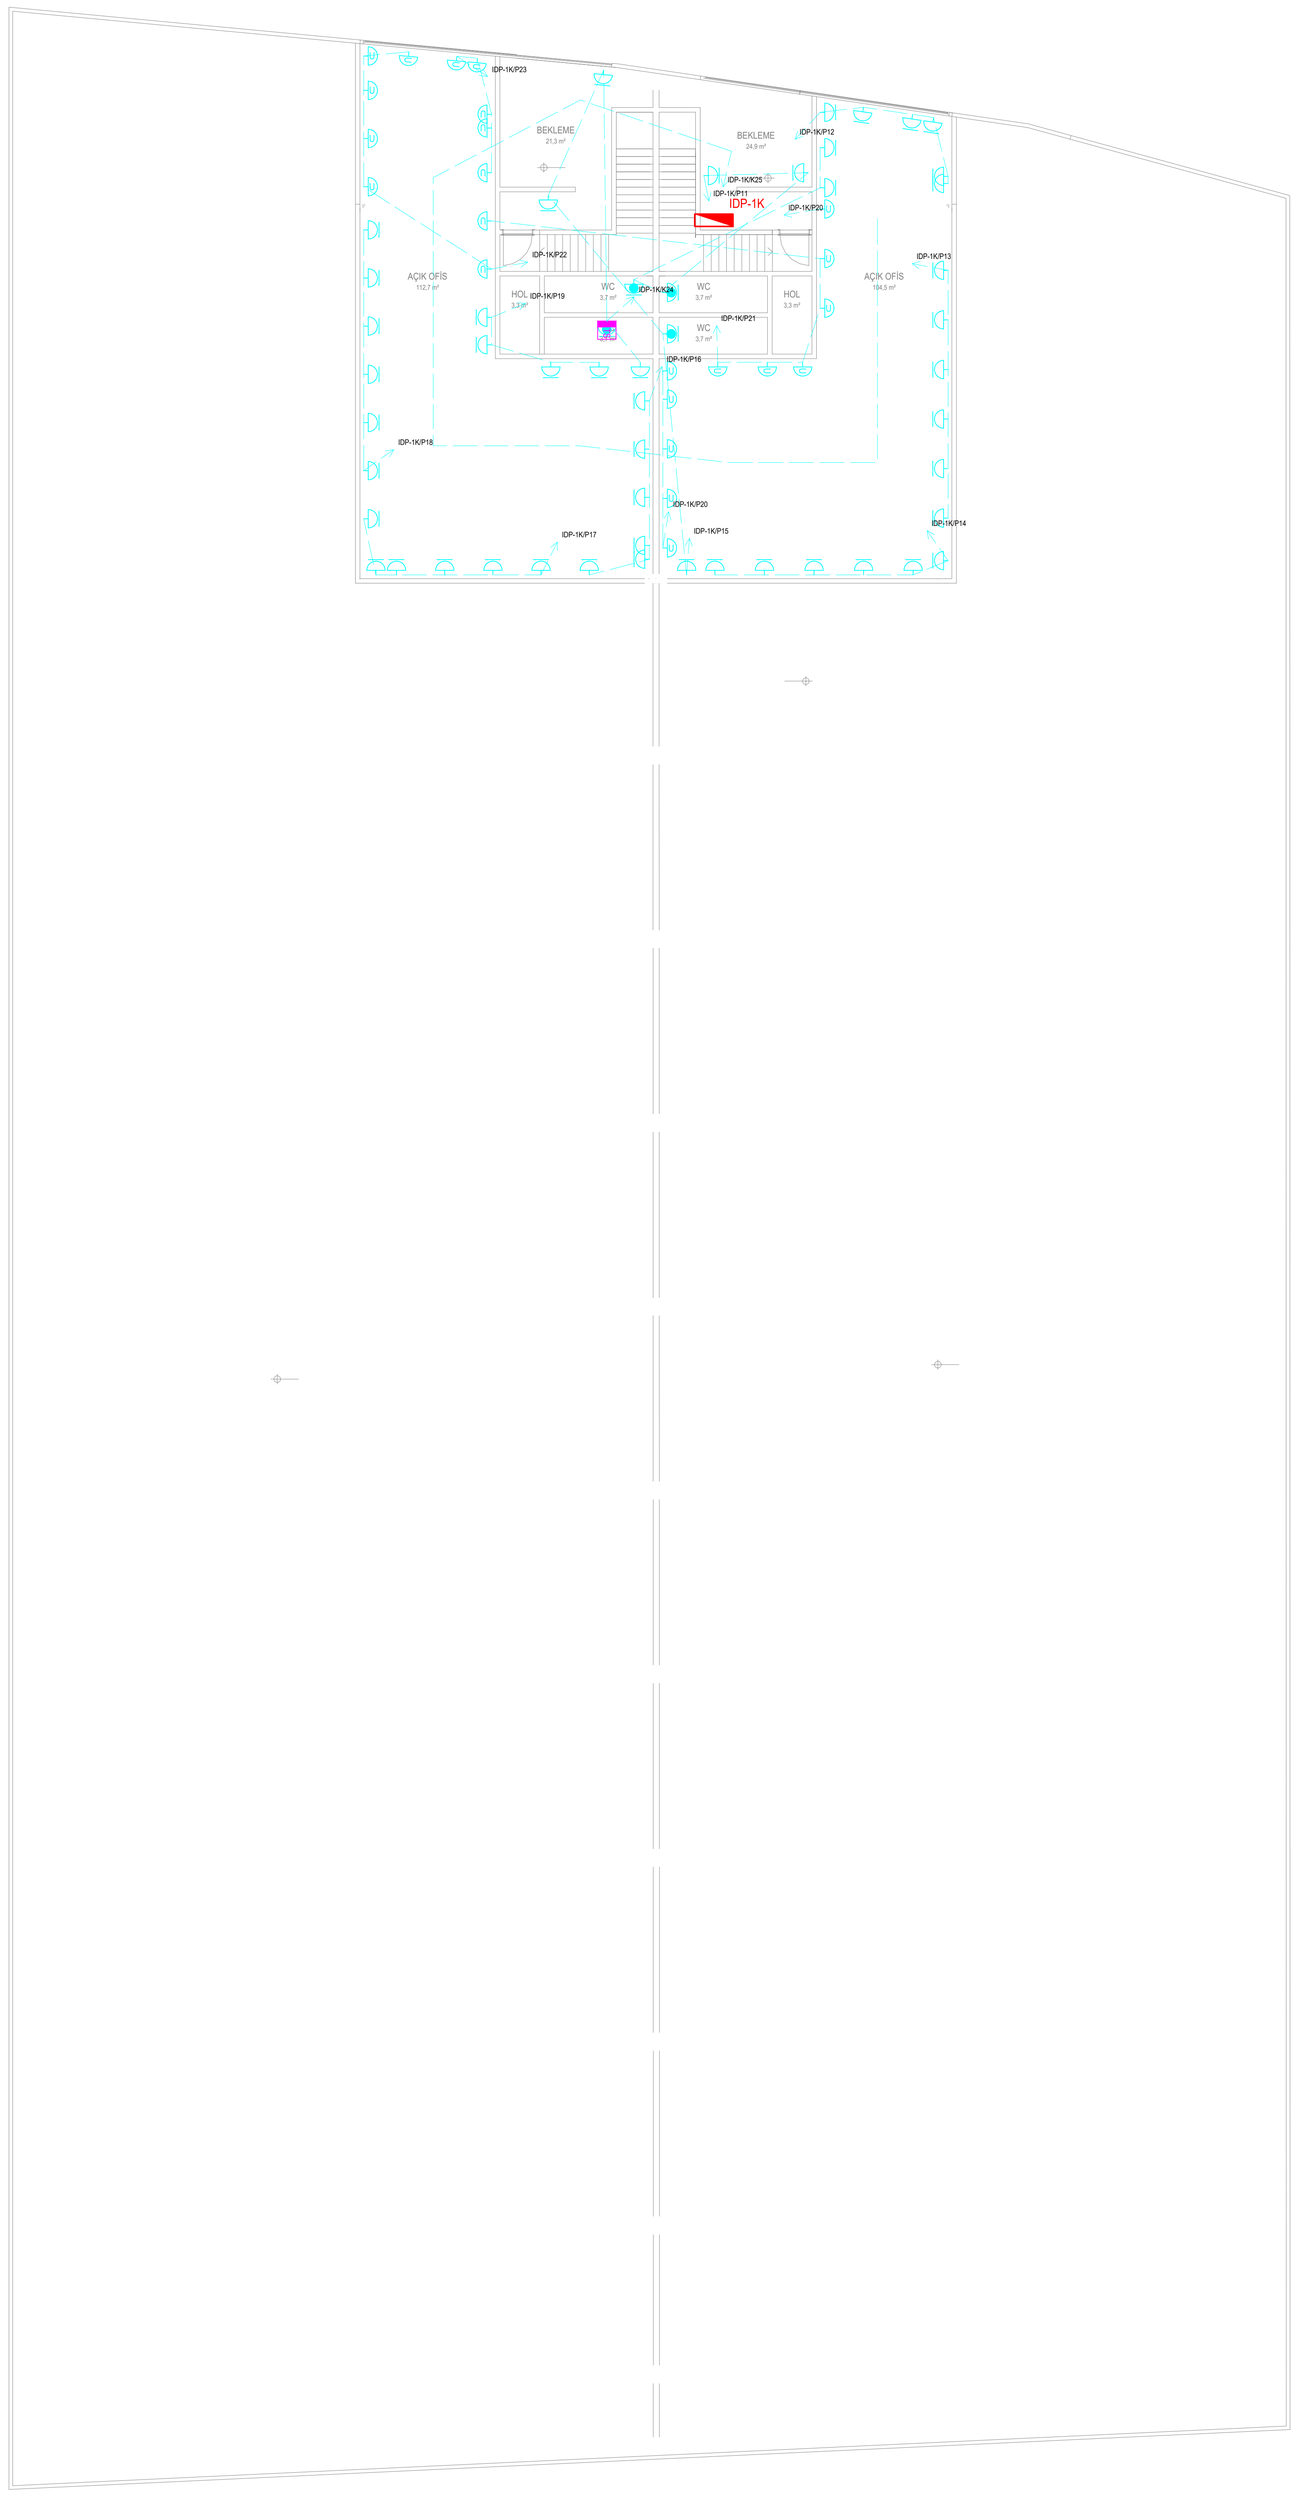

LEJANT

- Topraklı priz 16 A (h=40 cm, tezgah h=110 cm)
- Bilgisayar prizi (ayrı linye, UPS hazırlığı)
- Etanj priz IP44
- Endüstriyel priz grubu CEE 32A+16A+2x16A (iç koruma, h=150 cm)
- IS — Ani su ısıtıcı çıkışı (IS) - ayrı linye
- TS — Elektrikli termosifon çıkışı (TS) - ayrı linye
- B — Bulaşık makinesi çıkışı (B) - ayrı linye
- A — Havalandırma cihazı / aspiratör çıkışı (A) - ayrı linye
- Tali dağıtım panosu (UTP / İDP)
- Priz / kuvvet linyesi, ok: panoya dönüş

PRİZ VE KUVVET TESİSATI PLANI

1. KAT PLANI - Ö: 1/100

Parsel 4 | BROSCO İTHALAT İHRACAT VE TİCARET ANONİM ŞİRKETİ

CLD - 19.10.2026 - mimari altlık: BROSCO 4 NOLU PARSEL MİMARİ.dwg

İŞİN ADI	ELEKTRİK İÇ TESİSAT PROJESİ
YAPI SAHİBİ	BROSCO İTHALAT İHRACAT VE TİCARET ANONİM ŞİRKETİ
ADRES	ULUCAK / KEMALPAŞA / İZMİR - Ada: ..... Parsel: 4
PAFTA ADI	PRİZ VE KUVVET TESİSATI PLANI - 1. KAT PLANI
ÖLÇEK / TARİH / PAFTA NO	1/100 | 19.10.2026 | 01-04
PROJE MÜELLİFİ	Elektrik Mühendisi - Adı Soyadı: .....
ODA SİCİL / SMM NO	EMO Sicil No: ..... SMM Belge No: ..... İmza: .....

LEJANT

- LED yüksek tavan (highbay) armatürü 150 W, 21.000 lm, IP65
- LED panel armatür 60x60, 36 W, 3.600 lm, UGR<19
- LED downlight 18 W, 1.800 lm, IP20
- LED downlight 12 W, 1.200 lm, IP44 (ıslak hacim)
- LED etanj armatür 36 W, 4.000 lm, IP65
- LED acil aydınlatma armatürü 3 W, 3 saat, sürekli/sürekli olmayan
- LED çıkış/yönlendirme armatürü 3 W, 3 saat
- AK: 3 saat acil kitli armatür (sürekli faz ile beslenir)
- Adi anahtar (h=110 cm)
- Komütatör anahtar
- Vavien anahtar
- Tali dağıtım panosu (UTP / İDP)
- Aydınlatma linyesi, ok: panoya dönüş, etiket PANO/LİNYE
- Topraklı priz 16 A (h=40 cm, tezgah h=110 cm)
- Bilgisayar prizi (ayrı linye, UPS hazırlığı)
- Etanj priz IP44
- Endüstriyel priz grubu CEE 32A+16A+2x16A (iç koruma, h=150 cm)
- IS — Ani su ısıtıcı çıkışı (IS) - ayrı linye
- TS — Elektrikli termosifon çıkışı (TS) - ayrı linye
- B — Bulaşık makinesi çıkışı (B) - ayrı linye
- A — Havalandırma cihazı / aspiratör çıkışı (A) - ayrı linye
- Priz / kuvvet linyesi, ok: panoya dönüş

LİNYE LİSTESİ (1)

PANO	LİNYE	TÜR	AÇIKLAMA	ADET	GÜÇ (W)	FAZ	SİGORTA	KAÇAK AKIM	KABLO	L (m)	%e
IDP-ZK	A1	Aydınlatma	Aydınlatma	10	162	S	B10A	30 mA	NYM 3x1,5 mm²	20,6	0,15
IDP-ZK	A2	Aydınlatma	Aydınlatma	10	144	T	B10A	30 mA	NYM 3x1,5 mm²	26,7	0,17
IDP-ZK	A3	Aydınlatma	Aydınlatma	10	180	T	B10A	30 mA	NYM 3x1,5 mm²	41,3	0,33
IDP-ZK	A4	Aydınlatma	Aydınlatma	5	60	R	B10A	30 mA	NYM 3x1,5 mm²	26,0	0,07
IDP-ZK	A5	Aydınlatma	Aydınlatma	10	288	T	B10A	30 mA	NYM 3x1,5 mm²	45,4	0,59
IDP-ZK	A6	Aydınlatma	Aydınlatma	10	360	T	B10A	30 mA	NYM 3x1,5 mm²	41,4	0,67
IDP-ZK	A7	Aydınlatma	Aydınlatma	10	360	S	B10A	30 mA	NYM 3x1,5 mm²	34,3	0,56
IDP-ZK	A8	Aydınlatma	Aydınlatma	10	312	S	B10A	30 mA	NYM 3x1,5 mm²	45,0	0,63
IDP-ZK	A9	Aydınlatma	Aydınlatma	10	360	T	B10A	30 mA	NYM 3x1,5 mm²	28,8	0,47
IDP-ZK	A10	Aydınlatma	Aydınlatma	10	360	R	B10A	30 mA	NYM 3x1,5 mm²	34,9	0,56
IDP-ZK	A11	Aydınlatma	Aydınlatma	7	180	R	B10A	30 mA	NYM 3x1,5 mm²	29,8	0,24
IDP-ZK	AC12	Acil ayd.	Acil aydınlatma / yönlendirme	15	45	S	B10A	30 mA	NYM 3x1,5 mm²	57,5	0,12
IDP-ZK	AC13	Acil ayd.	Acil aydınlatma / yönlendirme	4	12	S	B10A	30 mA	NYM 3x1,5 mm²	34,1	0,02
IDP-ZK	P14	Priz	Priz	6	1.800	T	B16A	30 mA	NYM 3x2,5 mm²	28,6	1,39
IDP-ZK	P15	Priz	Priz	6	1.800	R	B16A	30 mA	NYM 3x2,5 mm²	24,1	1,17
IDP-ZK	P16	Priz	Priz	6	1.800	S	B16A	30 mA	NYM 3x2,5 mm²	24,3	1,18
IDP-ZK	P17	Priz	Priz	6	1.800	T	B16A	30 mA	NYM 3x2,5 mm²	26,4	1,28
IDP-ZK	P18	Priz	Priz	6	1.800	R	B16A	30 mA	NYM 3x2,5 mm²	21,3	1,03
IDP-ZK	P19	Priz	Priz	6	1.800	S	B16A	30 mA	NYM 3x2,5 mm²	27,1	1,32
IDP-ZK	P20	Priz	Priz	6	1.800	T	B16A	30 mA	NYM 3x2,5 mm²	30,0	1,46
IDP-ZK	P21	Priz	Priz	5	1.500	S	B16A	30 mA	NYM 3x4 mm²	43,0	1,09
IDP-ZK	P22	Priz	Priz	1	300	S	B16A	30 mA	NYM 3x2,5 mm²	12,3	0,10
IDP-ZK	P23	Priz	Priz	3	900	T	B16A	30 mA	NYM 3x2,5 mm²	24,7	0,60
IDP-ZK	P24	Priz	Priz	6	1.800	R	B16A	30 mA	NYM 3x4 mm²	36,4	1,11
IDP-ZK	P25	Priz	Priz	2	600	S	B16A	30 mA	NYM 3x2,5 mm²	25,1	0,41
IDP-ZK	P26	Priz	Bilgisayar prizi (UPS hazırlığı)	6	1.800	S	B16A	30 mA A tipi	NYM 3x2,5 mm²	12,5	0,61
IDP-ZK	P27	Priz	Bilgisayar prizi (UPS hazırlığı)	6	1.800	T	B16A	30 mA A tipi	NYM 3x2,5 mm²	27,1	1,32
IDP-ZK	P28	Priz	Bilgisayar prizi (UPS hazırlığı)	6	1.800	R	B16A	30 mA A tipi	NYM 3x2,5 mm²	24,7	1,20
IDP-ZK	P29	Priz	Bilgisayar prizi (UPS hazırlığı)	1	300	R	B16A	30 mA A tipi	NYM 3x2,5 mm²	11,1	0,09
IDP-ZK	K30	Kuvvet	Ani su ısıtıcı 3,5 kW	1	3.500	R	B25A	30 mA	NYM 3x4 mm²	16,2	0,96
IDP-ZK	K31	Kuvvet	Ani su ısıtıcı 3,5 kW	1	3.500	S	B25A	30 mA	NYM 3x4 mm²	12,6	0,74
IDP-ZK	K32	Kuvvet	Sığınak havalandırma cihazı	1	750	T	B10A	30 mA	NYM 3x1,5 mm²	18,3	0,62
IDP-ZK	K33	Kuvvet	Elektrikli termosifon 80 L 2 kW	1	2.000	T	B16A	30 mA	NYM 3x2,5 mm²	7,4	0,40
IDP-ZK	K34	Kuvvet	VRF iç üniteleri besleme	8	580	R	B10A	30 mA A tipi	NYM 3x1,5 mm²	56,6	1,48
UTP-2	A1	Aydınlatma	Aydınlatma (yüksek tavan, AK: sürekli faz)	8	1.200	R	B16A	30 mA	NYM 4x4 mm²	65,2	1,32
UTP-2	A2	Aydınlatma	Aydınlatma (yüksek tavan, AK: sürekli faz)	8	1.200	S	B16A	30 mA	NYM 4x4 mm²	65,2	1,32
UTP-2	A3	Aydınlatma	Aydınlatma (yüksek tavan, AK: sürekli faz)	8	1.200	T	B16A	30 mA	NYM 4x4 mm²	63,5	1,29
UTP-2	A4	Aydınlatma	Aydınlatma (yüksek tavan)	1	150	T	B10A	30 mA	NYM 3x1,5 mm²	29,5	0,20
UTP-2	A5	Aydınlatma	Aydınlatma (yüksek tavan, AK: sürekli faz)	7	1.050	S	B16A	30 mA	NYM 4x4 mm²	74,7	1,32
UTP-2	A6	Aydınlatma	Aydınlatma (yüksek tavan, AK: sürekli faz)	8	1.200	R	B16A	30 mA	NYM 4x4 mm²	48,8	0,99
UTP-2	A7	Aydınlatma	Aydınlatma (yüksek tavan, AK: sürekli faz)	3	450	T	B10A	30 mA	NYM 4x1,5 mm²	38,5	0,78
UTP-2	AC8	Acil ayd.	Acil aydınlatma / yönlendirme	1	3	T	B10A	30 mA	NYM 3x1,5 mm²	23,5	0,00
UTP-2	AC9	Acil ayd.	Acil aydınlatma / yönlendirme	2	6	T	B10A	30 mA	NYM 3x1,5 mm²	46,3	0,01
UTP-2	AC10	Acil ayd.	Acil aydınlatma / yönlendirme	1	3	T	B10A	30 mA	NYM 3x1,5 mm²	49,0	0,01
UTP-2	G11	End. priz	End. priz grubu (4P C32+C16+2xB16)	1	5.000	RST	C32A	30 mA A tipi (kutu içi)	NYM 5x10 mm²	27,3	0,33

LİNYE LİSTESİ (2)

PANO	LİNYE	TÜR	AÇIKLAMA	ADET	GÜÇ (W)	FAZ	SİGORTA	KAÇAK AKIM	KABLO	L (m)	%e
UTP-2	G12	End. priz	End. priz grubu (4P C32+C16+2xB16)	1	5.000	RST	C32A	30 mA A tipi (kutu içi)	NYM 5x10 mm²	30,0	0,37
UTP-2	G13	End. priz	End. priz grubu (4P C32+C16+2xB16)	1	5.000	RST	C32A	30 mA A tipi (kutu içi)	NYM 5x10 mm²	45,9	0,56
UTP-2	G14	End. priz	End. priz grubu (4P C32+C16+2xB16)	1	5.000	RST	C32A	30 mA A tipi (kutu içi)	NYM 5x10 mm²	40,6	0,50
UTP-2	G15	End. priz	End. priz grubu (4P C32+C16+2xB16)	1	5.000	RST	C32A	30 mA A tipi (kutu içi)	NYM 5x10 mm²	15,8	0,19
UTP-2	G16	End. priz	End. priz grubu (4P C32+C16+2xB16)	1	5.000	RST	C32A	30 mA A tipi (kutu içi)	NYM 5x10 mm²	15,9	0,20
UTP-2	G17	End. priz	End. priz grubu (4P C32+C16+2xB16)	1	5.000	RST	C32A	30 mA A tipi (kutu içi)	NYM 5x10 mm²	41,6	0,51
UTP-2	G18	End. priz	End. priz grubu (4P C32+C16+2xB16)	1	5.000	RST	C32A	30 mA A tipi (kutu içi)	NYM 5x10 mm²	45,6	0,56
UTP-2	G19	End. priz	End. priz grubu (4P C32+C16+2xB16)	1	5.000	RST	C32A	30 mA A tipi (kutu içi)	NYM 5x10 mm²	33,1	0,41
UTP-2	K20	Kuvvet	Aydınlatma kumanda (kontaktör/saat rölesi)	1	50	T	B10A	30 mA	NYM 3x1,5 mm²	3,0	0,01
UTP-2	K21	Kuvvet	Seksiyonel kapı motoru (L≈25 m kabul)	1	750	RST	C10A	300 mA	NYM 5x1,5 mm²	25,0	0,14
UTP-1	A1	Aydınlatma	Aydınlatma (yüksek tavan, AK: sürekli faz)	8	1.200	R	B16A	30 mA	NYM 4x4 mm²	73,1	1,48
UTP-1	A2	Aydınlatma	Aydınlatma (yüksek tavan, AK: sürekli faz)	8	1.200	S	B16A	30 mA	NYM 4x4 mm²	61,1	1,24
UTP-1	A3	Aydınlatma	Aydınlatma (yüksek tavan, AK: sürekli faz)	8	1.200	T	B16A	30 mA	NYM 4x4 mm²	55,8	1,13
UTP-1	A4	Aydınlatma	Aydınlatma (yüksek tavan, AK: sürekli faz)	8	1.200	R	B16A	30 mA	NYM 4x4 mm²	69,5	1,41
UTP-1	A5	Aydınlatma	Aydınlatma (yüksek tavan, AK: sürekli faz)	8	1.200	S	B16A	30 mA	NYM 4x4 mm²	50,7	1,03
UTP-1	A6	Aydınlatma	Aydınlatma (yüksek tavan, AK: sürekli faz)	7	1.050	T	B16A	30 mA	NYM 4x2,5 mm²	50,7	1,44
UTP-1	AC7	Acil ayd.	Acil aydınlatma / yönlendirme	1	3	T	B10A	30 mA	NYM 3x1,5 mm²	21,6	0,00
UTP-1	AC8	Acil ayd.	Acil aydınlatma / yönlendirme	1	3	T	B10A	30 mA	NYM 3x1,5 mm²	53,3	0,01
UTP-1	AC9	Acil ayd.	Acil aydınlatma / yönlendirme	1	3	T	B10A	30 mA	NYM 3x1,5 mm²	25,6	0,00
UTP-1	G10	End. priz	End. priz grubu (4P C32+C16+2xB16)	1	5.000	RST	C32A	30 mA A tipi (kutu içi)	NYM 5x10 mm²	50,9	0,62
UTP-1	G11	End. priz	End. priz grubu (4P C32+C16+2xB16)	1	5.000	RST	C32A	30 mA A tipi (kutu içi)	NYM 5x10 mm²	29,9	0,37
UTP-1	G12	End. priz	End. priz grubu (4P C32+C16+2xB16)	1	5.000	RST	C32A	30 mA A tipi (kutu içi)	NYM 5x10 mm²	5,5	0,07
UTP-1	G13	End. priz	End. priz grubu (4P C32+C16+2xB16)	1	5.000	RST	C32A	30 mA A tipi (kutu içi)	NYM 5x10 mm²	31,9	0,39
UTP-1	G14	End. priz	End. priz grubu (4P C32+C16+2xB16)	1	5.000	RST	C32A	30 mA A tipi (kutu içi)	NYM 5x10 mm²	44,9	0,55
UTP-1	G15	End. priz	End. priz grubu (4P C32+C16+2xB16)	1	5.000	RST	C32A	30 mA A tipi (kutu içi)	NYM 5x10 mm²	46,5	0,57
UTP-1	G16	End. priz	End. priz grubu (4P C32+C16+2xB16)	1	5.000	RST	C32A	30 mA A tipi (kutu içi)	NYM 5x10 mm²	31,3	0,38
UTP-1	G17	End. priz	End. priz grubu (4P C32+C16+2xB16)	1	5.000	RST	C32A	30 mA A tipi (kutu içi)	NYM 5x10 mm²	27,0	0,33
UTP-1	G18	End. priz	End. priz grubu (4P C32+C16+2xB16)	1	5.000	RST	C32A	30 mA A tipi (kutu içi)	NYM 5x10 mm²	38,2	0,47
UTP-1	G19	End. priz	End. priz grubu (4P C32+C16+2xB16)	1	5.000	RST	C32A	30 mA A tipi (kutu içi)	NYM 5x10 mm²	44,0	0,54
UTP-1	K20	Kuvvet	Aydınlatma kumanda (kontaktör/saat rölesi)	1	50	T	B10A	30 mA	NYM 3x1,5 mm²	3,0	0,01
UTP-1	K21	Kuvvet	Seksiyonel kapı motoru (L≈25 m kabul)	1	750	RST	C10A	300 mA	NYM 5x1,5 mm²	25,0	0,14
IDP-1K	A1	Aydınlatma	Aydınlatma	10	162	T	B10A	30 mA	NYM 3x1,5 mm²	20,5	0,15
IDP-1K	A2	Aydınlatma	Aydınlatma	10	162	R	B10A	30 mA	NYM 3x1,5 mm²	27,9	0,20
IDP-1K	A3	Aydınlatma	Aydınlatma	10	270	T	B10A	30 mA	NYM 3x1,5 mm²	33,5	0,41
IDP-1K	A4	Aydınlatma	Aydınlatma	10	360	R	B10A	30 mA	NYM 3x1,5 mm²	30,1	0,49
IDP-1K	A5	Aydınlatma	Aydınlatma	10	360	R	B10A	30 mA	NYM 3x1,5 mm²	29,3	0,48
IDP-1K	A6	Aydınlatma	Aydınlatma	10	270	S	B10A	30 mA	NYM 3x1,5 mm²	50,8	0,62
IDP-1K	A7	Aydınlatma	Aydınlatma	10	360	T	B10A	30 mA	NYM 3x1,5 mm²	28,5	0,46
IDP-1K	A8	Aydınlatma	Aydınlatma	10	360	R	B10A	30 mA	NYM 3x1,5 mm²	34,8	0,56
IDP-1K	A9	Aydınlatma	Aydınlatma	8	288	S	B10A	30 mA	NYM 3x1,5 mm²	26,7	0,35
IDP-1K	AC10	Acil ayd.	Acil aydınlatma / yönlendirme	10	30	T	B10A	30 mA	NYM 3x1,5 mm²	62,5	0,08
IDP-1K	P11	Priz	Priz	6	1.800	S	B16A	30 mA	NYM 3x2,5 mm²	26,4	1,29
IDP-1K	P12	Priz	Priz	6	1.800	T	B16A	30 mA	NYM 3x2,5 mm²	15,7	0,76
IDP-1K	P13	Priz	Priz	6	1.800	S	B16A	30 mA	NYM 3x2,5 mm²	21,3	1,03
IDP-1K	P14	Priz	Priz	6	1.800	T	B16A	30 mA	NYM 3x2,5 mm²	27,2	1,32

LİNYE LİSTESİ (3)

PANO	LİNYE	TÜR	AÇIKLAMA	ADET	GÜÇ (W)	FAZ	SİGORTA	KAÇAK AKIM	KABLO	L (m)	%e
IDP-1K	P15	Priz	Priz	6	1.800	R	B16A	30 mA	NYM 3x4 mm²	48,5	1,47
IDP-1K	P16	Priz	Priz	6	1.800	S	B16A	30 mA	NYM 3x2,5 mm²	18,3	0,89
IDP-1K	P17	Priz	Priz	6	1.800	T	B16A	30 mA	NYM 3x2,5 mm²	26,0	1,26
IDP-1K	P18	Priz	Priz	6	1.800	R	B16A	30 mA	NYM 3x2,5 mm²	28,1	1,36
IDP-1K	P19	Priz	Priz	4	1.200	T	B16A	30 mA	NYM 3x2,5 mm²	17,2	0,56
IDP-1K	P20	Priz	Bilgisayar prizi (UPS hazırlığı)	6	1.800	S	B16A	30 mA A tipi	NYM 3x2,5 mm²	27,7	1,35
IDP-1K	P21	Priz	Bilgisayar prizi (UPS hazırlığı)	6	1.800	T	B16A	30 mA A tipi	NYM 3x2,5 mm²	27,7	1,35
IDP-1K	P22	Priz	Bilgisayar prizi (UPS hazırlığı)	6	1.800	R	B16A	30 mA A tipi	NYM 3x2,5 mm²	23,8	1,16
IDP-1K	P23	Priz	Bilgisayar prizi (UPS hazırlığı)	5	1.500	S	B16A	30 mA A tipi	NYM 3x2,5 mm²	19,7	0,80
IDP-1K	K24	Kuvvet	Elektrikli termosifon 80 L 2 kW	1	2.000	R	B16A	30 mA	NYM 3x2,5 mm²	8,4	0,45
IDP-1K	K25	Kuvvet	VRF iç üniteleri besleme	8	580	R	B10A	30 mA A tipi	NYM 3x1,5 mm²	54,1	1,41

NOTLAR

1- Tesisat Elektrik İç Tesisleri Yönetmeliği, TS HD 60364 ve TS EN 12464-1 esas alınarak hesaplanmıştır.
2- Aydınlatma ve priz tesisatı ayrı paftalarda gösterilmiştir; linye etiketi "PANO/LİNYE", ok yönü panoyu gösterir.
3- Kesitler IEC 60364-5-52 C yöntemi x 0,80 (ofis) / x 0,71 (üretim holü tavası, 40 °C) ile seçilmiştir; gerilim düşümü aydınlatma ve prizde ≤ %1,5, kuvvette ≤ %3 olacak şekilde linyeler bölünmüştür.
4- Kaçak akım: tüm tek fazlı son devreler (priz, aydınlatma, ıslak hacim, özel çıkış) 30 mA, bilgisayar/VRF A tipi; 3 fazlı motor devreleri 300 mA; pano girişleri 300 mA S (seçici) - TS HD 60364-4-41 411.3.3, EMO.
5- Ofis ve ıslak hacimlerde sıva altı spiral boru, üretim alanında galvaniz kablo tavası / boru kullanılacaktır.
6- "AK" acil kitli armatürler kontaktör öncesinden sürekli faz ile beslenir (NYM 4x..: L anahtarlı + L sürekli, TS EN 50172).
7- Acil ve yönlendirme armatürleri 3 saat bataryalıdır (Binaların Yangından Korunması Hakkında Yönetmelik, TS EN 1838).
8- Endüstriyel priz grubu kutusu içinde 4P C32, C16 ve 2xB16 sigortalar ile 30 mA (A tipi) kaçak akım rölesi bulunur.
9- Anahtarlar sahada kapı açılış yönüne göre kapı kanadının arkasında kalmayacak şekilde yerleştirilecektir.
10- Üretim alanı aydınlatması tali panodan kontaktör + saat rölesi ile kumanda edilir.

HESAP TABLOLARI, CETVELLER VE NOTLAR

ELEKTRİK İÇ TESİSAT PROJESİ - Ölçeksiz

İŞİN ADI	ELEKTRİK İÇ TESİSAT PROJESİ
YAPI SAHİBİ	BROSCO İTHALAT İHRACAT VE TİCARET ANONİM ŞİRKETİ
ADRES	ULUCAK / KEMALPAŞA / İZMİR - Ada: ..... Parsel: 4
PAFTA ADI	HESAP TABLOLARI VE NOTLAR
ÖLÇEK / TARİH / PAFTA NO	Ölçeksiz | 19.10.2026 | 01-05
PROJE MÜELLİFİ	Elektrik Mühendisi - Adı Soyadı: .....
ODA SİCİL / SMM NO	EMO Sicil No: ..... SMM Belge No: ..... İmza: .....