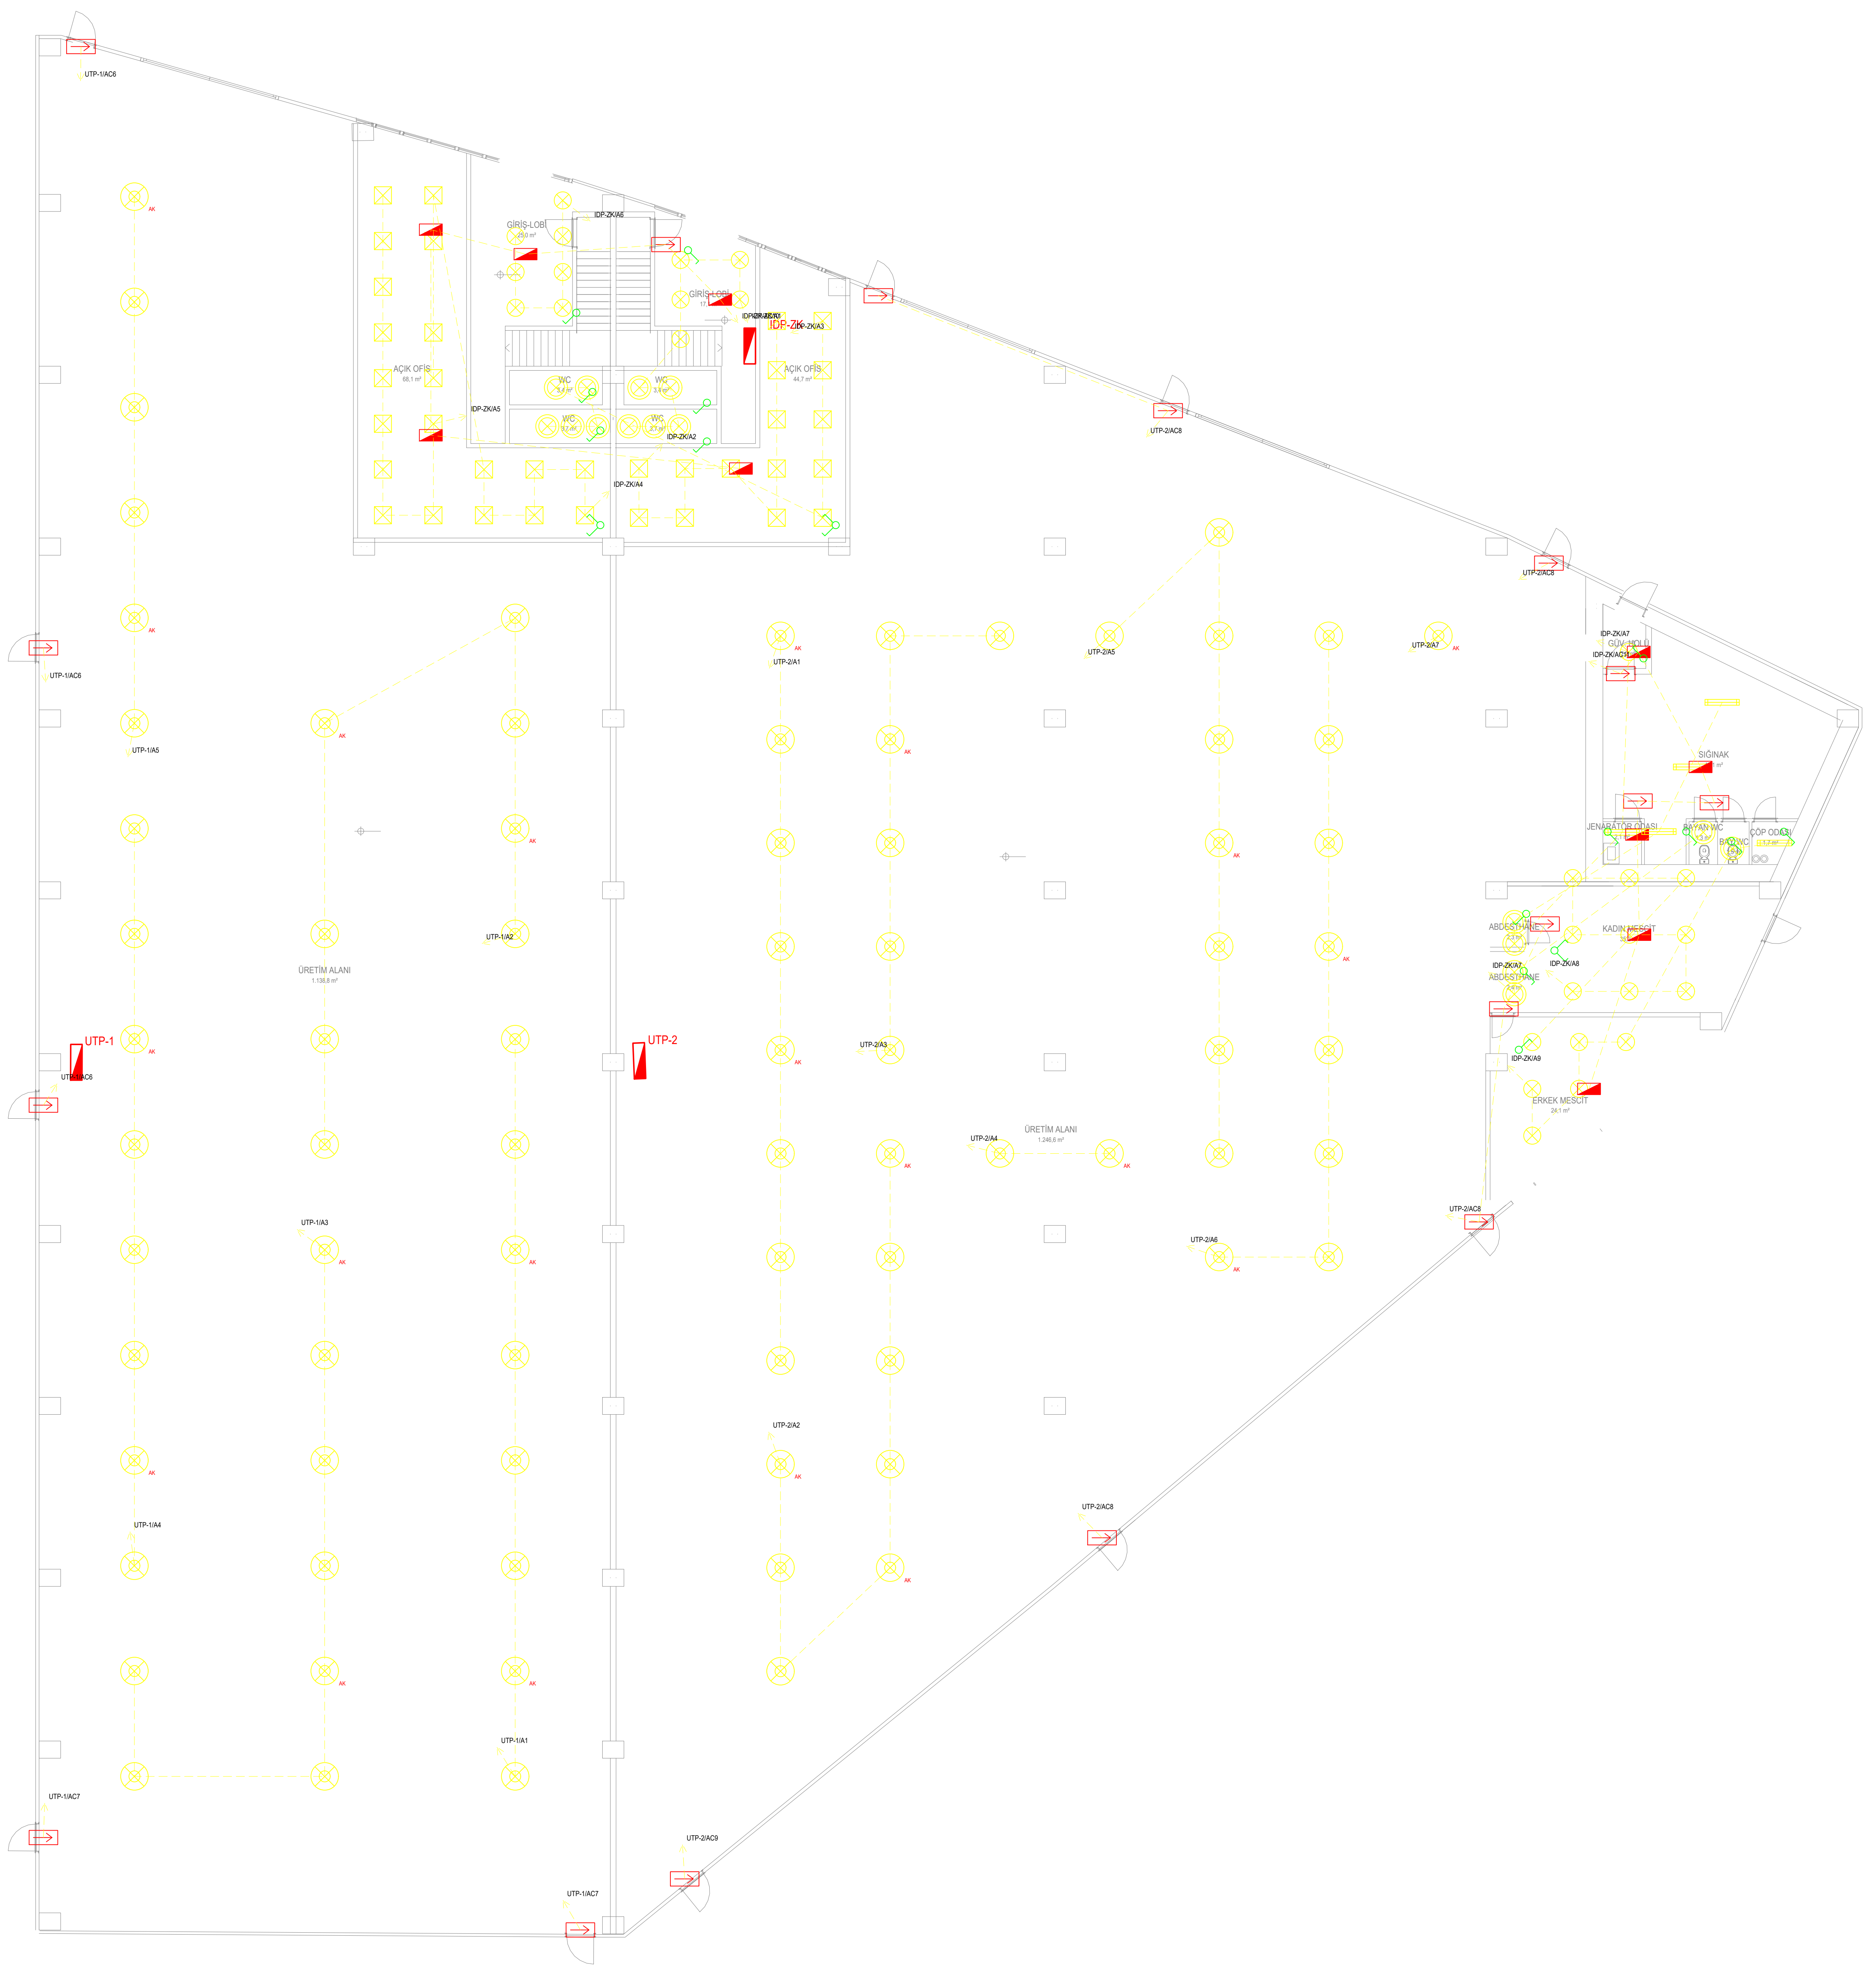

LEJANT

| | |
|---|---|
| ⊗ | LED yüksek tavan (highbay) armatürü 150 W, 21.000 lm, IP65 |
| ☒ | LED panel armatür 60x60, 36 W, 3.600 lm, UGR<19 |
| ⊗ | LED downlight 18 W, 1.800 lm, IP20 |
| ⊗ | LED downlight 12 W, 1.200 lm, IP44 (ıslak hacim) |
| ▭ | LED etanj armatür 36 W, 4.000 lm, IP65 |
| ◪ | LED acil aydınlatma armatürü 3 W, 3 saat, sürekli/sürekli olmayan |
| → | LED çıkış/yönlendirme armatürü 3 W, 3 saat |
| | AK: 3 saat acil kitli armatür (sürekli faz ile beslenir) |
| | Adi anahtar (h=110 cm) |
| | Komütatör anahtar |
| | Vavien anahtar |
| ◪ | Tali dağıtım panosu (UTP / İDP) |
| — — — | Aydınlatma linyesi, ok: panoya dönüş, etiket PANO/LİNYE |

# AYDINLATMA TESİSATI PLANI

ZEMİN KAT PLANI - Ö: 1/100

Parsel 5 | BROSCO İTHALAT İHRACAT VE TİCARET ANONİM ŞİRKETİ

CLD - 19.10.2026 - mimari altlık: BROSCO 5 NOLU PARSEL MİMARİ.dwg

| | |
|---|---|
| İŞİN ADI | ELEKTRİK İÇ TESİSAT PROJESİ |
| YAPI SAHİBİ | BROSCO İTHALAT İHRACAT VE TİCARET ANONİM ŞİRKETİ |
| ADRES | YUKARI MAHALLE / KEMALPAŞA / İZMİR - Ada: ...... Parsel: 5 |
| PAFTA ADI | AYDINLATMA TESİSATI PLANI - ZEMİN KAT PLANI |
| ÖLÇEK / TARİH / PAFTA NO | 1/100 \| 19.10.2026 \| 01-01 |
| PROJE MÜELLİFİ | Elektrik Mühendisi - Adı Soyadı: .............................. |
| ODA SİCİL / SMM NO | EMO Sicil No: ............ SMM Belge No: ............ İmza: ............ |

LEJANT

| | |
|---|---|
| ⊗ | LED yüksek tavan (highbay) armatürü 150 W, 21.000 lm, IP65 |
| ☒ | LED panel armatür 60x60, 36 W, 3.600 lm, UGR<19 |
| ⊗ | LED downlight 18 W, 1.800 lm, IP20 |
| ⊗ | LED downlight 12 W, 1.200 lm, IP44 (ıslak hacim) |
| ▭ | LED etanj armatür 36 W, 4.000 lm, IP65 |
| ◪ | LED acil aydınlatma armatürü 3 W, 3 saat, sürekli/sürekli olmayan |
| → | LED çıkış/yönlendirme armatürü 3 W, 3 saat |
| | AK: 3 saat acil kitli armatür (sürekli faz ile beslenir) |
| ○ | Adi anahtar (h=110 cm) |
| ○ | Komütatör anahtar |
| ○ | Vavien anahtar |
| ▮ | Tali dağıtım panosu (UTP / İDP) |
| — — — | Aydınlatma linyesi, ok: panoya dönüş, etiket PANO/LİNYE |

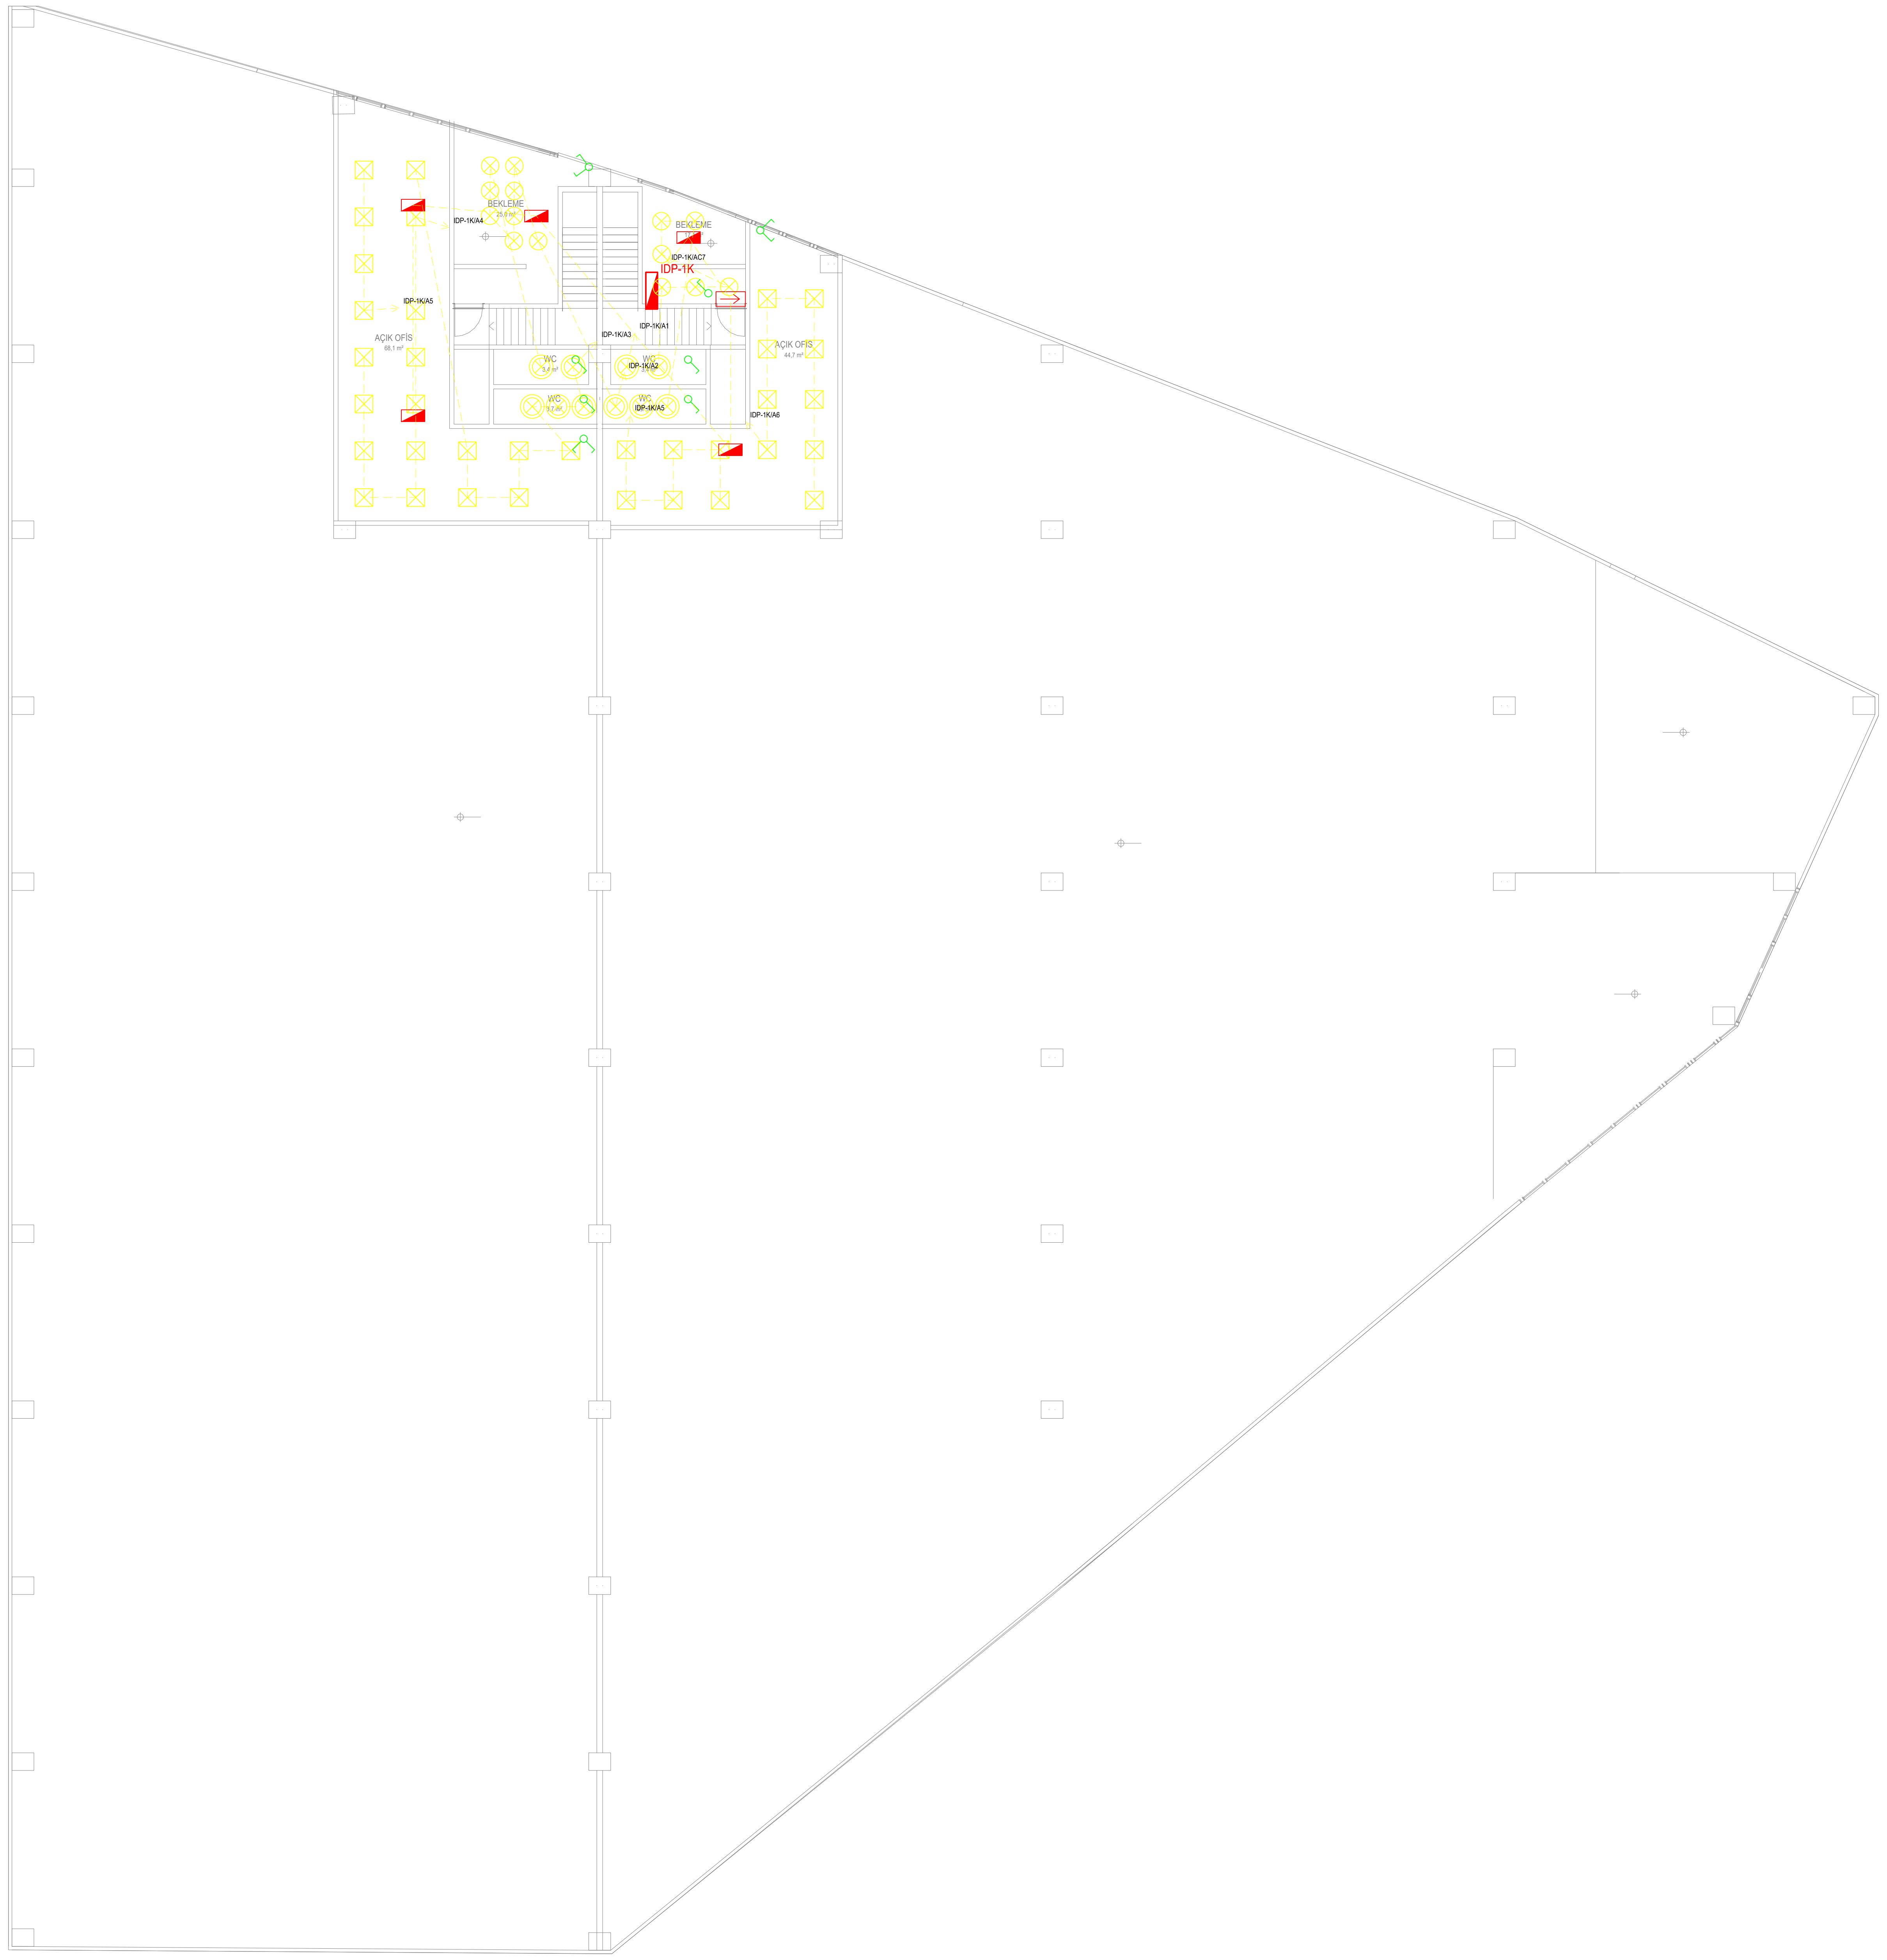

# AYDINLATMA TESİSATI PLANI

1. KAT PLANI - Ö: 1/100

Parsel 5 | BROSCO İTHALAT İHRACAT VE TİCARET ANONİM ŞİRKETİ

CLD - 19.10.2026 - mimari altlık: BROSCO 5 NOLU PARSEL MİMARİ.dwg

| | |
|---|---|
| İŞİN ADI | ELEKTRİK İÇ TESİSAT PROJESİ |
| YAPI SAHİBİ | BROSCO İTHALAT İHRACAT VE TİCARET ANONİM ŞİRKETİ |
| ADRES | YUKARI MAHALLE / KEMALPAŞA / İZMİR - Ada: ...... Parsel: 5 |
| PAFTA ADI | AYDINLATMA TESİSATI PLANI - 1. KAT PLANI |
| ÖLÇEK / TARİH / PAFTA NO | 1/100 \| 19.10.2026 \| 01-02 |
| PROJE MÜELLİFİ | Elektrik Mühendisi - Adı Soyadı: .............................. |
| ODA SİCİL / SMM NO | EMO Sicil No: ............ SMM Belge No: ............ İmza: ............ |

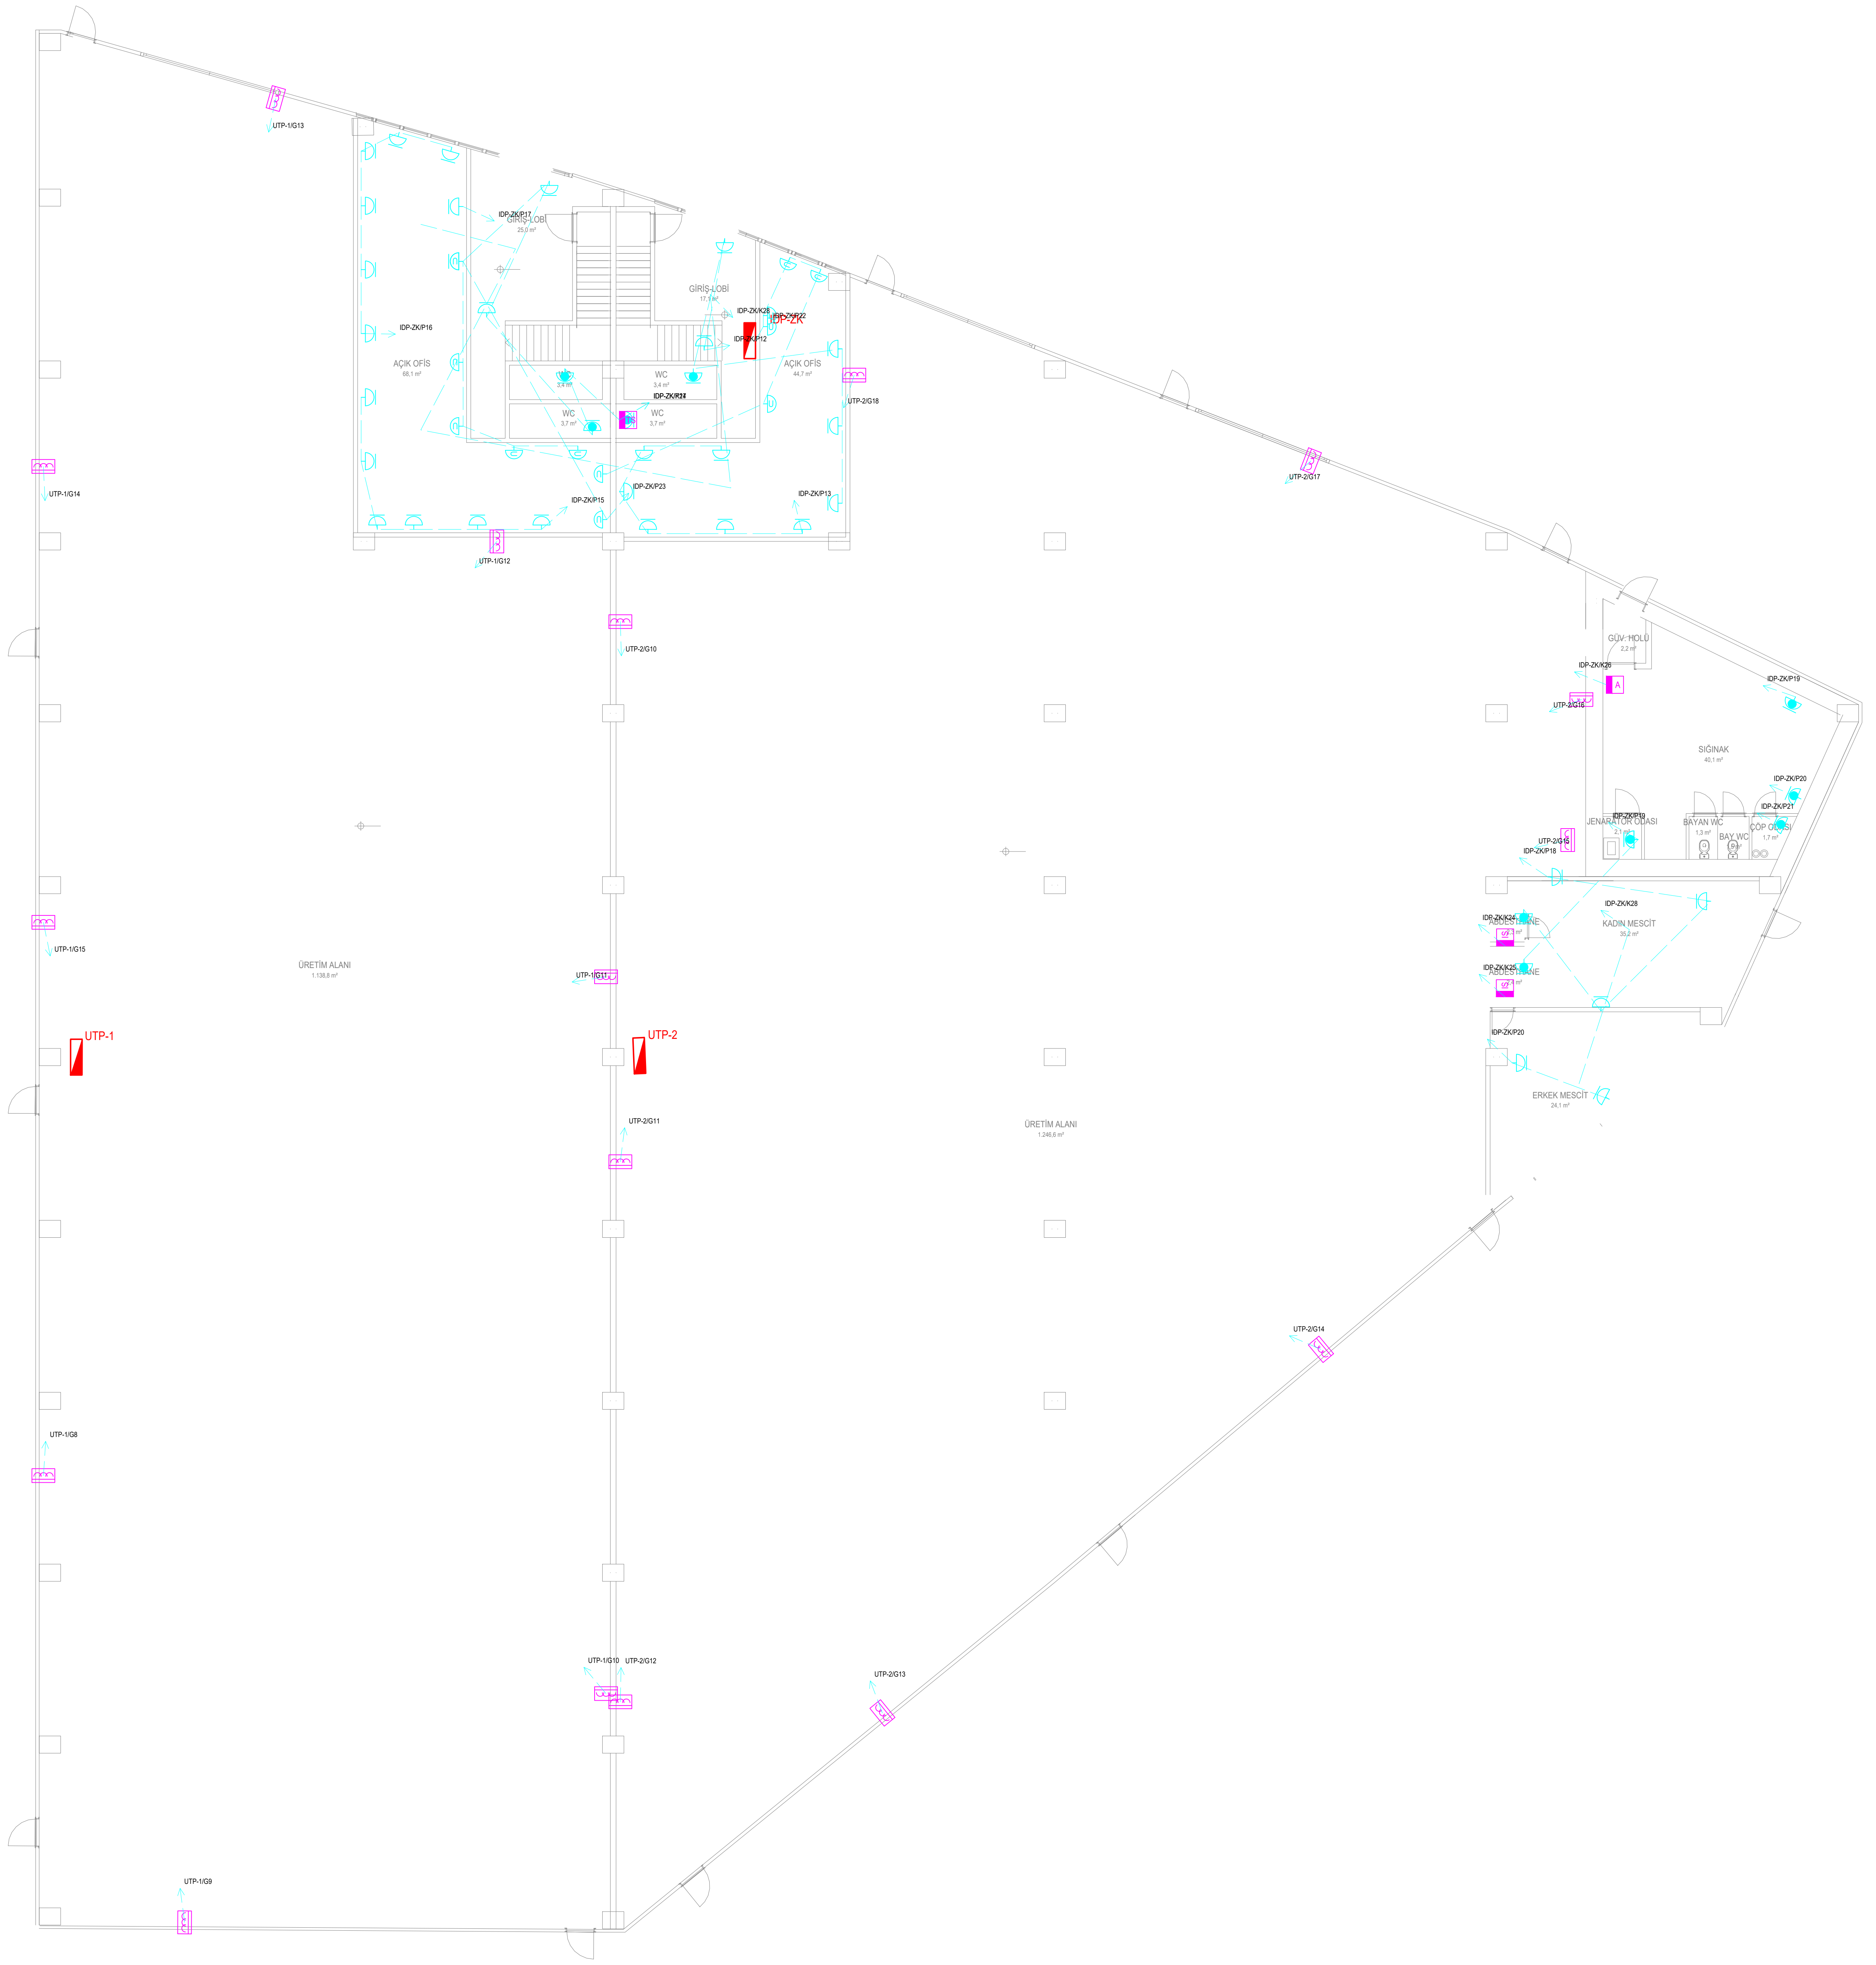

LEJANT

| | |
|---|---|
| ⊣D | Topraklı priz 16 A (h=40 cm, tezgah h=110 cm) |
| ⊣U | Bilgisayar prizi (ayrı linye, UPS hazırlığı) |
| ⊣● | Etanj priz IP44 |
| ▭ | Endüstriyel priz grubu CEE 32A+16A+2x16A (iç koruma, h=150 cm) |
| IS | Ani su ısıtıcı çıkışı (IS) - ayrı linye |
| TS | Elektrikli termosifon çıkışı (TS) - ayrı linye |
| B | Bulaşık makinesi çıkışı (B) - ayrı linye |
| A | Havalandırma cihazı / aspiratör çıkışı (A) - ayrı linye |
| ◩ | Tali dağıtım panosu (UTP / İDP) |
| — — — | Priz / kuvvet linyesi, ok: panoya dönüş |

# PRİZ VE KUVVET TESİSATI PLANI

## ZEMİN KAT PLANI - Ö: 1/100

Parsel 5 | BROSCO İTHALAT İHRACAT VE TİCARET ANONİM ŞİRKETİ

CLD - 19.10.2026 - mimari altlık: BROSCO 5 NOLU PARSEL MİMARİ.dwg

| | |
|---|---|
| İŞİN ADI | ELEKTRİK İÇ TESİSAT PROJESİ |
| YAPI SAHİBİ | BROSCO İTHALAT İHRACAT VE TİCARET ANONİM ŞİRKETİ |
| ADRES | YUKARI MAHALLE / KEMALPAŞA / İZMİR - Ada: ...... Parsel: 5 |
| PAFTA ADI | PRİZ VE KUVVET TESİSATI PLANI - ZEMİN KAT PLANI |
| ÖLÇEK / TARİH / PAFTA NO | 1/100 \| 19.10.2026 \| 01-03 |
| PROJE MÜELLİFİ | Elektrik Mühendisi - Adı Soyadı: .............................. |
| ODA SİCİL / SMM NO | EMO Sicil No: ............ SMM Belge No: ............ İmza: ............ |

LEJANT

| | |
|---|---|
| ◗ | Topraklı priz 16 A (h=40 cm, tezgah h=110 cm) |
| U | Bilgisayar prizi (ayrı linye, UPS hazırlığı) |
| ● | Etanj priz IP44 |
| ▭ | Endüstriyel priz grubu CEE 32A+16A+2x16A (iç koruma, h=150 cm) |
| IS | Ani su ısıtıcı çıkışı (IS) - ayrı linye |
| TS | Elektrikli termosifon çıkışı (TS) - ayrı linye |
| B | Bulaşık makinesi çıkışı (B) - ayrı linye |
| A | Havalandırma cihazı / aspiratör çıkışı (A) - ayrı linye |
| ◩ | Tali dağıtım panosu (UTP / İDP) |
| — — | Priz / kuvvet linyesi, ok: panoya dönüş |

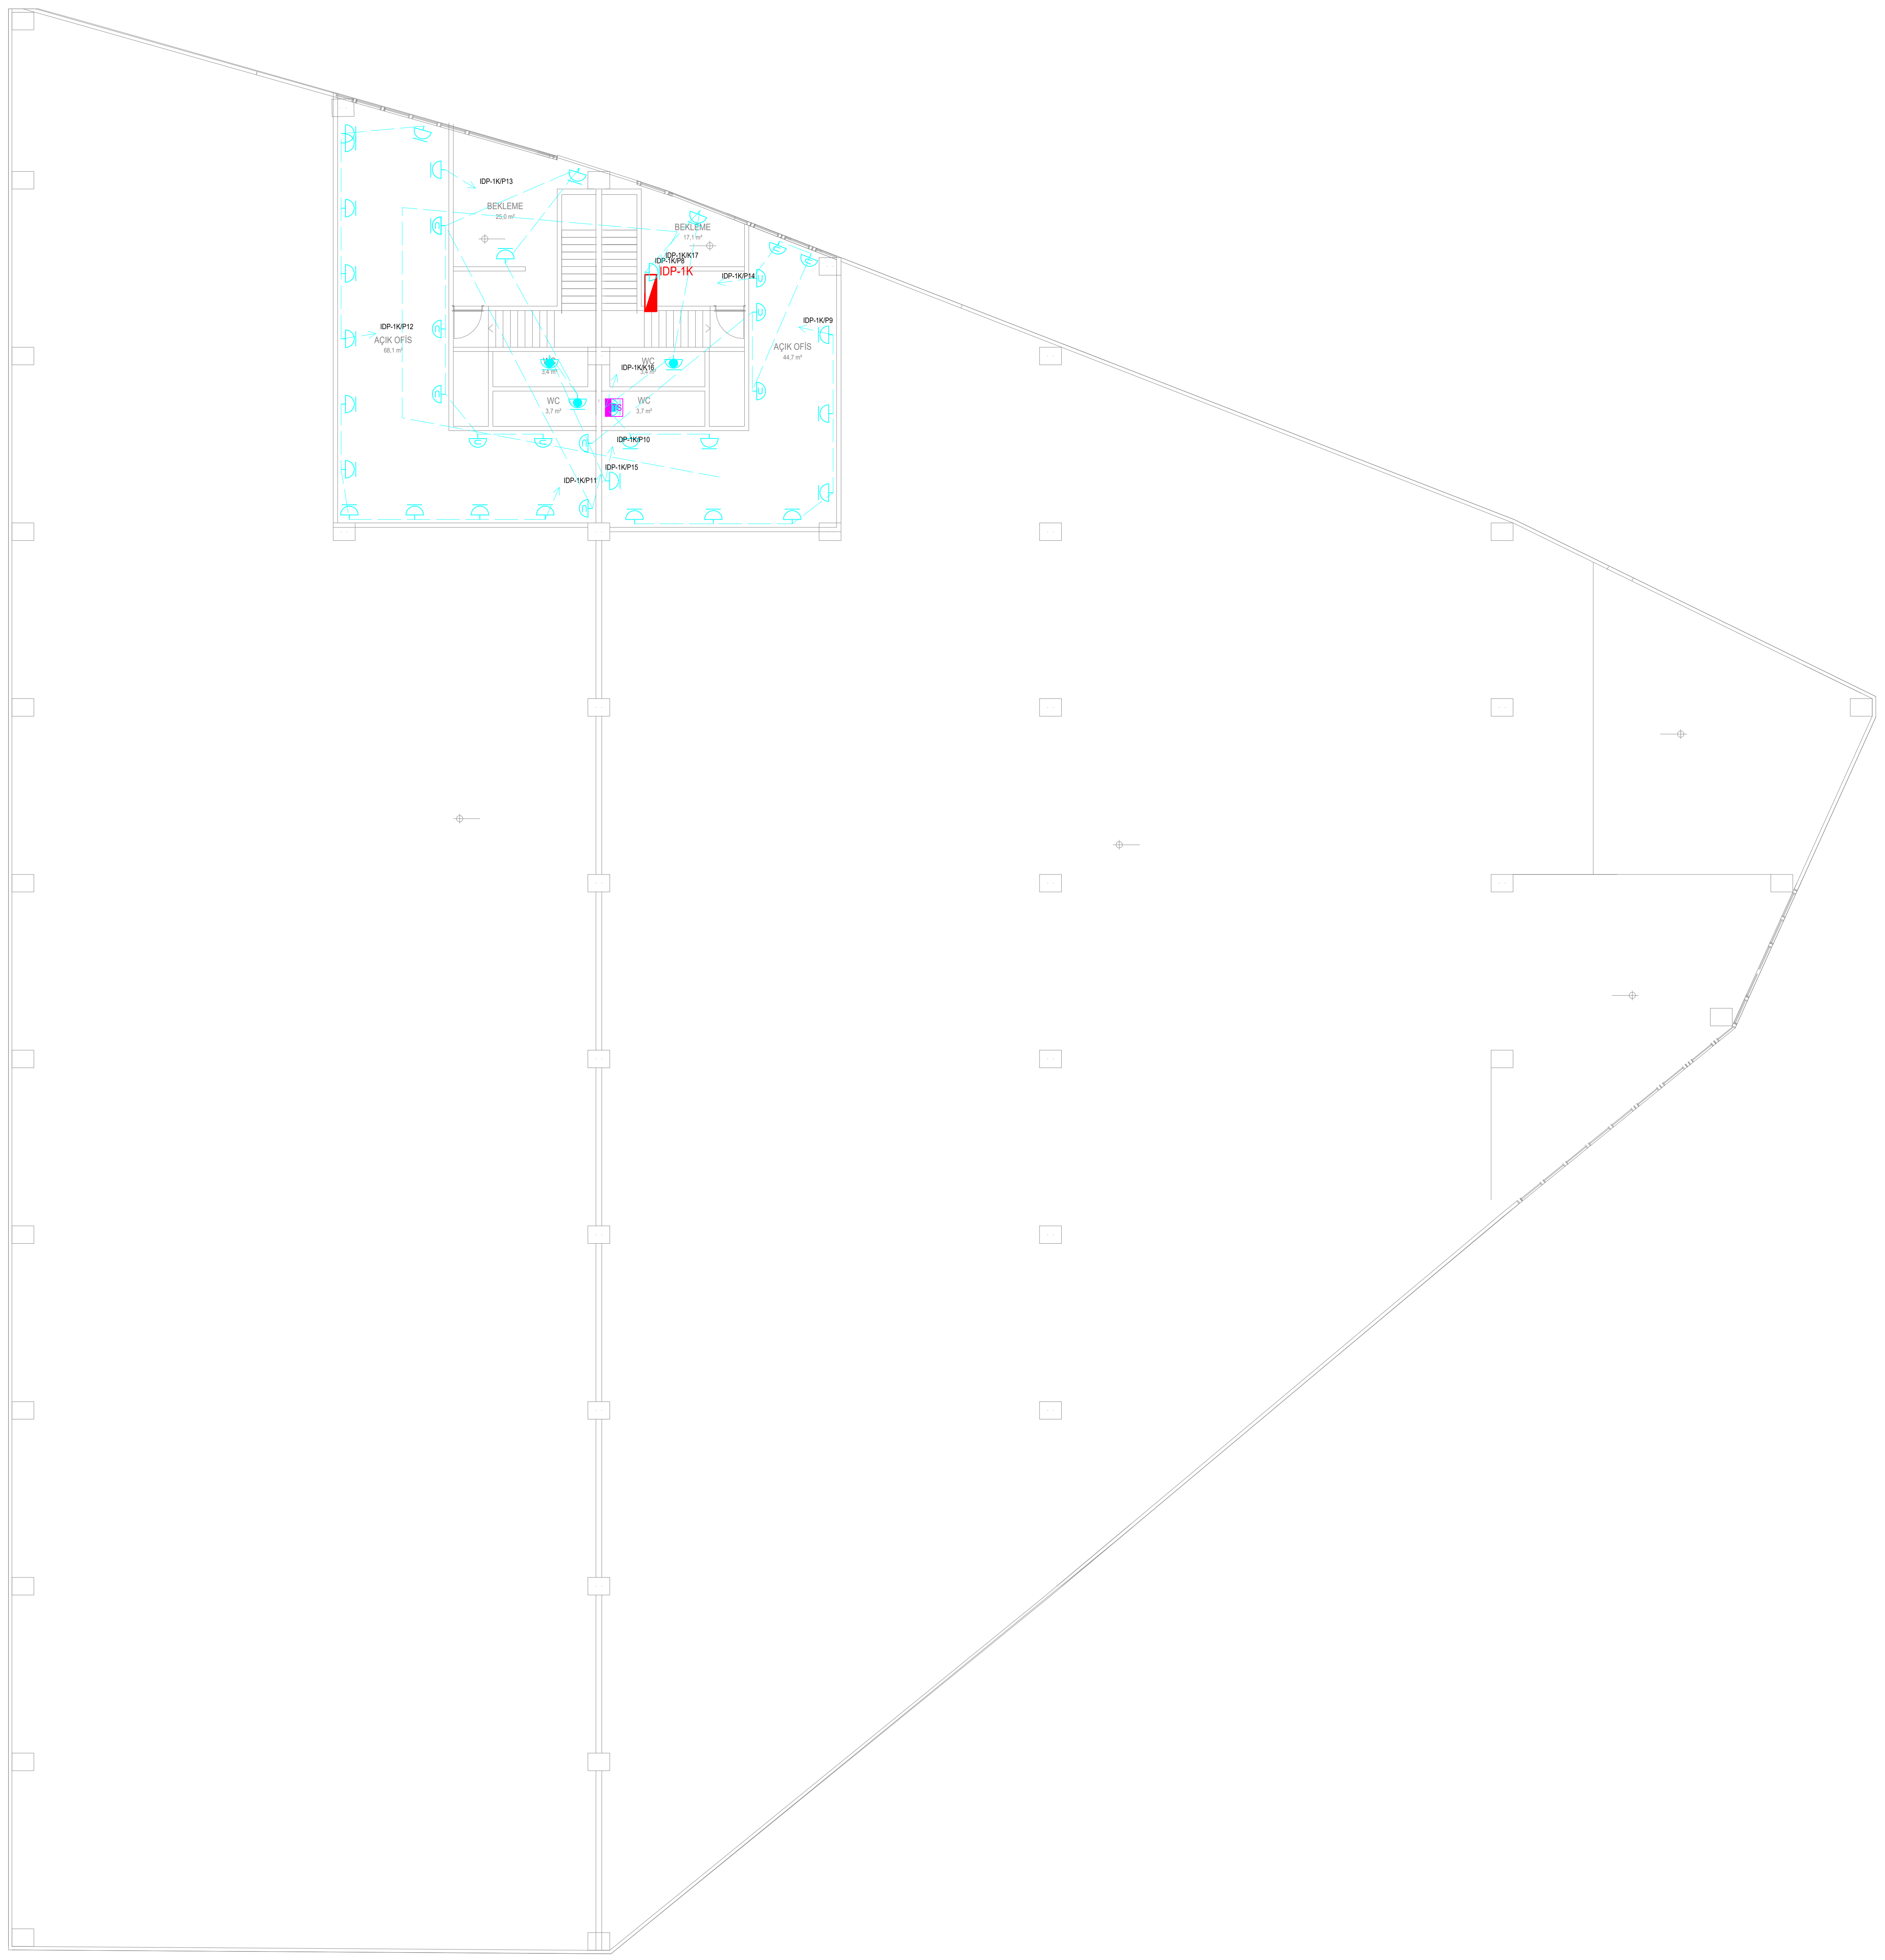

# PRİZ VE KUVVET TESİSATI PLANI

1. KAT PLANI - Ö: 1/100

Parsel 5 | BROSCO İTHALAT İHRACAT VE TİCARET ANONİM ŞİRKETİ

CLD - 19.10.2026 - mimari altlık: BROSCO 5 NOLU PARSEL MİMARİ.dwg

| | |
|---|---|
| İŞİN ADI | ELEKTRİK İÇ TESİSAT PROJESİ |
| YAPI SAHİBİ | BROSCO İTHALAT İHRACAT VE TİCARET ANONİM ŞİRKETİ |
| ADRES | YUKARI MAHALLE / KEMALPAŞA / İZMİR - Ada: ...... Parsel: 5 |
| PAFTA ADI | PRİZ VE KUVVET TESİSATI PLANI - 1. KAT PLANI |
| ÖLÇEK / TARİH / PAFTA NO | 1/100 \| 19.10.2026 \| 01-04 |
| PROJE MÜELLİFİ | Elektrik Mühendisi - Adı Soyadı: .............................. |
| ODA SİCİL / SMM NO | EMO Sicil No: ............ SMM Belge No: ............ İmza: ............ |

## LEJANT

| | |
|---|---|
| ⊗ | LED yüksek tavan (highbay) armatürü 150 W, 21.000 lm, IP65 |
| ⊠ | LED panel armatür 60x60, 36 W, 3.600 lm, UGR<19 |
| ⊗ | LED downlight 18 W, 1.800 lm, IP20 |
| ⊗ | LED downlight 12 W, 1.200 lm, IP44 (ıslak hacim) |
| ▭ | LED etanj armatür 36 W, 4.000 lm, IP65 |
| ◢ | LED acil aydınlatma armatürü 3 W, 3 saat, sürekli/sürekli olmayan |
| → | LED çıkış/yönlendirme armatürü 3 W, 3 saat |
| | AK: 3 saat acil kitli armatür (sürekli faz ile beslenir) |
| | Adi anahtar (h=110 cm) |
| | Komütatör anahtar |
| | Vavien anahtar |
| ◪ | Tali dağıtım panosu (UTP / İDP) |
| — — — | Aydınlatma linyesi, ok: panoya dönüş, etiket PANO/LİNYE |
| | Topraklı priz 16 A (h=40 cm, tezgah h=110 cm) |
| U | Bilgisayar prizi (ayrı linye, UPS hazırlığı) |
| ● | Etanj priz IP44 |
| | Endüstriyel priz grubu CEE 32A+16A+2x16A (iç koruma, h=150 cm) |
| IS | Ani su ısıtıcı çıkışı (IS) - ayrı linye |
| TS | Elektrikli termosifon çıkışı (TS) - ayrı linye |
| B | Bulaşık makinesi çıkışı (B) - ayrı linye |
| A | Havalandırma cihazı / aspiratör çıkışı (A) - ayrı linye |
| — — — | Priz / kuvvet linyesi, ok: panoya dönüş |

## LİNYE LİSTESİ (1)

| PANO | LİNYE | TÜR | AÇIKLAMA | ADET | GÜÇ (W) | FAZ | SİGORTA | KAÇAK AKIM | KABLO | L (m) | %e |
|---|---|---|---|---|---|---|---|---|---|---|---|
| IDP-ZK | A1 | Aydınlatma | Aydınlatma | 10 | 150 | R | B10A | 30 mA | NYM 3x1,5 mm² | 19,5 | 0,13 |
| IDP-ZK | A2 | Aydınlatma | Aydınlatma | 10 | 360 | T | B10A | 30 mA | NYM 3x1,5 mm² | 28,0 | 0,45 |
| IDP-ZK | A3 | Aydınlatma | Aydınlatma | 10 | 240 | S | B10A | 30 mA | NYM 3x1,5 mm² | 30,6 | 0,33 |
| IDP-ZK | A4 | Aydınlatma | Aydınlatma | 10 | 360 | T | B10A | 30 mA | NYM 3x1,5 mm² | 40,7 | 0,66 |
| IDP-ZK | A5 | Aydınlatma | Aydınlatma | 10 | 360 | S | B10A | 30 mA | NYM 3x1,5 mm² | 34,8 | 0,56 |
| IDP-ZK | A6 | Aydınlatma | Aydınlatma | 7 | 126 | T | B10A | 30 mA | NYM 3x1,5 mm² | 21,8 | 0,12 |
| IDP-ZK | A7 | Aydınlatma | Aydınlatma | 10 | 222 | T | B10A | 30 mA | NYM 3x1,5 mm² | 91,8 | 0,92 |
| IDP-ZK | A8 | Aydınlatma | Aydınlatma | 10 | 180 | S | B10A | 30 mA | NYM 3x1,5 mm² | 72,0 | 0,58 |
| IDP-ZK | A9 | Aydınlatma | Aydınlatma | 7 | 138 | R | B10A | 30 mA | NYM 3x1,5 mm² | 65,0 | 0,40 |
| IDP-ZK | AC10 | Acil ayd. | Acil aydınlatma / yönlendirme | 6 | 18 | S | B10A | 30 mA | NYM 3x1,5 mm² | 38,8 | 0,03 |
| IDP-ZK | AC11 | Acil ayd. | Acil aydınlatma / yönlendirme | 8 | 24 | S | B10A | 30 mA | NYM 3x1,5 mm² | 63,0 | 0,07 |
| IDP-ZK | P12 | Priz | Priz | 6 | 1.800 | T | B16A | 30 mA | NYM 3x2,5 mm² | 27,3 | 1,33 |
| IDP-ZK | P13 | Priz | Priz | 6 | 1.800 | R | B16A | 30 mA | NYM 3x2,5 mm² | 24,4 | 1,19 |
| IDP-ZK | P14 | Priz | Priz | 6 | 1.800 | S | B16A | 30 mA | NYM 3x4 mm² | 32,3 | 0,98 |
| IDP-ZK | P15 | Priz | Priz | 6 | 1.800 | T | B16A | 30 mA | NYM 3x2,5 mm² | 26,4 | 1,28 |
| IDP-ZK | P16 | Priz | Priz | 6 | 1.800 | R | B16A | 30 mA | NYM 3x2,5 mm² | 30,1 | 1,46 |
| IDP-ZK | P17 | Priz | Priz | 1 | 300 | T | B16A | 30 mA | NYM 3x2,5 mm² | 15,9 | 0,13 |
| IDP-ZK | P18 | Priz | Priz | 4 | 1.200 | R | B16A | 30 mA | NYM 3x4 mm² | 59,4 | 1,20 |
| IDP-ZK | P19 | Priz | Priz | 4 | 1.200 | S | B16A | 30 mA | NYM 3x4 mm² | 65,5 | 1,33 |
| IDP-ZK | P20 | Priz | Priz | 3 | 900 | T | B16A | 30 mA | NYM 3x4 mm² | 68,7 | 1,04 |
| IDP-ZK | P21 | Priz | Priz | 1 | 300 | R | B16A | 30 mA | NYM 3x2,5 mm² | 48,8 | 0,40 |
| IDP-ZK | P22 | Priz | Bilgisayar prizi (UPS hazırlığı) | 6 | 1.800 | S | B16A | 30 mA A tipi | NYM 3x2,5 mm² | 20,7 | 1,01 |
| IDP-ZK | P23 | Priz | Bilgisayar prizi (UPS hazırlığı) | 6 | 1.800 | T | B16A | 30 mA A tipi | NYM 3x4 mm² | 35,6 | 1,08 |
| IDP-ZK | K24 | Kuvvet | Ani su ısıtıcı 3,5 kW | 1 | 3.500 | R | B25A | 30 mA | NYM 3x4 mm² | 41,7 | 2,46 |
| IDP-ZK | K25 | Kuvvet | Ani su ısıtıcı 3,5 kW | 1 | 3.500 | S | B25A | 30 mA | NYM 3x4 mm² | 43,0 | 2,54 |
| IDP-ZK | K26 | Kuvvet | Sığınak havalandırma cihazı | 1 | 750 | R | B10A | 30 mA | NYM 3x1,5 mm² | 39,8 | 1,35 |
| IDP-ZK | K27 | Kuvvet | Elektrikli termosifon 80 L 2 kW | 1 | 2.000 | T | B16A | 30 mA | NYM 3x2,5 mm² | 9,3 | 0,50 |
| IDP-ZK | K28 | Kuvvet | VRF iç üniteleri besleme | 7 | 520 | S | B10A | 30 mA A tipi | NYM 3x1,5 mm² | 100,9 | 2,36 |
| UTP-1 | A1 | Aydınlatma | Aydınlatma (yüksek tavan, AK: sürekli faz) | 8 | 1.200 | R | B16A | 30 mA | NYM 4x4 mm² | 69,4 | 1,41 |
| UTP-1 | A2 | Aydınlatma | Aydınlatma (yüksek tavan, AK: sürekli faz) | 8 | 1.200 | S | B16A | 30 mA | NYM 4x4 mm² | 62,9 | 1,27 |
| UTP-1 | A3 | Aydınlatma | Aydınlatma (yüksek tavan, AK: sürekli faz) | 8 | 1.200 | T | B16A | 30 mA | NYM 4x4 mm² | 51,7 | 1,05 |
| UTP-1 | A4 | Aydınlatma | Aydınlatma (yüksek tavan, AK: sürekli faz) | 8 | 1.200 | R | B16A | 30 mA | NYM 4x4 mm² | 56,0 | 1,13 |
| UTP-1 | A5 | Aydınlatma | Aydınlatma (yüksek tavan, AK: sürekli faz) | 6 | 900 | S | B10A | 30 mA | NYM 4x2,5 mm² | 41,0 | 1,00 |
| UTP-1 | AC6 | Acil ayd. | Acil aydınlatma / yönlendirme | 3 | 9 | T | B10A | 30 mA | NYM 3x1,5 mm² | 47,6 | 0,02 |
| UTP-1 | AC7 | Acil ayd. | Acil aydınlatma / yönlendirme | 2 | 6 | T | B10A | 30 mA | NYM 3x1,5 mm² | 56,0 | 0,02 |
| UTP-1 | G8 | End. priz | End. priz grubu (4P C32+C16+2xB16) | 1 | 5.000 | RST | C32A | 30 mA A tipi (kutu içi) | NYM 5x10 mm² | 19,8 | 0,24 |
| UTP-1 | G9 | End. priz | End. priz grubu (4P C32+C16+2xB16) | 1 | 5.000 | RST | C32A | 30 mA A tipi (kutu içi) | NYM 5x10 mm² | 38,0 | 0,47 |
| UTP-1 | G10 | End. priz | End. priz grubu (4P C32+C16+2xB16) | 1 | 5.000 | RST | C32A | 30 mA A tipi (kutu içi) | NYM 5x10 mm² | 36,4 | 0,45 |
| UTP-1 | G11 | End. priz | End. priz grubu (4P C32+C16+2xB16) | 1 | 5.000 | RST | C32A | 30 mA A tipi (kutu içi) | NYM 5x10 mm² | 24,7 | 0,30 |
| UTP-1 | G12 | End. priz | End. priz grubu (4P C32+C16+2xB16) | 1 | 5.000 | RST | C32A | 30 mA A tipi (kutu içi) | NYM 5x10 mm² | 29,9 | 0,37 |
| UTP-1 | G13 | End. priz | End. priz grubu (4P C32+C16+2xB16) | 1 | 5.000 | RST | C32A | 30 mA A tipi (kutu içi) | NYM 5x10 mm² | 42,4 | 0,52 |
| UTP-1 | G14 | End. priz | End. priz grubu (4P C32+C16+2xB16) | 1 | 5.000 | RST | C32A | 30 mA A tipi (kutu içi) | NYM 5x10 mm² | 26,7 | 0,33 |
| UTP-1 | G15 | End. priz | End. priz grubu (4P C32+C16+2xB16) | 1 | 5.000 | RST | C32A | 30 mA A tipi (kutu içi) | NYM 5x10 mm² | 8,5 | 0,10 |
| UTP-1 | K16 | Kuvvet | Aydınlatma kumanda (kontaktör/saat rölesi) | 1 | 50 | T | B10A | 30 mA | NYM 3x1,5 mm² | 3,0 | 0,01 |
| UTP-1 | K17 | Kuvvet | Seksiyonel kapı motoru (L≈25 m kabul) | 1 | 750 | RST | C10A | 300 mA | NYM 5x1,5 mm² | 25,0 | 0,14 |

## LİNYE LİSTESİ (2)

| PANO | LİNYE | TÜR | AÇIKLAMA | ADET | GÜÇ (W) | FAZ | SİGORTA | KAÇAK AKIM | KABLO | L (m) | %e |
|---|---|---|---|---|---|---|---|---|---|---|---|
| UTP-2 | A1 | Aydınlatma | Aydınlatma (yüksek tavan, AK: sürekli faz) | 8 | 1.200 | R | B16A | 30 mA | NYM 4x4 mm² | 53,2 | 1,08 |
| UTP-2 | A2 | Aydınlatma | Aydınlatma (yüksek tavan, AK: sürekli faz) | 8 | 1.200 | S | B16A | 30 mA | NYM 4x4 mm² | 54,2 | 1,10 |
| UTP-2 | A3 | Aydınlatma | Aydınlatma (yüksek tavan, AK: sürekli faz) | 6 | 900 | S | B10A | 30 mA | NYM 4x2,5 mm² | 37,3 | 0,91 |
| UTP-2 | A4 | Aydınlatma | Aydınlatma (yüksek tavan, AK: sürekli faz) | 2 | 300 | T | B10A | 30 mA | NYM 4x1,5 mm² | 25,6 | 0,35 |
| UTP-2 | A5 | Aydınlatma | Aydınlatma (yüksek tavan, AK: sürekli faz) | 8 | 1.200 | T | B16A | 30 mA | NYM 4x4 mm² | 62,6 | 1,27 |
| UTP-2 | A6 | Aydınlatma | Aydınlatma (yüksek tavan, AK: sürekli faz) | 8 | 1.200 | R | B16A | 30 mA | NYM 4x4 mm² | 60,1 | 1,22 |
| UTP-2 | A7 | Aydınlatma | Aydınlatma (yüksek tavan, AK: sürekli faz) | 1 | 150 | T | B10A | 30 mA | NYM 4x1,5 mm² | 42,5 | 0,29 |
| UTP-2 | AC8 | Acil ayd. | Acil aydınlatma / yönlendirme | 7 | 21 | T | B10A | 30 mA | NYM 3x1,5 mm² | 105,5 | 0,10 |
| UTP-2 | AC9 | Acil ayd. | Acil aydınlatma / yönlendirme | 1 | 3 | T | B10A | 30 mA | NYM 3x1,5 mm² | 35,9 | 0,00 |
| UTP-2 | G10 | End. priz | End. priz grubu (4P C32+C16+2xB16) | 1 | 5.000 | RST | C32A | 30 mA A tipi (kutu içi) | NYM 5x10 mm² | 20,4 | 0,25 |
| UTP-2 | G11 | End. priz | End. priz grubu (4P C32+C16+2xB16) | 1 | 5.000 | RST | C32A | 30 mA A tipi (kutu içi) | NYM 5x10 mm² | 7,3 | 0,09 |
| UTP-2 | G12 | End. priz | End. priz grubu (4P C32+C16+2xB16) | 1 | 5.000 | RST | C32A | 30 mA A tipi (kutu içi) | NYM 5x10 mm² | 28,9 | 0,36 |
| UTP-2 | G13 | End. priz | End. priz grubu (4P C32+C16+2xB16) | 1 | 5.000 | RST | C32A | 30 mA A tipi (kutu içi) | NYM 5x10 mm² | 31,2 | 0,38 |
| UTP-2 | G14 | End. priz | End. priz grubu (4P C32+C16+2xB16) | 1 | 5.000 | RST | C32A | 30 mA A tipi (kutu içi) | NYM 5x10 mm² | 33,0 | 0,41 |
| UTP-2 | G15 | End. priz | End. priz grubu (4P C32+C16+2xB16) | 1 | 5.000 | RST | C32A | 30 mA A tipi (kutu içi) | NYM 5x10 mm² | 41,5 | 0,51 |
| UTP-2 | G16 | End. priz | End. priz grubu (4P C32+C16+2xB16) | 1 | 5.000 | RST | C32A | 30 mA A tipi (kutu içi) | NYM 5x10 mm² | 43,7 | 0,54 |
| UTP-2 | G17 | End. priz | End. priz grubu (4P C32+C16+2xB16) | 1 | 5.000 | RST | C32A | 30 mA A tipi (kutu içi) | NYM 5x10 mm² | 39,2 | 0,48 |
| UTP-2 | G18 | End. priz | End. priz grubu (4P C32+C16+2xB16) | 1 | 5.000 | RST | C32A | 30 mA A tipi (kutu içi) | NYM 5x10 mm² | 31,7 | 0,39 |
| UTP-2 | K19 | Kuvvet | Aydınlatma kumanda (kontaktör/saat rölesi) | 1 | 50 | T | B10A | 30 mA | NYM 3x1,5 mm² | 3,0 | 0,01 |
| UTP-2 | K20 | Kuvvet | Seksiyonel kapı motoru (L≈25 m kabul) | 1 | 750 | RST | C10A | 300 mA | NYM 5x1,5 mm² | 25,0 | 0,14 |
| IDP-1K | A1 | Aydınlatma | Aydınlatma | 10 | 156 | R | B10A | 30 mA | NYM 3x1,5 mm² | 27,0 | 0,19 |
| IDP-1K | A2 | Aydınlatma | Aydınlatma | 10 | 168 | T | B10A | 30 mA | NYM 3x1,5 mm² | 32,4 | 0,24 |
| IDP-1K | A3 | Aydınlatma | Aydınlatma | 10 | 264 | S | B10A | 30 mA | NYM 3x1,5 mm² | 32,0 | 0,38 |
| IDP-1K | A4 | Aydınlatma | Aydınlatma | 10 | 360 | R | B10A | 30 mA | NYM 3x1,5 mm² | 31,0 | 0,50 |
| IDP-1K | A5 | Aydınlatma | Aydınlatma | 10 | 360 | R | B10A | 30 mA | NYM 3x1,5 mm² | 44,2 | 0,72 |
| IDP-1K | A6 | Aydınlatma | Aydınlatma | 9 | 324 | R | B10A | 30 mA | NYM 3x1,5 mm² | 26,5 | 0,39 |
| IDP-1K | AC7 | Acil ayd. | Acil aydınlatma / yönlendirme | 6 | 18 | T | B10A | 30 mA | NYM 3x1,5 mm² | 39,5 | 0,03 |
| IDP-1K | P8 | Priz | Priz | 6 | 1.800 | S | B16A | 30 mA | NYM 3x2,5 mm² | 20,8 | 1,01 |
| IDP-1K | P9 | Priz | Priz | 6 | 1.800 | T | B16A | 30 mA | NYM 3x2,5 mm² | 25,0 | 1,21 |
| IDP-1K | P10 | Priz | Priz | 6 | 1.800 | S | B16A | 30 mA | NYM 3x4 mm² | 34,2 | 1,04 |
| IDP-1K | P11 | Priz | Priz | 6 | 1.800 | T | B16A | 30 mA | NYM 3x2,5 mm² | 25,0 | 1,21 |
| IDP-1K | P12 | Priz | Priz | 6 | 1.800 | R | B16A | 30 mA | NYM 3x2,5 mm² | 26,4 | 1,28 |
| IDP-1K | P13 | Priz | Priz | 1 | 300 | R | B16A | 30 mA | NYM 3x2,5 mm² | 12,2 | 0,10 |
| IDP-1K | P14 | Priz | Bilgisayar prizi (UPS hazırlığı) | 6 | 1.800 | S | B16A | 30 mA A tipi | NYM 3x2,5 mm² | 27,5 | 1,34 |
| IDP-1K | P15 | Priz | Bilgisayar prizi (UPS hazırlığı) | 6 | 1.800 | T | B16A | 30 mA A tipi | NYM 3x4 mm² | 35,4 | 1,08 |
| IDP-1K | K16 | Kuvvet | Elektrikli termosifon 80 L 2 kW | 1 | 2.000 | R | B16A | 30 mA | NYM 3x2,5 mm² | 7,8 | 0,42 |
| IDP-1K | K17 | Kuvvet | VRF iç üniteleri besleme | 5 | 400 | R | B10A | 30 mA A tipi | NYM 3x1,5 mm² | 37,5 | 0,67 |

## NOTLAR

1- Tesisat Elektrik İç Tesisleri Yönetmeliği, TS HD 60364 ve TS EN 12464-1 esas alınarak hesaplanmıştır.
2- Aydınlatma ve priz tesisatı ayrı paftalarda gösterilmiştir; linye etiketi "PANO/LİNYE", ok yönü panoyu gösterir.
3- Kesitler IEC 60364-5-52 C yöntemi x 0,80 (ofis) / x 0,71 (üretim holü tavası, 40 °C) ile seçilmiştir; gerilim düşümü aydınlatma ve prizde ≤ %1,5, kuvvette ≤ %3 olacak şekilde linyeler bölünmüştür.
4- Kaçak akım: tüm tek fazlı son devreler (priz, aydınlatma, ıslak hacim, özel çıkış) 30 mA, bilgisayar/VRF A tipi; 3 fazlı motor devreleri 300 mA; pano girişleri 300 mA S (seçici) - TS HD 60364-4-41 411.3.3, EMO.
5- Ofis ve ıslak hacimlerde sıva altı spiral boru, üretim alanında galvaniz kablo tavası / boru kullanılacaktır.
6- "AK" acil kitli armatürler kontaktör öncesinden sürekli faz ile beslenir (NYM 4x..: L anahtarlı + L sürekli, TS EN 50172).
7- Acil ve yönlendirme armatürleri 3 saat bataryalıdır (Binaların Yangından Korunması Hakkında Yönetmelik, TS EN 1838).
8- Endüstriyel priz grubu kutusu içinde 4P C32, C16 ve 2xB16 sigortalar ile 30 mA (A tipi) kaçak akım rölesi bulunur.
9- Anahtarlar sahada kapı açılış yönüne göre kapı kanadının arkasında kalmayacak şekilde yerleştirilecektir.
10- Üretim alanı aydınlatması tali panodan kontaktör + saat rölesi ile kumanda edilir.

# HESAP TABLOLARI, CETVELLER VE NOTLAR

ELEKTRİK İÇ TESİSAT PROJESİ - Ölçeksiz

| | |
|---|---|
| İŞİN ADI | ELEKTRİK İÇ TESİSAT PROJESİ |
| YAPI SAHİBİ | BROSCO İTHALAT İHRACAT VE TİCARET ANONİM ŞİRKETİ |
| ADRES | YUKARI MAHALLE / KEMALPAŞA / İZMİR - Ada: ...... Parsel: 5 |
| PAFTA ADI | HESAP TABLOLARI VE NOTLAR |
| ÖLÇEK / TARİH / PAFTA NO | Ölçeksiz \| 19.10.2026 \| 01-05 |
| PROJE MÜELLİFİ | Elektrik Mühendisi - Adı Soyadı: .............................. |
| ODA SİCİL / SMM NO | EMO Sicil No: ............ SMM Belge No: ............ İmza: ............ |