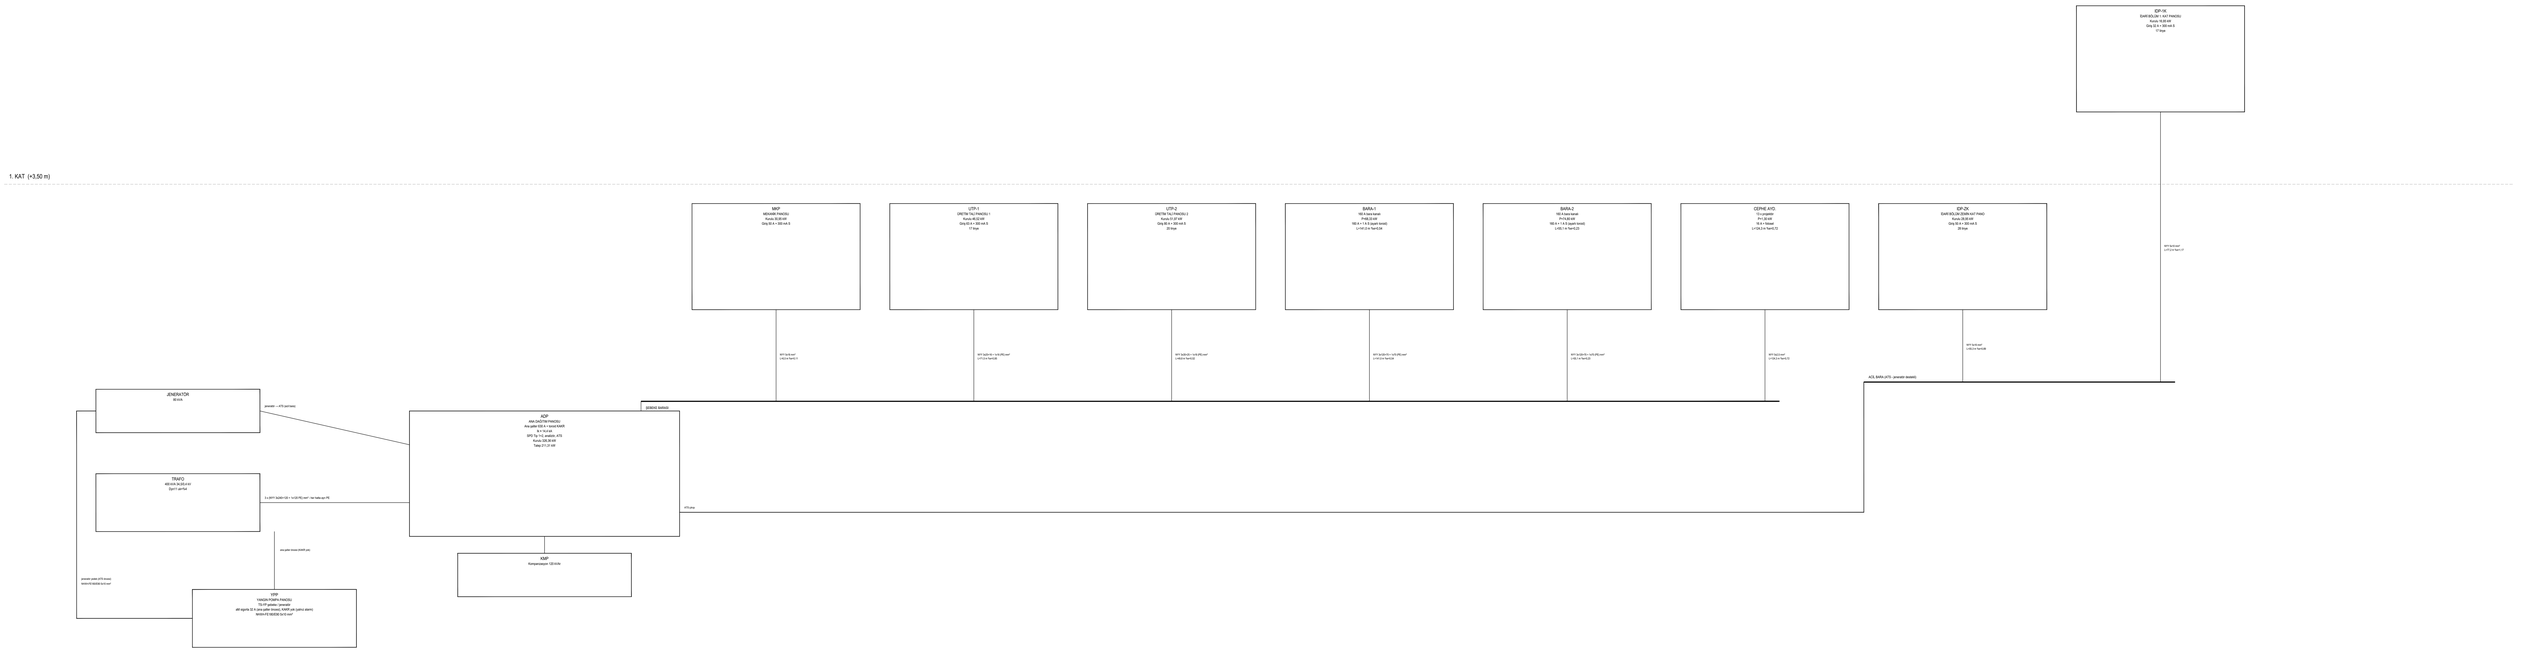


HESAP TABLOLARI, CETVELLER VE NOTLAR

KOLON ŞEMASI (TEK HAT DAĞITIM ŞEMASI) - Örgekaiz

işin adı	KOLON ŞEMASI (TEK HAT DAĞITIM ŞEMASI)
yer adresi	BİRECİK İTHALAT İHRACAT VE TİCARET ANONİM ŞİRKETİ
sahibi	YUKARI MAHALLE, YENİLİ PAZAR CİVARI - Ada: ..., Parsel: 5
müt.yük.	KÖŞAT İNŞ.İLİŞ.VE MÜT.A.Ş.
ölçüm / kontrol yer.	Zeytinli - 0 - 0 m (0,00 ± 1 dk.m)
hesp.yapan	Gökhan Mühendislik - Ahi Hüsam
tarih (ilk) - tadilat	2026 Ocak ay ..... - 2026 Şubat ay ..... - Sayfa .....